AERODROME CHART

ARP
22° 59' 36.466" N
083° 11' 33.907" E

ELEV. : 1941 ft


TWR
118.2 / 118.325

AMBIKAPUR, INDIA

AMBIKAPUR AIRPORT

RWY	DIRECTION	THR. CO-ORDINATES	THR. ELEV.	BEARING STRENGH
16	159°	23°00'03.75607" N 083°11'25.64176" E	1918	34/F/B/W/T
34	339°	22°59'09.20285"N 083°11'48.48073" E	1941	

DATUM: WGS 84
GEOID MODEL: EGM 2008
ELEVATIONS IN FEET
DIMENSIONS IN METRES
RWY BEARINGS ARE MAGNETIC

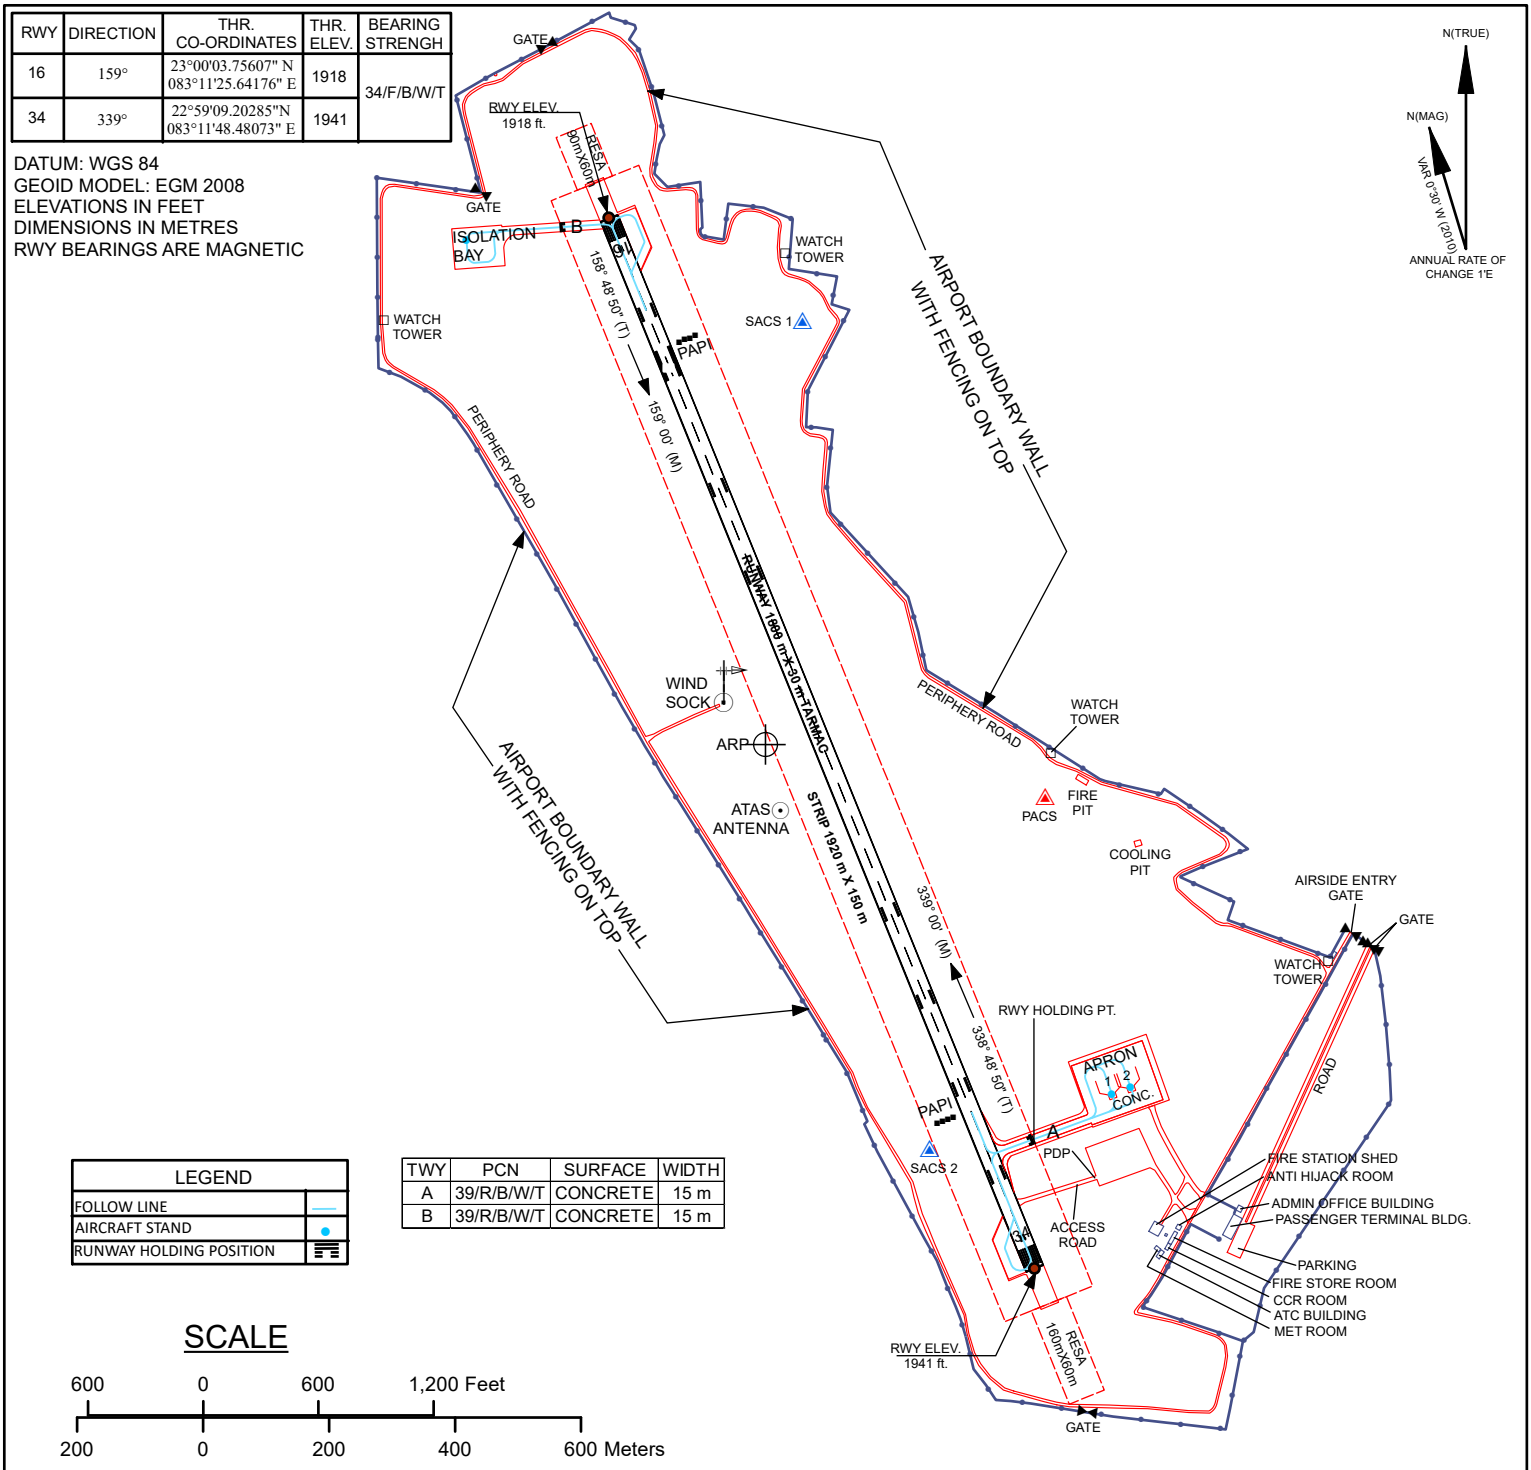


LEGEND	
FOLLOW LINE	
AIRCRAFT STAND	
RUNWAY HOLDING POSITION	

TWY	PCN	SURFACE	WIDTH
A	39/R/B/W/T	CONCRETE	15 m
B	39/R/B/W/T	CONCRETE	15 m

SCALE

600 0 600 1,200 Feet
200 0 200 400 600 Meters

MARKING AIDS RUNWAY 16/34

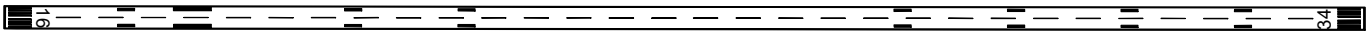

SCALE

0 100 200 400 Meters