
# AERODROME OBSTACLE CHART

TYPE - A (OPERATING LIMITATIONS)

## INDIA / AMBIKAPUR

AMBIKAPUR AIRPORT / RWY 16

ELEVATIONS IN FEET
ALL OTHER DIMENSIONS IN METRES

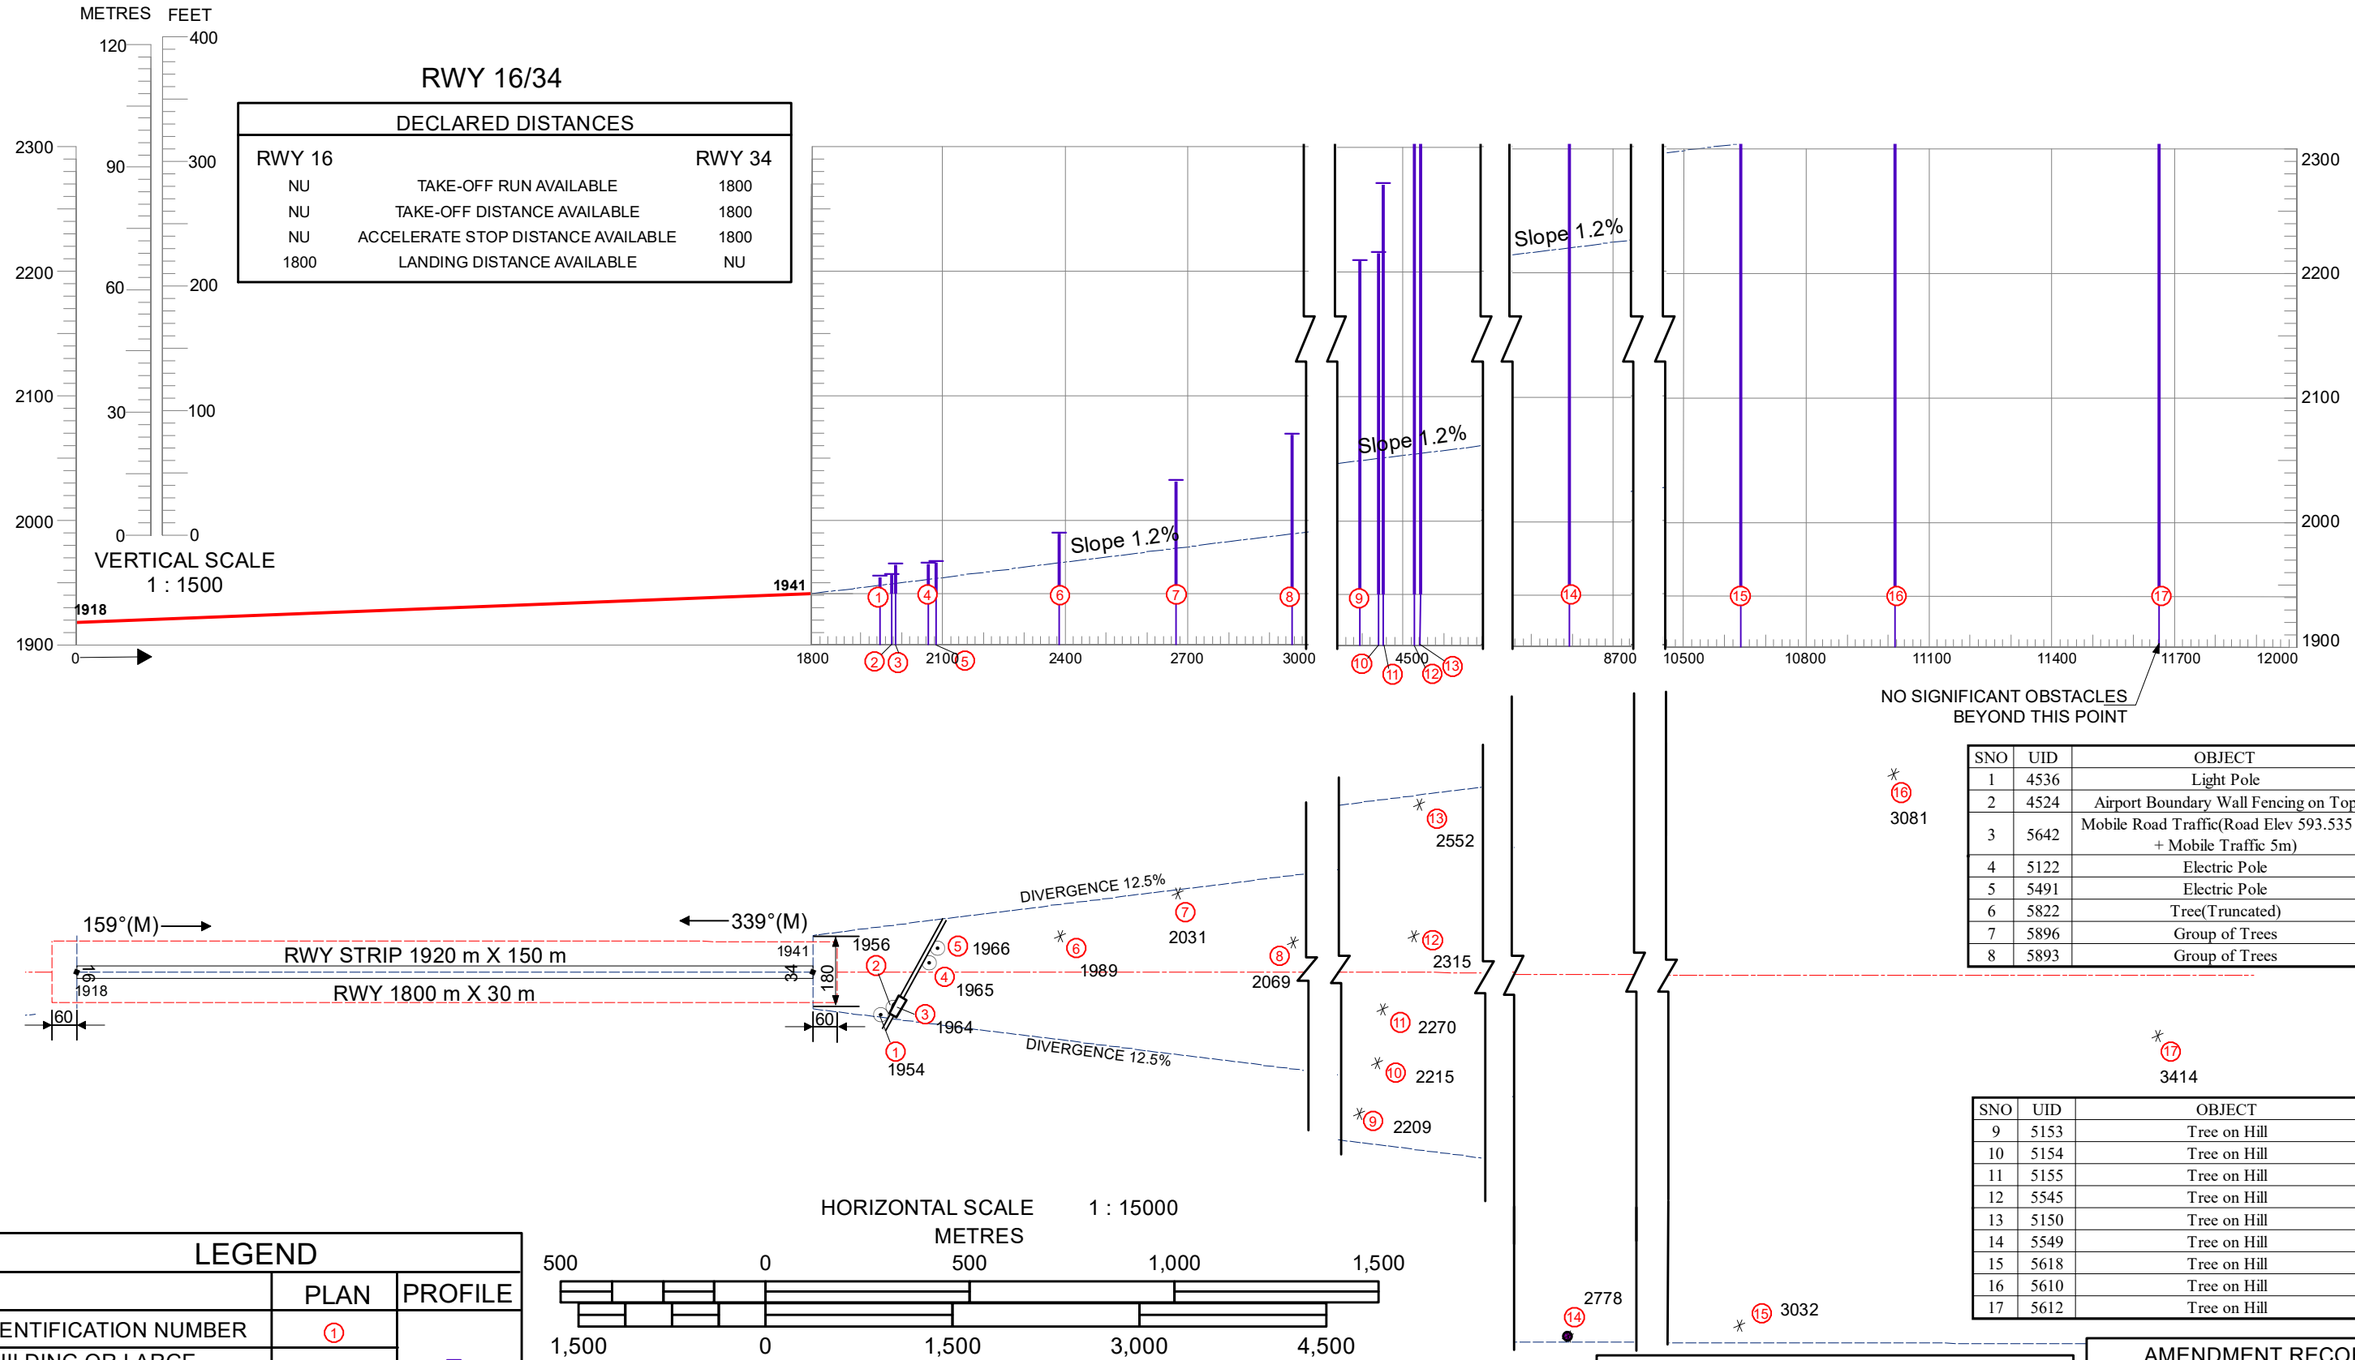


| SNO | UID | OBJECT |
|---|---|---|
| 1 | 4536 | Light Pole |
| 2 | 4524 | Airport Boundary Wall Fencing on Top |
| 3 | 5642 | Mobile Road Traffic(Road Elev 593.535 m + Mobile Traffic 5m) |
| 4 | 5122 | Electric Pole |
| 5 | 5491 | Electric Pole |
| 6 | 5822 | Tree(Truncated) |
| 7 | 5896 | Group of Trees |
| 8 | 5893 | Group of Trees |

| SNO | UID | OBJECT |
|---|---|---|
| 9 | 5153 | Tree on Hill |
| 10 | 5154 | Tree on Hill |
| 11 | 5155 | Tree on Hill |
| 12 | 5545 | Tree on Hill |
| 13 | 5150 | Tree on Hill |
| 14 | 5549 | Tree on Hill |
| 15 | 5618 | Tree on Hill |
| 16 | 5610 | Tree on Hill |
| 17 | 5612 | Tree on Hill |

HORIZONTAL SCALE 1 : 15000
METRES
500 0 500 1,000 1,500
1,500 0 1,500 3,000 4,500
FEET

| LEGEND | PLAN | PROFILE |
|---|---|---|
| IDENTIFICATION NUMBER | ① | |
| BUILDING OR LARGE STRUCTURE | ■ | |
| TREE OR SHRUB | ✳ | |
| MOBILE ROAD TRAFFIC | ═══ | |
| RWY ELEV. (SPOT) | ▪ 1918 | |

| ORDER OF ACCURACY |
|---|
| HORIZONTAL : 3.0 m |
| VERTICAL : 1.0 ft |

NOTES:
1. The objects that have been shielded due to presence of other higher objects have not been shown in this chart.
2. Datum - All Elevations are EGM08.
3. Consult NOTAM for latest information.
4. RWY direction rounded to nearest degree.(Magnetic) (In degree minute:RWY 16/34 = 159°00'/339°00' ) (taken upto 2023)
5. All obstacles shown in this chart are based on Aeronautical Obstacle Survey of March, 2023

| AMENDMENT RECORD | | |
|---|---|---|
| NO. | DATE | ENTERED BY |
| | | |

**AERONAUTICAL INFORMATION UPTO - MAY 2023**

MAP REF. : QA/TA/RWY16/AMB/IN 1/4
DATE OF ISSUE : 06.06.2023
SUPERSEDES DATE : 11.05.2023