
AIRCRAFT PARKING/ DOCKING CHART

APRON ELEV. 1764 ft

TWR MAIN 122.250
STANDBY 132.400

HYDERABAD, INDIA
BEGUMPET AIRPORT

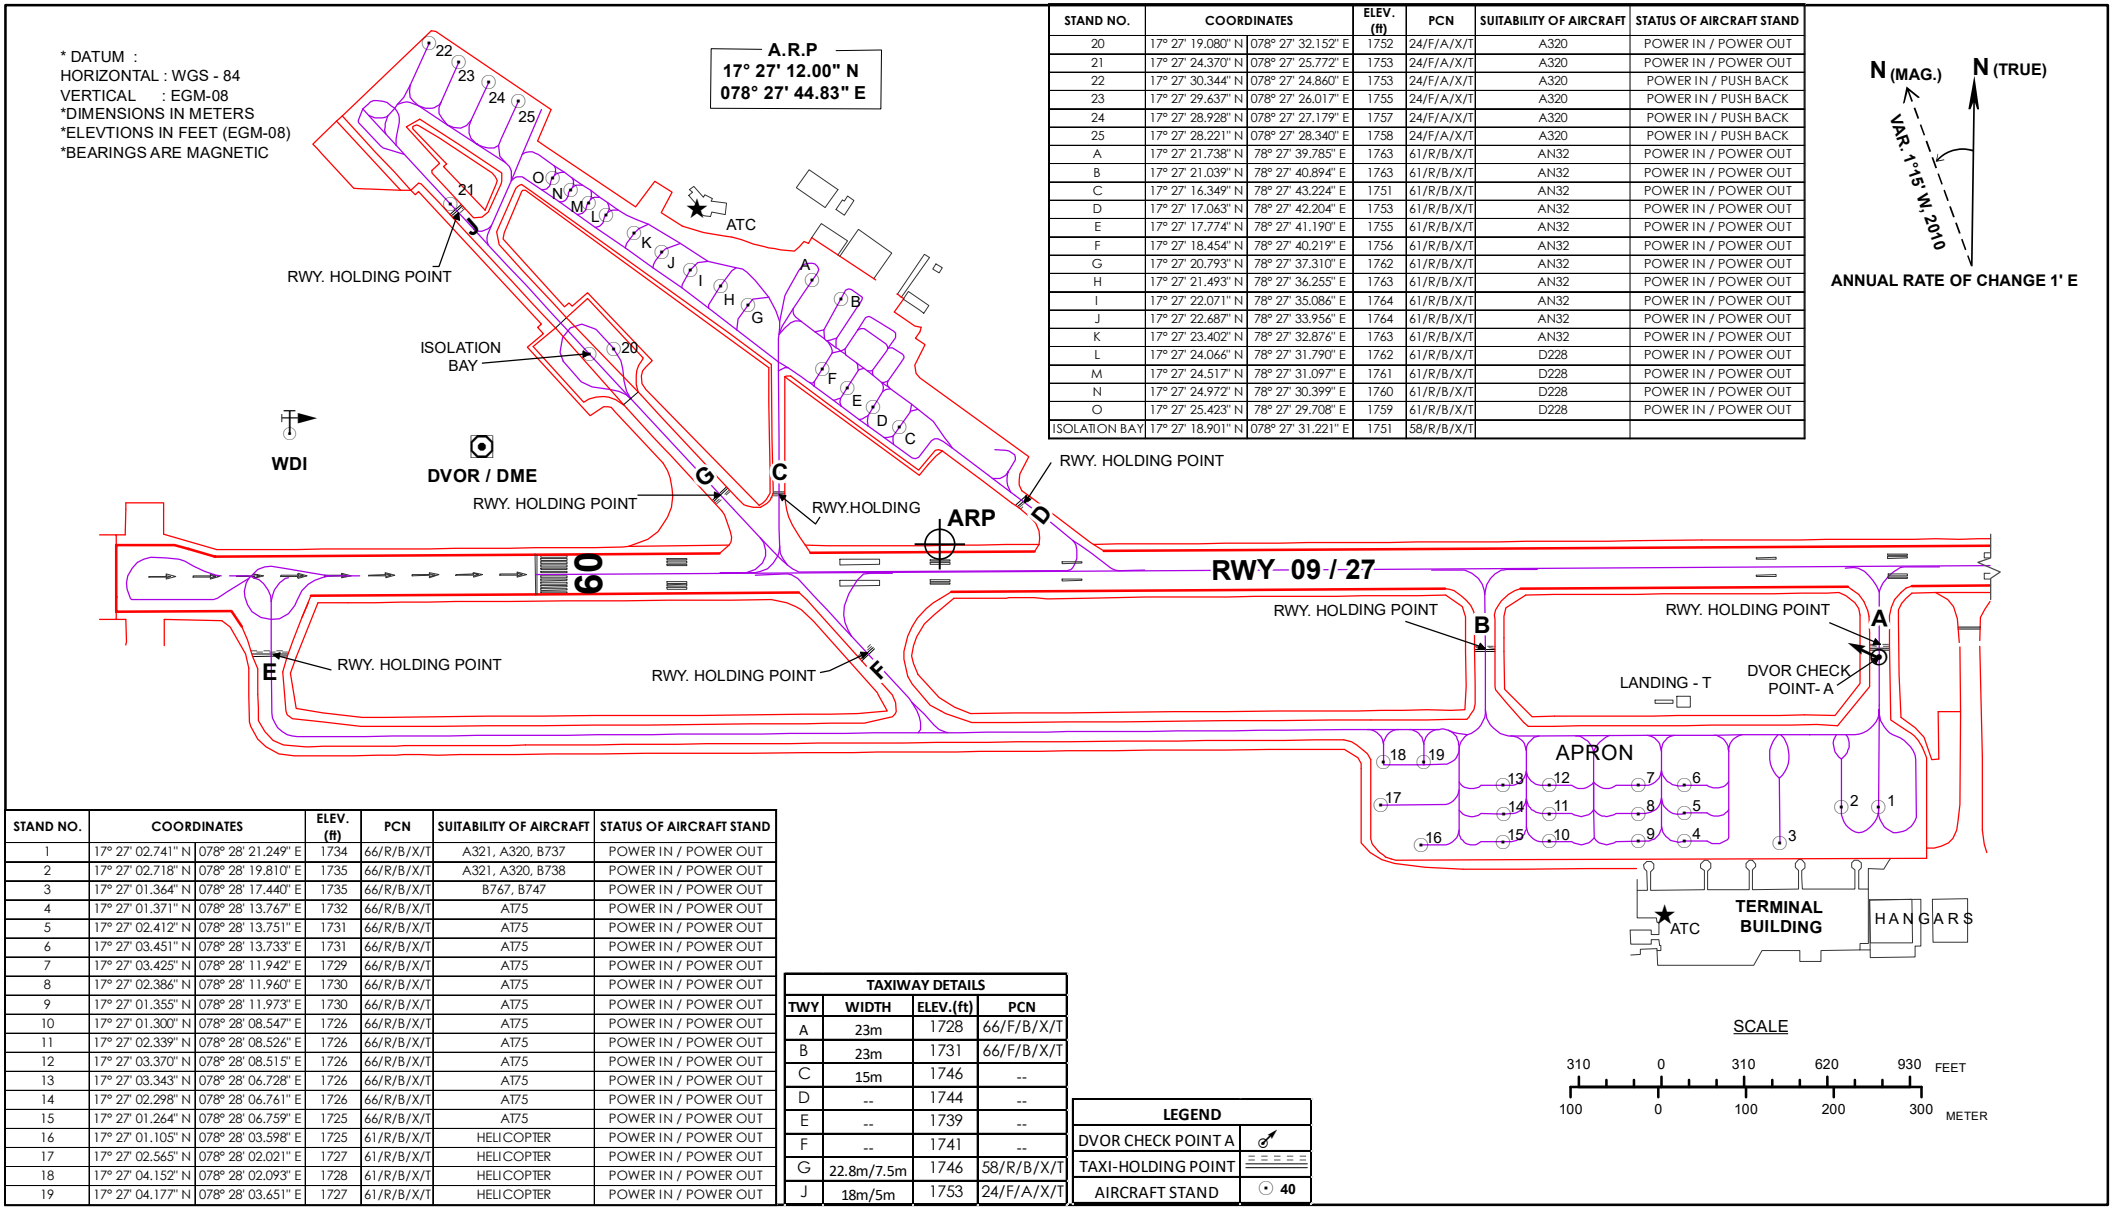

STAND NO.	COORDINATES		ELEV. (ft)	PCN	SUITABILITY OF AIRCRAFT	STATUS OF AIRCRAFT STAND
20	17° 27' 19.080" N	078° 27' 32.152" E	1752	24/F/A/X/T	A320	POWER IN / POWER OUT
21	17° 27' 24.370" N	078° 27' 25.772" E	1753	24/F/A/X/T	A320	POWER IN / POWER OUT
22	17° 27' 30.344" N	078° 27' 24.860" E	1753	24/F/A/X/T	A320	POWER IN / PUSH BACK
23	17° 27' 29.637" N	078° 27' 26.017" E	1755	24/F/A/X/T	A320	POWER IN / PUSH BACK
24	17° 27' 28.928" N	078° 27' 27.179" E	1757	24/F/A/X/T	A320	POWER IN / PUSH BACK
25	17° 27' 28.221" N	078° 27' 28.340" E	1758	24/F/A/X/T	A320	POWER IN / PUSH BACK
A	17° 27' 21.738" N	78° 27' 39.785" E	1763	61/R/B/X/T	AN32	POWER IN / POWER OUT
B	17° 27' 21.039" N	78° 27' 40.894" E	1763	61/R/B/X/T	AN32	POWER IN / POWER OUT
C	17° 27' 16.349" N	78° 27' 43.224" E	1751	61/R/B/X/T	AN32	POWER IN / POWER OUT
D	17° 27' 17.063" N	78° 27' 42.204" E	1753	61/R/B/X/T	AN32	POWER IN / POWER OUT
E	17° 27' 17.774" N	78° 27' 41.190" E	1755	61/R/B/X/T	AN32	POWER IN / POWER OUT
F	17° 27' 18.454" N	78° 27' 40.219" E	1756	61/R/B/X/T	AN32	POWER IN / POWER OUT
G	17° 27' 20.793" N	78° 27' 37.310" E	1762	61/R/B/X/T	AN32	POWER IN / POWER OUT
H	17° 27' 21.493" N	78° 27' 36.255" E	1763	61/R/B/X/T	AN32	POWER IN / POWER OUT
I	17° 27' 22.071" N	78° 27' 35.086" E	1764	61/R/B/X/T	AN32	POWER IN / POWER OUT
J	17° 27' 22.687" N	78° 27' 33.956" E	1764	61/R/B/X/T	AN32	POWER IN / POWER OUT
K	17° 27' 23.402" N	78° 27' 32.876" E	1763	61/R/B/X/T	AN32	POWER IN / POWER OUT
L	17° 27' 24.066" N	78° 27' 31.790" E	1762	61/R/B/X/T	D228	POWER IN / POWER OUT
M	17° 27' 24.517" N	78° 27' 31.097" E	1761	61/R/B/X/T	D228	POWER IN / POWER OUT
N	17° 27' 24.972" N	78° 27' 30.399" E	1760	61/R/B/X/T	D228	POWER IN / POWER OUT
O	17° 27' 25.423" N	78° 27' 29.708" E	1759	61/R/B/X/T	D228	POWER IN / POWER OUT
ISOLATION BAY	17° 27' 18.901" N	078° 27' 31.221" E	1751	58/R/B/X/T		

STAND NO.	COORDINATES		ELEV. (ft)	PCN	SUITABILITY OF AIRCRAFT	STATUS OF AIRCRAFT STAND
1	17° 27' 02.741" N	078° 28' 21.249" E	1734	66/R/B/X/T	A321, A320, B737	POWER IN / POWER OUT
2	17° 27' 02.718" N	078° 28' 19.810" E	1735	66/R/B/X/T	A321, A320, B738	POWER IN / POWER OUT
3	17° 27' 01.364" N	078° 28' 17.440" E	1735	66/R/B/X/T	B767, B747	POWER IN / POWER OUT
4	17° 27' 01.371" N	078° 28' 13.767" E	1732	66/R/B/X/T	AT75	POWER IN / POWER OUT
5	17° 27' 02.412" N	078° 28' 13.751" E	1731	66/R/B/X/T	AT75	POWER IN / POWER OUT
6	17° 27' 03.451" N	078° 28' 13.733" E	1731	66/R/B/X/T	AT75	POWER IN / POWER OUT
7	17° 27' 03.425" N	078° 28' 11.942" E	1729	66/R/B/X/T	AT75	POWER IN / POWER OUT
8	17° 27' 02.386" N	078° 28' 11.960" E	1730	66/R/B/X/T	AT75	POWER IN / POWER OUT
9	17° 27' 01.355" N	078° 28' 11.973" E	1730	66/R/B/X/T	AT75	POWER IN / POWER OUT
10	17° 27' 01.300" N	078° 28' 08.547" E	1726	66/R/B/X/T	AT75	POWER IN / POWER OUT
11	17° 27' 02.339" N	078° 28' 08.526" E	1726	66/R/B/X/T	AT75	POWER IN / POWER OUT
12	17° 27' 03.370" N	078° 28' 08.515" E	1726	66/R/B/X/T	AT75	POWER IN / POWER OUT
13	17° 27' 03.343" N	078° 28' 06.728" E	1726	66/R/B/X/T	AT75	POWER IN / POWER OUT
14	17° 27' 02.298" N	078° 28' 06.761" E	1726	66/R/B/X/T	AT75	POWER IN / POWER OUT
15	17° 27' 01.264" N	078° 28' 06.759" E	1725	66/R/B/X/T	AT75	POWER IN / POWER OUT
16	17° 27' 01.105" N	078° 28' 03.598" E	1725	61/R/B/X/T	HELICOPTER	POWER IN / POWER OUT
17	17° 27' 02.565" N	078° 28' 02.021" E	1727	61/R/B/X/T	HELICOPTER	POWER IN / POWER OUT
18	17° 27' 04.152" N	078° 28' 02.093" E	1728	61/R/B/X/T	HELICOPTER	POWER IN / POWER OUT
19	17° 27' 04.177" N	078° 28' 03.651" E	1727	61/R/B/X/T	HELICOPTER	POWER IN / POWER OUT

TAXIWAY DETAILS			
TWY	WIDTH	ELEV.(ft)	PCN
A	23m	1728	66/F/B/X/T
B	23m	1731	66/F/B/X/T
C	15m	1746	--
D	--	1744	--
E	--	1739	--
F	--	1741	--
G	22.8m/7.5m	1746	58/R/B/X/T
J	18m/5m	1753	24/F/A/X/T

LEGEND	
DVOR CHECK POINT A	
TAXI-HOLDING POINT	
AIRCRAFT STAND	40

DATE OF AERONAUTICAL INFORMATION
MARCH, 2025

AIRPORT AUTHORITY OF INDIA

DRG. NO. AAI-08 / PDC / 2025, (CARTO)