
AERODROME ELEVATION 2915 ft.

DISTANCE IN METRE.
ELEVATION IN FEET(EGM-08).
GRID LINES AND CO-ORDINATES SHOWN ARE BASED ON WGS-84 DATUM.
UTM ZONE-43N

AERODROME OBSTACLE CHART
TYPE - B

BENGALURU(HAL),INDIA
BENGALURU AIRPORT(HAL)

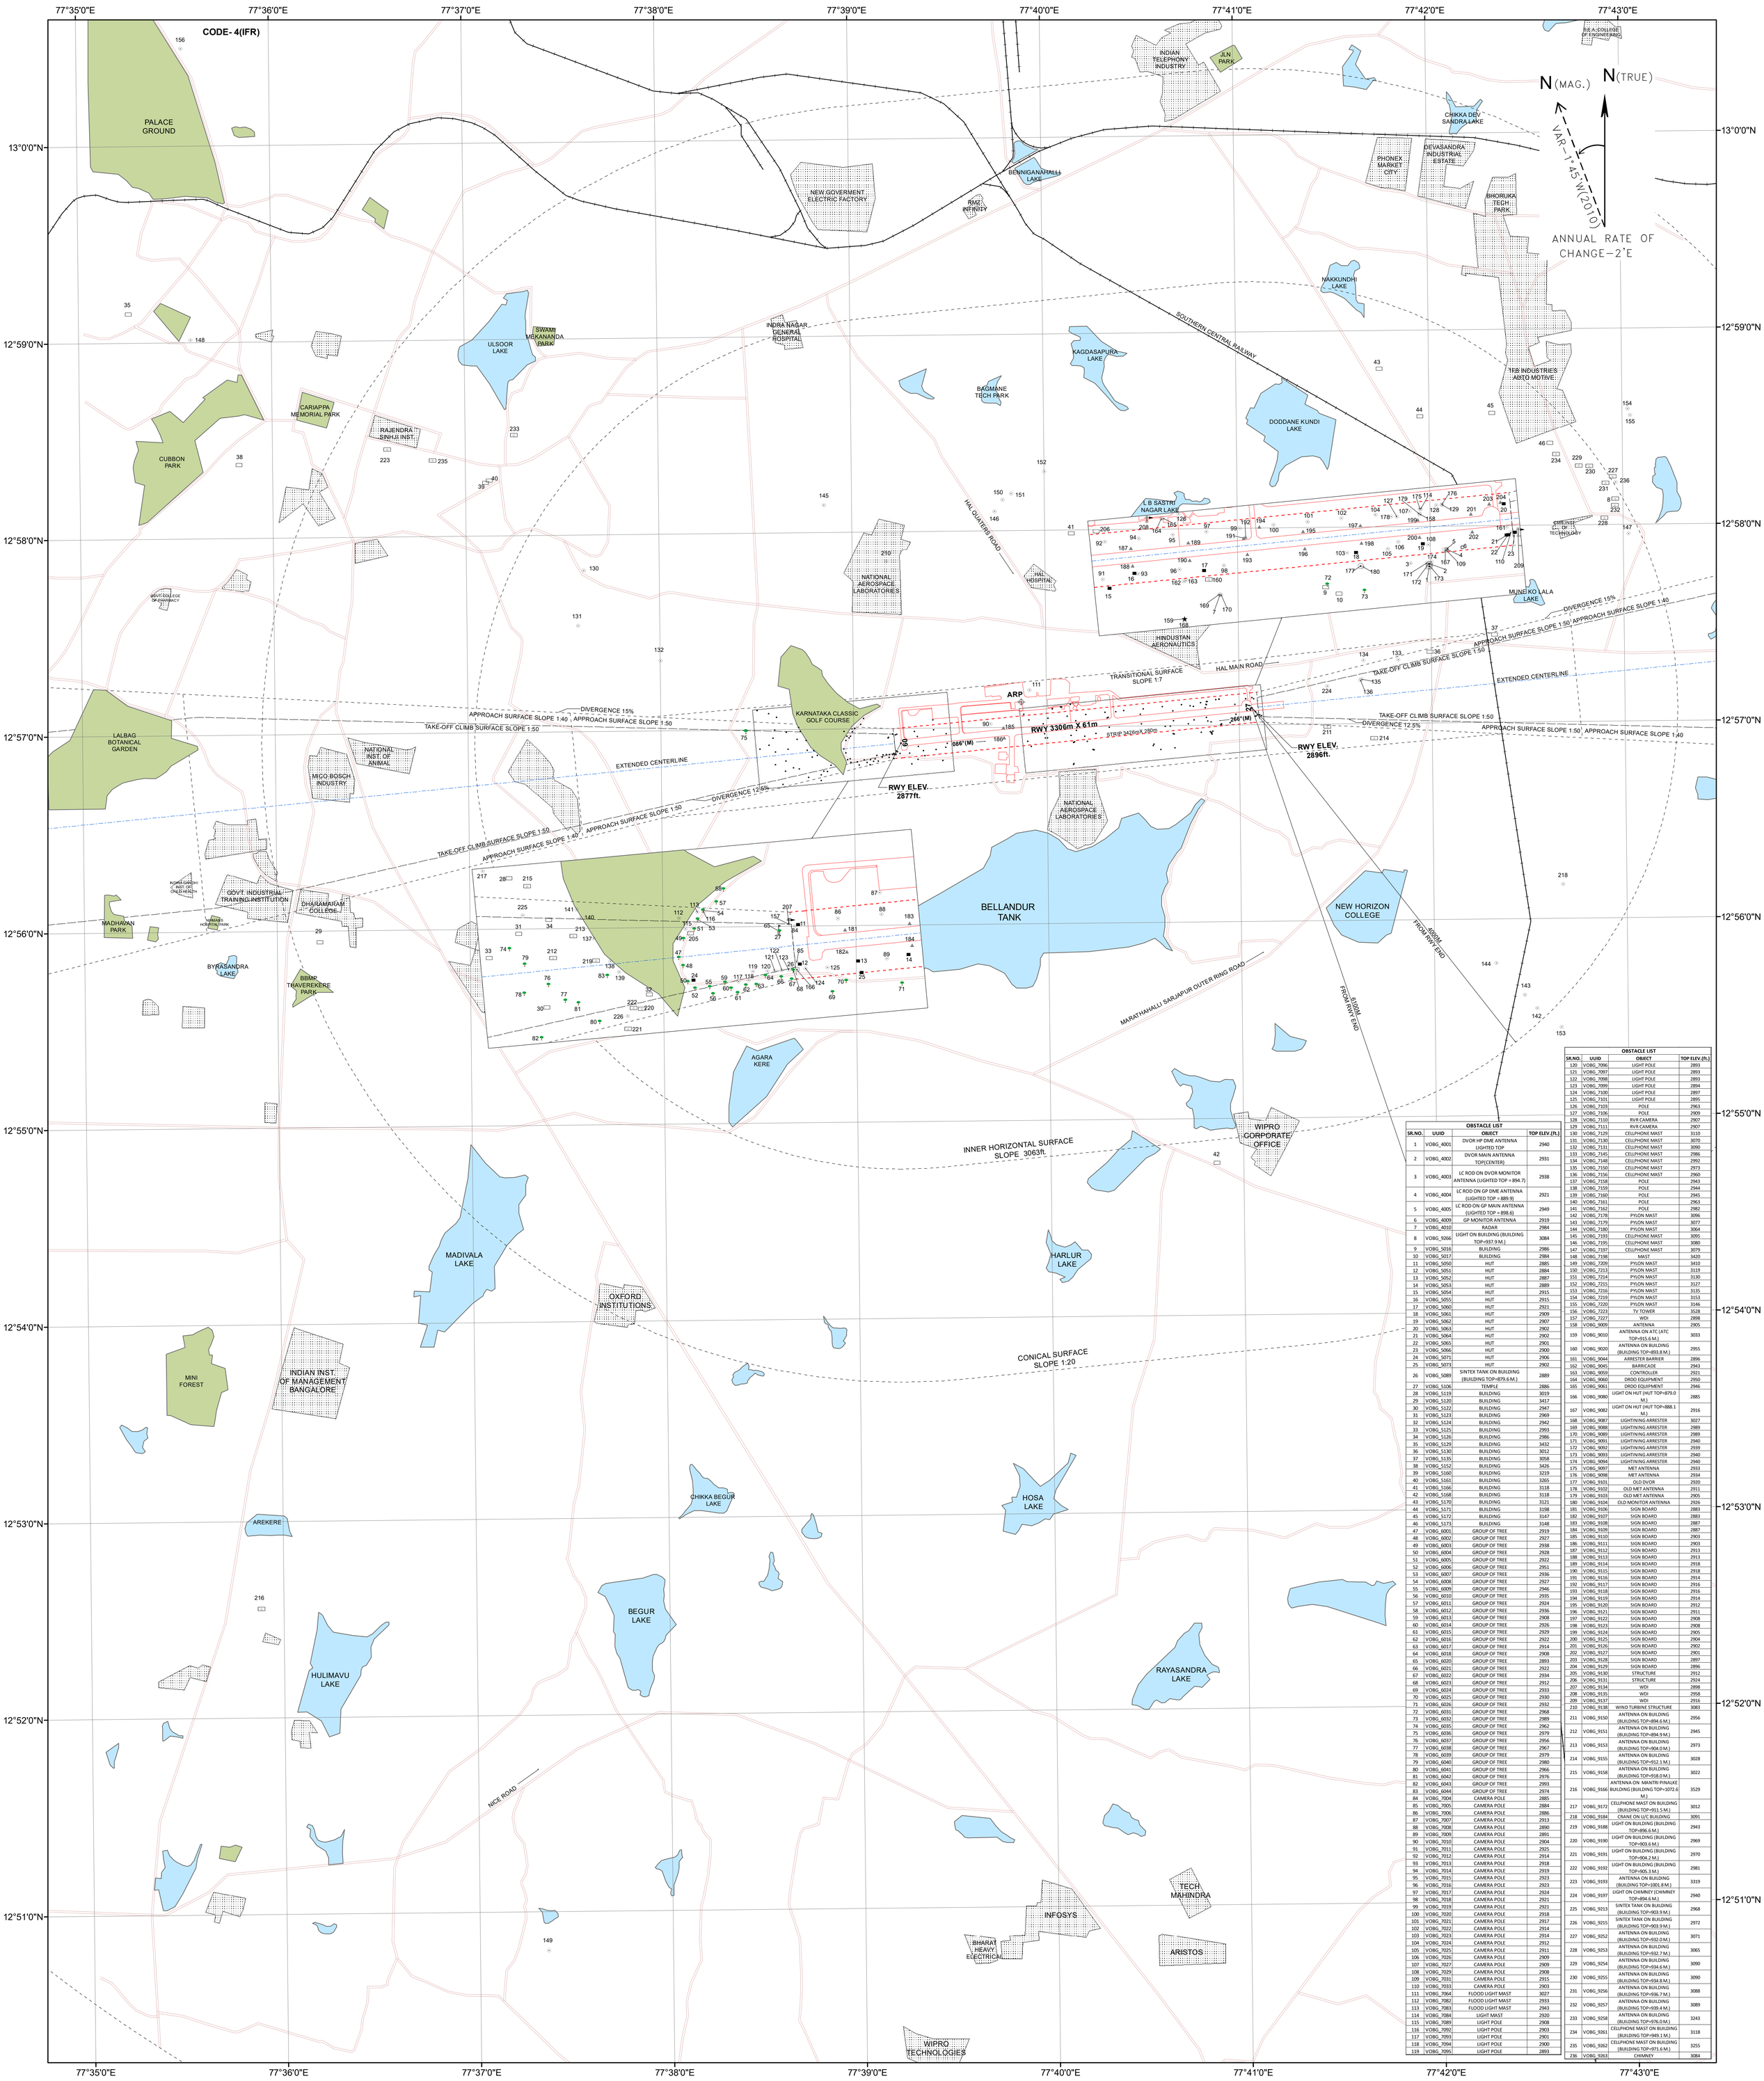

OBSTACLE LIST			
SR.NO.	UUID	OBJECT	TOP ELEV.(ft.)
1	VOBG_4001	DVOR HP DME ANTENNA LIGHTED TOP	2940
2	VOBG_4002	DVOR MAIN ANTENNA TOP(CENTER)	2931
3	VOBG_4003	LC ROD ON DVOR MONITOR ANTENNA (LIGHTED TOP = 894.7)	2938
4	VOBG_4004	LC ROD ON GP DME ANTENNA (LIGHTED TOP = 889.9)	2921
5	VOBG_4005	LC ROD ON GP MAIN ANTENNA (LIGHTED TOP = 898.6)	2949
6	VOBG_4009	GP MONITOR ANTENNA	2919
7	VOBG_4010	RADAR	2984
8	VOBG_9266	LIGHT ON BUILDING (BUILDING TOP=937.9 M.)	3084
9	VOBG_5016	BUILDING	2986
10	VOBG_5017	BUILDING	2984
11	VOBG_5050	HUT	2885
12	VOBG_5051	HUT	2884
13	VOBG_5052	HUT	2887
14	VOBG_5053	HUT	2889
15	VOBG_5054	HUT	2915
16	VOBG_5055	HUT	2915
17	VOBG_5060	HUT	2921
18	VOBG_5061	HUT	2909
19	VOBG_5062	HUT	2907
20	VOBG_5063	HUT	2902
21	VOBG_5064	HUT	2902
22	VOBG_5065	HUT	2901
23	VOBG_5066	HUT	2900
24	VOBG_5071	HUT	2906
25	VOBG_5073	HUT	2902
26	VOBG_5089	SINTEX TANK ON BUILDING (BUILDING TOP=879.6 M.)	2889
27	VOBG_5106	TEMPLE	2886
28	VOBG_5119	BUILDING	3019
29	VOBG_5120	BUILDING	3417
30	VOBG_5122	BUILDING	2947
31	VOBG_5123	BUILDING	2969
32	VOBG_5124	BUILDING	2942
33	VOBG_5125	BUILDING	2993
34	VOBG_5126	BUILDING	2986
35	VOBG_5129	BUILDING	3432
36	VOBG_5130	BUILDING	3012
37	VOBG_5135	BUILDING	3058
38	VOBG_5152	BUILDING	3426
39	VOBG_5160	BUILDING	3219
40	VOBG_5161	BUILDING	3265
41	VOBG_5166	BUILDING	3118
42	VOBG_5168	BUILDING	3118
43	VOBG_5170	BUILDING	3121
44	VOBG_5171	BUILDING	3198
45	VOBG_5172	BUILDING	3147
46	VOBG_5173	BUILDING	3148
47	VOBG_6001	GROUP OF TREE	2919
48	VOBG_6002	GROUP OF TREE	2927
49	VOBG_6003	GROUP OF TREE	2938
50	VOBG_6004	GROUP OF TREE	2928
51	VOBG_6005	GROUP OF TREE	2922
52	VOBG_6006	GROUP OF TREE	2951
53	VOBG_6007	GROUP OF TREE	2936
54	VOBG_6008	GROUP OF TREE	2927
55	VOBG_6009	GROUP OF TREE	2946
56	VOBG_6010	GROUP OF TREE	2935
57	VOBG_6011	GROUP OF TREE	2924
58	VOBG_6012	GROUP OF TREE	2936
59	VOBG_6013	GROUP OF TREE	2908
60	VOBG_6014	GROUP OF TREE	2926
61	VOBG_6015	GROUP OF TREE	2929
62	VOBG_6016	GROUP OF TREE	2922
63	VOBG_6017	GROUP OF TREE	2914
64	VOBG_6018	GROUP OF TREE	2908
65	VOBG_6020	GROUP OF TREE	2893
66	VOBG_6021	GROUP OF TREE	2922
67	VOBG_6022	GROUP OF TREE	2934
68	VOBG_6023	GROUP OF TREE	2912
69	VOBG_6024	GROUP OF TREE	2933
70	VOBG_6025	GROUP OF TREE	2930
71	VOBG_6026	GROUP OF TREE	2932
72	VOBG_6031	GROUP OF TREE	2968
73	VOBG_6032	GROUP OF TREE	2989
74	VOBG_6035	GROUP OF TREE	2962
75	VOBG_6036	GROUP OF TREE	2979
76	VOBG_6037	GROUP OF TREE	2956
77	VOBG_6038	GROUP OF TREE	2967
78	VOBG_6039	GROUP OF TREE	2979
79	VOBG_6040	GROUP OF TREE	2980
80	VOBG_6041	GROUP OF TREE	2966
81	VOBG_6042	GROUP OF TREE	2976
82	VOBG_6043	GROUP OF TREE	2993
83	VOBG_6044	GROUP OF TREE	2974
84	VOBG_7004	CAMERA POLE	2885
85	VOBG_7005	CAMERA POLE	2884
86	VOBG_7006	CAMERA POLE	2886
87	VOBG_7007	CAMERA POLE	2913
88	VOBG_7008	CAMERA POLE	2890
89	VOBG_7009	CAMERA POLE	2891
90	VOBG_7010	CAMERA POLE	2904
91	VOBG_7011	CAMERA POLE	2925
92	VOBG_7012	CAMERA POLE	2914
93	VOBG_7013	CAMERA POLE	2918
94	VOBG_7014	CAMERA POLE	2919
95	VOBG_7015	CAMERA POLE	2923
96	VOBG_7016	CAMERA POLE	2923
97	VOBG_7017	CAMERA POLE	2924
98	VOBG_7018	CAMERA POLE	2921
99	VOBG_7019	CAMERA POLE	2921
100	VOBG_7020	CAMERA POLE	2918
101	VOBG_7021	CAMERA POLE	2917
102	VOBG_7022	CAMERA POLE	2914
103	VOBG_7023	CAMERA POLE	2914
104	VOBG_7024	CAMERA POLE	2912
105	VOBG_7025	CAMERA POLE	2911
106	VOBG_7026	CAMERA POLE	2909
107	VOBG_7027	CAMERA POLE	2909
108	VOBG_7029	CAMERA POLE	2908
109	VOBG_7031	CAMERA POLE	2915
110	VOBG_7033	CAMERA POLE	2903
111	VOBG_7064	FLOOD LIGHT MAST	3027
112	VOBG_7082	FLOOD LIGHT MAST	2933
113	VOBG_7083	FLOOD LIGHT MAST	2943
114	VOBG_7084	LIGHT MAST	2920
115	VOBG_7089	LIGHT POLE	2908
116	VOBG_7092	LIGHT POLE	2903
117	VOBG_7093	LIGHT POLE	2901
118	VOBG_7094	LIGHT POLE	2900
119	VOBG_7095	LIGHT POLE	2893
120	VOBG_7096	LIGHT POLE	2893
121	VOBG_7097	LIGHT POLE	2893
122	VOBG_7098	LIGHT POLE	2893
123	VOBG_7099	LIGHT POLE	2894
124	VOBG_7100	LIGHT POLE	2897
125	VOBG_7101	LIGHT POLE	2895
126	VOBG_7103	POLE	2963
127	VOBG_7106	POLE	2909
128	VOBG_7110	RVR CAMERA	2907
129	VOBG_7111	RVR CAMERA	2907
130	VOBG_7129	CELLPHONE MAST	3110
131	VOBG_7130	CELLPHONE MAST	3070
132	VOBG_7131	CELLPHONE MAST	3090
133	VOBG_7145	CELLPHONE MAST	2986
134	VOBG_7148	CELLPHONE MAST	2992
135	VOBG_7150	CELLPHONE MAST	2973
136	VOBG_7156	CELLPHONE MAST	2960
137	VOBG_7158	POLE	2943
138	VOBG_7159	POLE	2944
139	VOBG_7160	POLE	2945
140	VOBG_7161	POLE	2963
141	VOBG_7162	POLE	2982
142	VOBG_7178	PYLON MAST	3096
143	VOBG_7179	PYLON MAST	3077
144	VOBG_7180	PYLON MAST	3064
145	VOBG_7193	CELLPHONE MAST	3095
146	VOBG_7195	CELLPHONE MAST	3080
147	VOBG_7197	CELLPHONE MAST	3079
148	VOBG_7198	MAST	3420
149	VOBG_7209	PYLON MAST	3410
150	VOBG_7213	PYLON MAST	3119
151	VOBG_7214	PYLON MAST	3130
152	VOBG_7215	PYLON MAST	3127
153	VOBG_7216	PYLON MAST	3135
154	VOBG_7219	PYLON MAST	3153
155	VOBG_7220	PYLON MAST	3146
156	VOBG_7223	TV TOWER	3528
157	VOBG_7227	WDI	2898
158	VOBG_9009	ANTENNA	2905
159	VOBG_9010	ANTENNA ON ATC (ATC TOP=915.6 M.)	3033
160	VOBG_9020	ANTENNA ON BUILDING (BUILDING TOP=893.8 M.)	2955
161	VOBG_9044	ARRESTER BARRIER	2896
162	VOBG_9045	BARRICADE	2943
163	VOBG_9059	CONTROLLER	2921
164	VOBG_9060	DRDO EQUIPMENT	2950
165	VOBG_9061	DRDO EQUIPMENT	2946
166	VOBG_9080	LIGHT ON HUT (HUT TOP=879.0 M.)	2885
167	VOBG_9082	LIGHT ON HUT (HUT TOP=888.1 M.)	2916
168	VOBG_9087	LIGHTNING ARRESTER	3027
169	VOBG_9088	LIGHTNING ARRESTER	2989
170	VOBG_9089	LIGHTNING ARRESTER	2989
171	VOBG_9091	LIGHTNING ARRESTER	2940
172	VOBG_9092	LIGHTNING ARRESTER	2939
173	VOBG_9093	LIGHTNING ARRESTER	2940
174	VOBG_9094	LIGHTNING ARRESTER	2940
175	VOBG_9097	MET ANTENNA	2933
176	VOBG_9098	MET ANTENNA	2934
177	VOBG_9101	OLD DVOR	2920
178	VOBG_9102	OLD MET ANTENNA	2911
179	VOBG_9103	OLD MET ANTENNA	2905
180	VOBG_9104	OLD MONITOR ANTENNA	2926
181	VOBG_9106	SIGN BOARD	2883
182	VOBG_9107	SIGN BOARD	2883
183	VOBG_9108	SIGN BOARD	2887
184	VOBG_9109	SIGN BOARD	2887
185	VOBG_9110	SIGN BOARD	2903
186	VOBG_9111	SIGN BOARD	2903
187	VOBG_9112	SIGN BOARD	2913
188	VOBG_9113	SIGN BOARD	2913
189	VOBG_9114	SIGN BOARD	2918
190	VOBG_9115	SIGN BOARD	2918
191	VOBG_9116	SIGN BOARD	2914
192	VOBG_9117	SIGN BOARD	2916
193	VOBG_9118	SIGN BOARD	2916
194	VOBG_9119	SIGN BOARD	2914
195	VOBG_9120	SIGN BOARD	2912
196	VOBG_9121	SIGN BOARD	2911
197	VOBG_9122	SIGN BOARD	2908
198	VOBG_9123	SIGN BOARD	2908
199	VOBG_9124	SIGN BOARD	2905
200	VOBG_9125	SIGN BOARD	2904
201	VOBG_9126	SIGN BOARD	2902
202	VOBG_9127	SIGN BOARD	2901
203	VOBG_9128	SIGN BOARD	2897
204	VOBG_9129	SIGN BOARD	2896
205	VOBG_9130	STRUCTURE	2912
206	VOBG_9131	STRUCTURE	2924
207	VOBG_9134	WDI	2898
208	VOBG_9135	WDI	2958
209	VOBG_9137	WDI	2916
210	VOBG_9138	WIND TURBINE STRUCTURE	3083
211	VOBG_9150	ANTENNA ON BUILDING (BUILDING TOP=894.6 M.)	2956
212	VOBG_9151	ANTENNA ON BUILDING (BUILDING TOP=894.9 M.)	2945
213	VOBG_9153	ANTENNA ON BUILDING (BUILDING TOP=904.0 M.)	2973
214	VOBG_9155	ANTENNA ON BUILDING (BUILDING TOP=912.1 M.)	3028
215	VOBG_9158	ANTENNA ON BUILDING (BUILDING TOP=918.0 M.)	3022
216	VOBG_9166	ANTENNA ON MANTRI PINALKE BUILDING (BUILDING TOP=1072.6 M.)	3529
217	VOBG_9172	CELLPHONE MAST ON BUILDING (BUILDING TOP=911.5 M.)	3012
218	VOBG_9184	CRANE ON U/C BUILDING	3091
219	VOBG_9188	LIGHT ON BUILDING (BUILDING TOP=896.6 M.)	2943
220	VOBG_9190	LIGHT ON BUILDING (BUILDING TOP=903.6 M.)	2969
221	VOBG_9191	LIGHT ON BUILDING (BUILDING TOP=924.2 M.)	2970
222	VOBG_9192	LIGHT ON BUILDING (BUILDING TOP=905.3 M.)	2981
223	VOBG_9193	ANTENNA ON BUILDING (BUILDING TOP=1001.8 M.)	3319
224	VOBG_9197	LIGHT ON CHIMNEY (CHIMNEY TOP=894.6 M.)	2940
225	VOBG_9213	SINTEX TANK ON BUILDING (BUILDING TOP=903.9 M.)	2968
226	VOBG_9215	SINTEX TANK ON BUILDING (BUILDING TOP=903.9 M.)	2972
227	VOBG_9252	ANTENNA ON BUILDING (BUILDING TOP=932.0 M.)	3071
228	VOBG_9253	ANTENNA ON BUILDING (BUILDING TOP=932.7 M.)	3065
229	VOBG_9254	ANTENNA ON BUILDING (BUILDING TOP=934.6 M.)	3090
230	VOBG_9255	ANTENNA ON BUILDING (BUILDING TOP=934.8 M.)	3090
231	VOBG_9256	ANTENNA ON BUILDING (BUILDING TOP=936.7 M.)	3088
232	VOBG_9257	ANTENNA ON BUILDING (BUILDING TOP=939.4 M.)	3089
233	VOBG_9258	ANTENNA ON BUILDING (BUILDING TOP=976.0 M.)	3243
234	VOBG_9261	CELLPHONE MAST ON BUILDING (BUILDING TOP=949.1 M.)	3118
235	VOBG_9262	CELLPHONE MAST ON BUILDING (BUILDING TOP=971.6 M.)	3255
236	VOBG_9263	CHIMNEY	3084

LEGEND

AERODROME REFRENCE POINT 12°57'07.83"N 077°39'51.90"E	⊕
RAILWAY TRACK	
ROADS	
PARK	
WATERBODIES	
BUILD-UP AREA	

ORDER OF ACCURACY	
TAKE-OFF AND APPROACH AREAS	
HORIZONTAL	REMARK
5M	AT POINT OF ORIGIN INCREASING AT A RATE OF 1 PER 500.
VERTICAL	REMARK
0.5M	IN THE FIRST 300M AND INCREASING AT A RATE OF 1 PER 1000.
OTHER AREAS	
HORIZONTAL	REMARK
5M	WITHIN 5000M OF THE ARP AND 12M BEYOND THAT AREA.
VERTICAL	REMARK
1M	WITHIN 1500M OF THE ARP INCREASING AT A RATE OF 1 PER 1000.

SCALE 1:20,000

METRES 500 0 500 1000 1500 2000 2500

FEET 2000 0 2000 4000 6000 8000 10000

NOTE :

1.OBSTACLES SHOWN ARE THOSE WHICH PENETRATE THE SURFACES SPECIFIED IN ANNEX 14, VOL-1, CHAPTER-4 & GSR.
2.TORA FOR RWY 09 IS 3306M.
TORA FOR RWY27 IS 3306M.
3.TO BRING OUT THE CLEARITY IN THE OBSTACLES DEPICTED IN THE APPROACH AND TAKE-OFF SURFACE, ONLY HIGHER OBSTACLES HAVE BEEN SHOWN FROM GROUP OF OBSTACLES.
4.ALL OBSTACLES ARE SHOWN IN THE CHART BASED ON AERONAUTICAL SURVEY NOV. 2025.
5.TOPOGRAPHIC FEATURES SOURCE- WORLD TOPO MAP, ESRI.

AMENDMENT RECORD		
NO.	DATE	ENTERED BY

AERONAUTICAL INFORMATION UPTO: MARCH.2026

AAI DRG.NO.-05/BENGALURU(HAL)/2026(CARTO)