AIRCRAFT PARKING/ DOCKING CHART

APRON-I ELEV. 2917 ft.
APRON-II ELEV. 2941 ft.
APRON-IV ELEV. 2935 ft.
APRON-V ELEV. 2929 ft.
APRON-VI ELEV. 2879 ft.

TWR 123.5

HAL, INDIA
HAL BENAGLURU AIRPORT


APRON-I					
STAND NO.	WGS CO-ORDINATES FOR AIRCRAFT STANDS		SUITABILITY	PCN	ELEV. ft
1A	12° 57' 13.167" N	077° 39' 51.268" E	UP TO 18m - WING SPAN	65/R/B/W/U	2914
1B	12° 57' 13.132" N	077° 39' 50.848" E	UP TO 18m - WING SPAN	65/R/B/W/U	2913
2A	12° 57' 12.394" N	077° 39' 51.359" E	UP TO 18m - WING SPAN	65/R/B/W/U	2914
2B	12° 57' 12.359" N	077° 39' 50.932" E	UP TO 18m - WING SPAN	65/R/B/W/U	2914
3A	12° 57' 11.627" N	077° 39' 51.449" E	UP TO 18m - WING SPAN	65/R/B/W/U	2915
3B	12° 57' 11.590" N	077° 39' 51.015" E	UP TO 18m - WING SPAN	65/R/B/W/U	2914
4A	12° 57' 10.842" N	077° 39' 51.540" E	UP TO 18m - WING SPAN	65/R/B/W/U	2916
4B	12° 57' 10.787" N	077° 39' 51.102" E	UP TO 18m - WING SPAN	65/R/B/W/U	2915
5A	12° 57' 10.048" N	077° 39' 51.635" E	UP TO 18m - WING SPAN	65/R/B/W/U	2917
5B	12° 57' 09.994" N	077° 39' 51.188" E	UP TO 18m - WING SPAN	65/R/B/W/U	2916
6A	12° 57' 13.005" N	077° 39' 49.783" E	UP TO 18m - WING SPAN	65/R/B/W/U	2914
6B	12° 57' 12.961" N	077° 39' 49.331" E	UP TO 18m - WING SPAN	65/R/B/W/U	2915
7A	12° 57' 12.312" N	077° 39' 49.843" E	UP TO 18m - WING SPAN	65/R/B/W/U	2915
7B	12° 57' 12.275" N	077° 39' 49.390" E	UP TO 18m - WING SPAN	65/R/B/W/U	2916
8A	12° 57' 11.446" N	077° 39' 49.917" E	UP TO 18m - WING SPAN	65/R/B/W/U	2913
8B	12° 57' 11.414" N	077° 39' 49.465" E	UP TO 18m - WING SPAN	65/R/B/W/U	2914
9A	12° 57' 10.623" N	077° 39' 49.989" E	UP TO 18m - WING SPAN	65/R/B/W/U	2914
9B	12° 57' 10.585" N	077° 39' 49.536" E	UP TO 18m - WING SPAN	65/R/B/W/U	2913
10A	12° 57' 09.871" N	077° 39' 50.054" E	UP TO 18m - WING SPAN	65/R/B/W/U	2914
10B	12° 57' 09.837" N	077° 39' 49.584" E	UP TO 18m - WING SPAN	65/R/B/W/U	2915
11A	12° 57' 12.200" N	077° 39' 47.706" E	UP TO 29m - WING SPAN	65/R/B/W/U	2909
11B	12° 57' 12.136" N	077° 39' 46.874" E	UP TO 29m - WING SPAN	65/R/B/W/U	2909
12A	12° 57' 11.069" N	077° 39' 47.838" E	UP TO 29m - WING SPAN	65/R/B/W/U	2910
12B	12° 57' 10.968" N	077° 39' 47.003" E	UP TO 29m - WING SPAN	65/R/B/W/U	2910
13A	12° 57' 09.961" N	077° 39' 47.967" E	UP TO 29m - WING SPAN	65/R/B/W/U	2912
13B	12° 57' 09.862" N	077° 39' 47.129" E	UP TO 29m - WING SPAN	65/R/B/W/U	2911
14	12° 57' 12.373" N	077° 39' 45.374" E	UP TO 32m - WING SPAN	65/R/B/W/U	2905
HELIPAD-1	12° 57' 11.907" N	077° 39' 41.008" E	UP TO 18m -ROTOR DIA.	65/R/B/W/U	2901
HELIPAD-2	12° 57' 10.938" N	077° 39' 41.123" E	UP TO 18m -ROTOR DIA.	65/R/B/W/U	2902
HELIPAD-3	12° 57' 09.968" N	077° 39' 41.215" E	UP TO 18m -ROTOR DIA.	65/R/B/W/U	2903
HELIPAD-4	12° 57' 12.131" N	077° 39' 42.985" E	UP TO 18m -ROTOR DIA.	65/R/B/W/U	2903
HELIPAD-5	12° 57' 11.165" N	077° 39' 43.102" E	UP TO 18m -ROTOR DIA.	65/R/B/W/U	2905

APRON-II					
STAND NO.	WGS CO-ORDINATES FOR AIRCRAFT STANDS		SUITABILITY	PCN	ELEV. ft
1	12° 57' 13.810" N	077° 40' 2.339" E	UP TO 36m - WING SPAN	76/R/A/W/T	2941
2	12° 57' 12.343" N	077° 40' 2.271" E	UP TO 74m - WING SPAN	76/R/A/W/T	2941
3	12° 57' 10.865" N	077° 40' 2.215" E	UP TO 66m - WING SPAN	76/R/A/W/T	2941
4	12° 57' 12.874" N	077° 40' 5.749" E	-	76/R/A/W/T	2941

APRON-IV					
STAND NO.	WGS CO-ORDINATES FOR AIRCRAFT STANDS		SUITABILITY	PCN	ELEV. ft
1A	12° 57' 08.362" N	077° 40' 10.250" E	B-737	52/R/B/W/U	2935
1B	12° 57' 07.399" N	077° 40' 10.318" E	B-737	52/R/B/W/U	2935
2A	12° 57' 08.455" N	077° 40' 11.633" E	B-737	52/R/B/W/U	2935
2B	12° 57' 07.476" N	077° 40' 11.697" E	B-737	52/R/B/W/U	2934
3A	12° 57' 08.534" N	077° 40' 13.028" E	B-737	52/R/B/W/U	2934
3B	12° 57' 07.555" N	077° 40' 13.096" E	B-737	52/R/B/W/U	2933
4A	12° 57' 08.635" N	077° 40' 14.362" E	B-737	52/R/B/W/U	2932
4B	12° 57' 07.657" N	077° 40' 14.441" E	B-737	52/R/B/W/U	2932

* DATUM :
  HORIZONTAL : WGS-1984
  VERTICAL : EGM-08
*DIMENSION IN METRES.
*ELEVATION IN FEET.

N(TRUE)
N(MAG.)
M.VAR. 1°45'W(2010)
ANNUAL RATE OF CHANGE 2'E

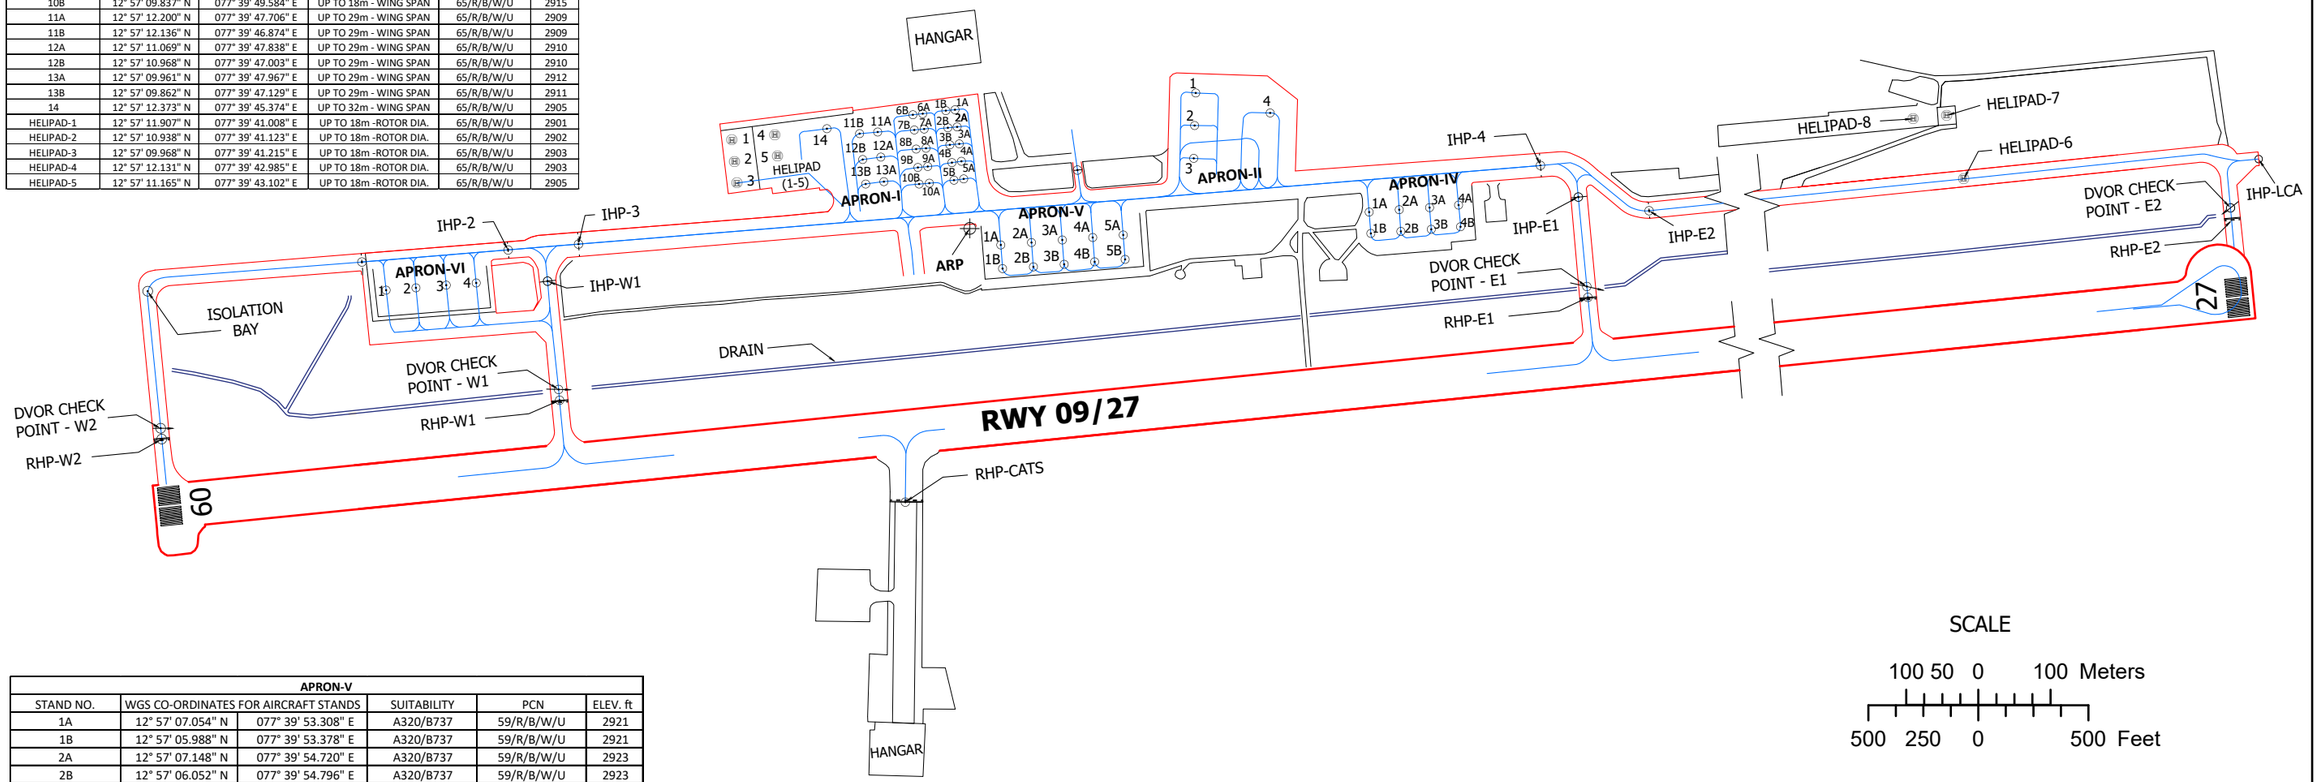

SCALE
100 50 0 100 Meters
500 250 0 500 Feet

APRON-V					
STAND NO.	WGS CO-ORDINATES FOR AIRCRAFT STANDS		SUITABILITY	PCN	ELEV. ft
1A	12° 57' 07.054" N	077° 39' 53.308" E	A320/B737	59/R/B/W/U	2921
1B	12° 57' 05.988" N	077° 39' 53.378" E	A320/B737	59/R/B/W/U	2921
2A	12° 57' 07.148" N	077° 39' 54.720" E	A320/B737	59/R/B/W/U	2923
2B	12° 57' 06.052" N	077° 39' 54.796" E	A320/B737	59/R/B/W/U	2923
3A	12° 57' 07.249" N	077° 39' 56.137" E	A320/B737	59/R/B/W/U	2925
3B	12° 57' 06.152" N	077° 39' 56.210" E	A320/B737	59/R/B/W/U	2924
4A	12° 57' 07.347" N	077° 39' 57.536" E	A320/B737	59/R/B/W/U	2926
4B	12° 57' 06.250" N	077° 39' 57.613" E	A320/B737	59/R/B/W/U	2926
5A	12° 57' 07.446" N	077° 39' 58.939" E	A320/B737	59/R/B/W/U	2929
5B	12° 57' 06.345" N	077° 39' 59.014" E	A320/B737	59/R/B/W/U	2927

APRON-VI					
STAND NO.	WGS CO-ORDINATES FOR AIRCRAFT STANDS		SUITABILITY	PCN	ELEV. ft
1	12° 57' 05.305" N	077° 39' 25.043" E	A320/B737	52/R/B/W/U	2877
2	12° 57' 05.396" N	077° 39' 26.414" E	A320/B737	52/R/B/W/U	2877
3	12° 57' 05.503" N	077° 39' 27.808" E	A320/B737	52/R/B/W/U	2878
4	12° 57' 05.588" N	077° 39' 29.187" E	A320/B737	52/R/B/W/U	2879

ISOLATION BAY			
STAND NO.	WGS CO-ORDINATES FOR AIRCRAFT STANDS		ELEV. ft
ISOLATION BAY	12° 57' 05.370" N	077° 39' 14.087" E	2879

HELIPADS				
STAND NO.	WGS CO-ORDINATES FOR AIRCRAFT STANDS		SUITABILITY	ELEV. ft
HELIPAD-6	12° 57' 10.691" N	077° 40' 50.307" E	UP TO 22m -ROTOR DIA.	2907
HELIPAD-7	12° 57' 13.552" N	077° 40' 49.554" E	UP TO 22m -ROTOR DIA.	2920
HELIPAD-8	12° 57' 13.422" N	077° 40' 48.018" E	UP TO 22m -ROTOR DIA.	2920

LEGEND	
DVOR CHECK POINT	
TAXI -HOLDING POINT	
AIRCRAFT STAND	

DATE OF AERONAUTICAL INFORMATION
FEBURARY, 2026

AIRPORTS AUTHORITY OF INDIA

DRG NO .: AAI-09/PDC/2026 (CARTO)