AERODROME ELEVATION : 1857 ft.

AERODROME OBSTACLE CHART
TYPE - B

DEHRADUN, INDIA

DEHRADUN AIRPORT

DISTANCE IN METRE
ELEVATION IN FEET (EGM-08)
GRID LINES AND CO-ORDINATES
SHOWN ARE BASED ON WGS-84 DATUM

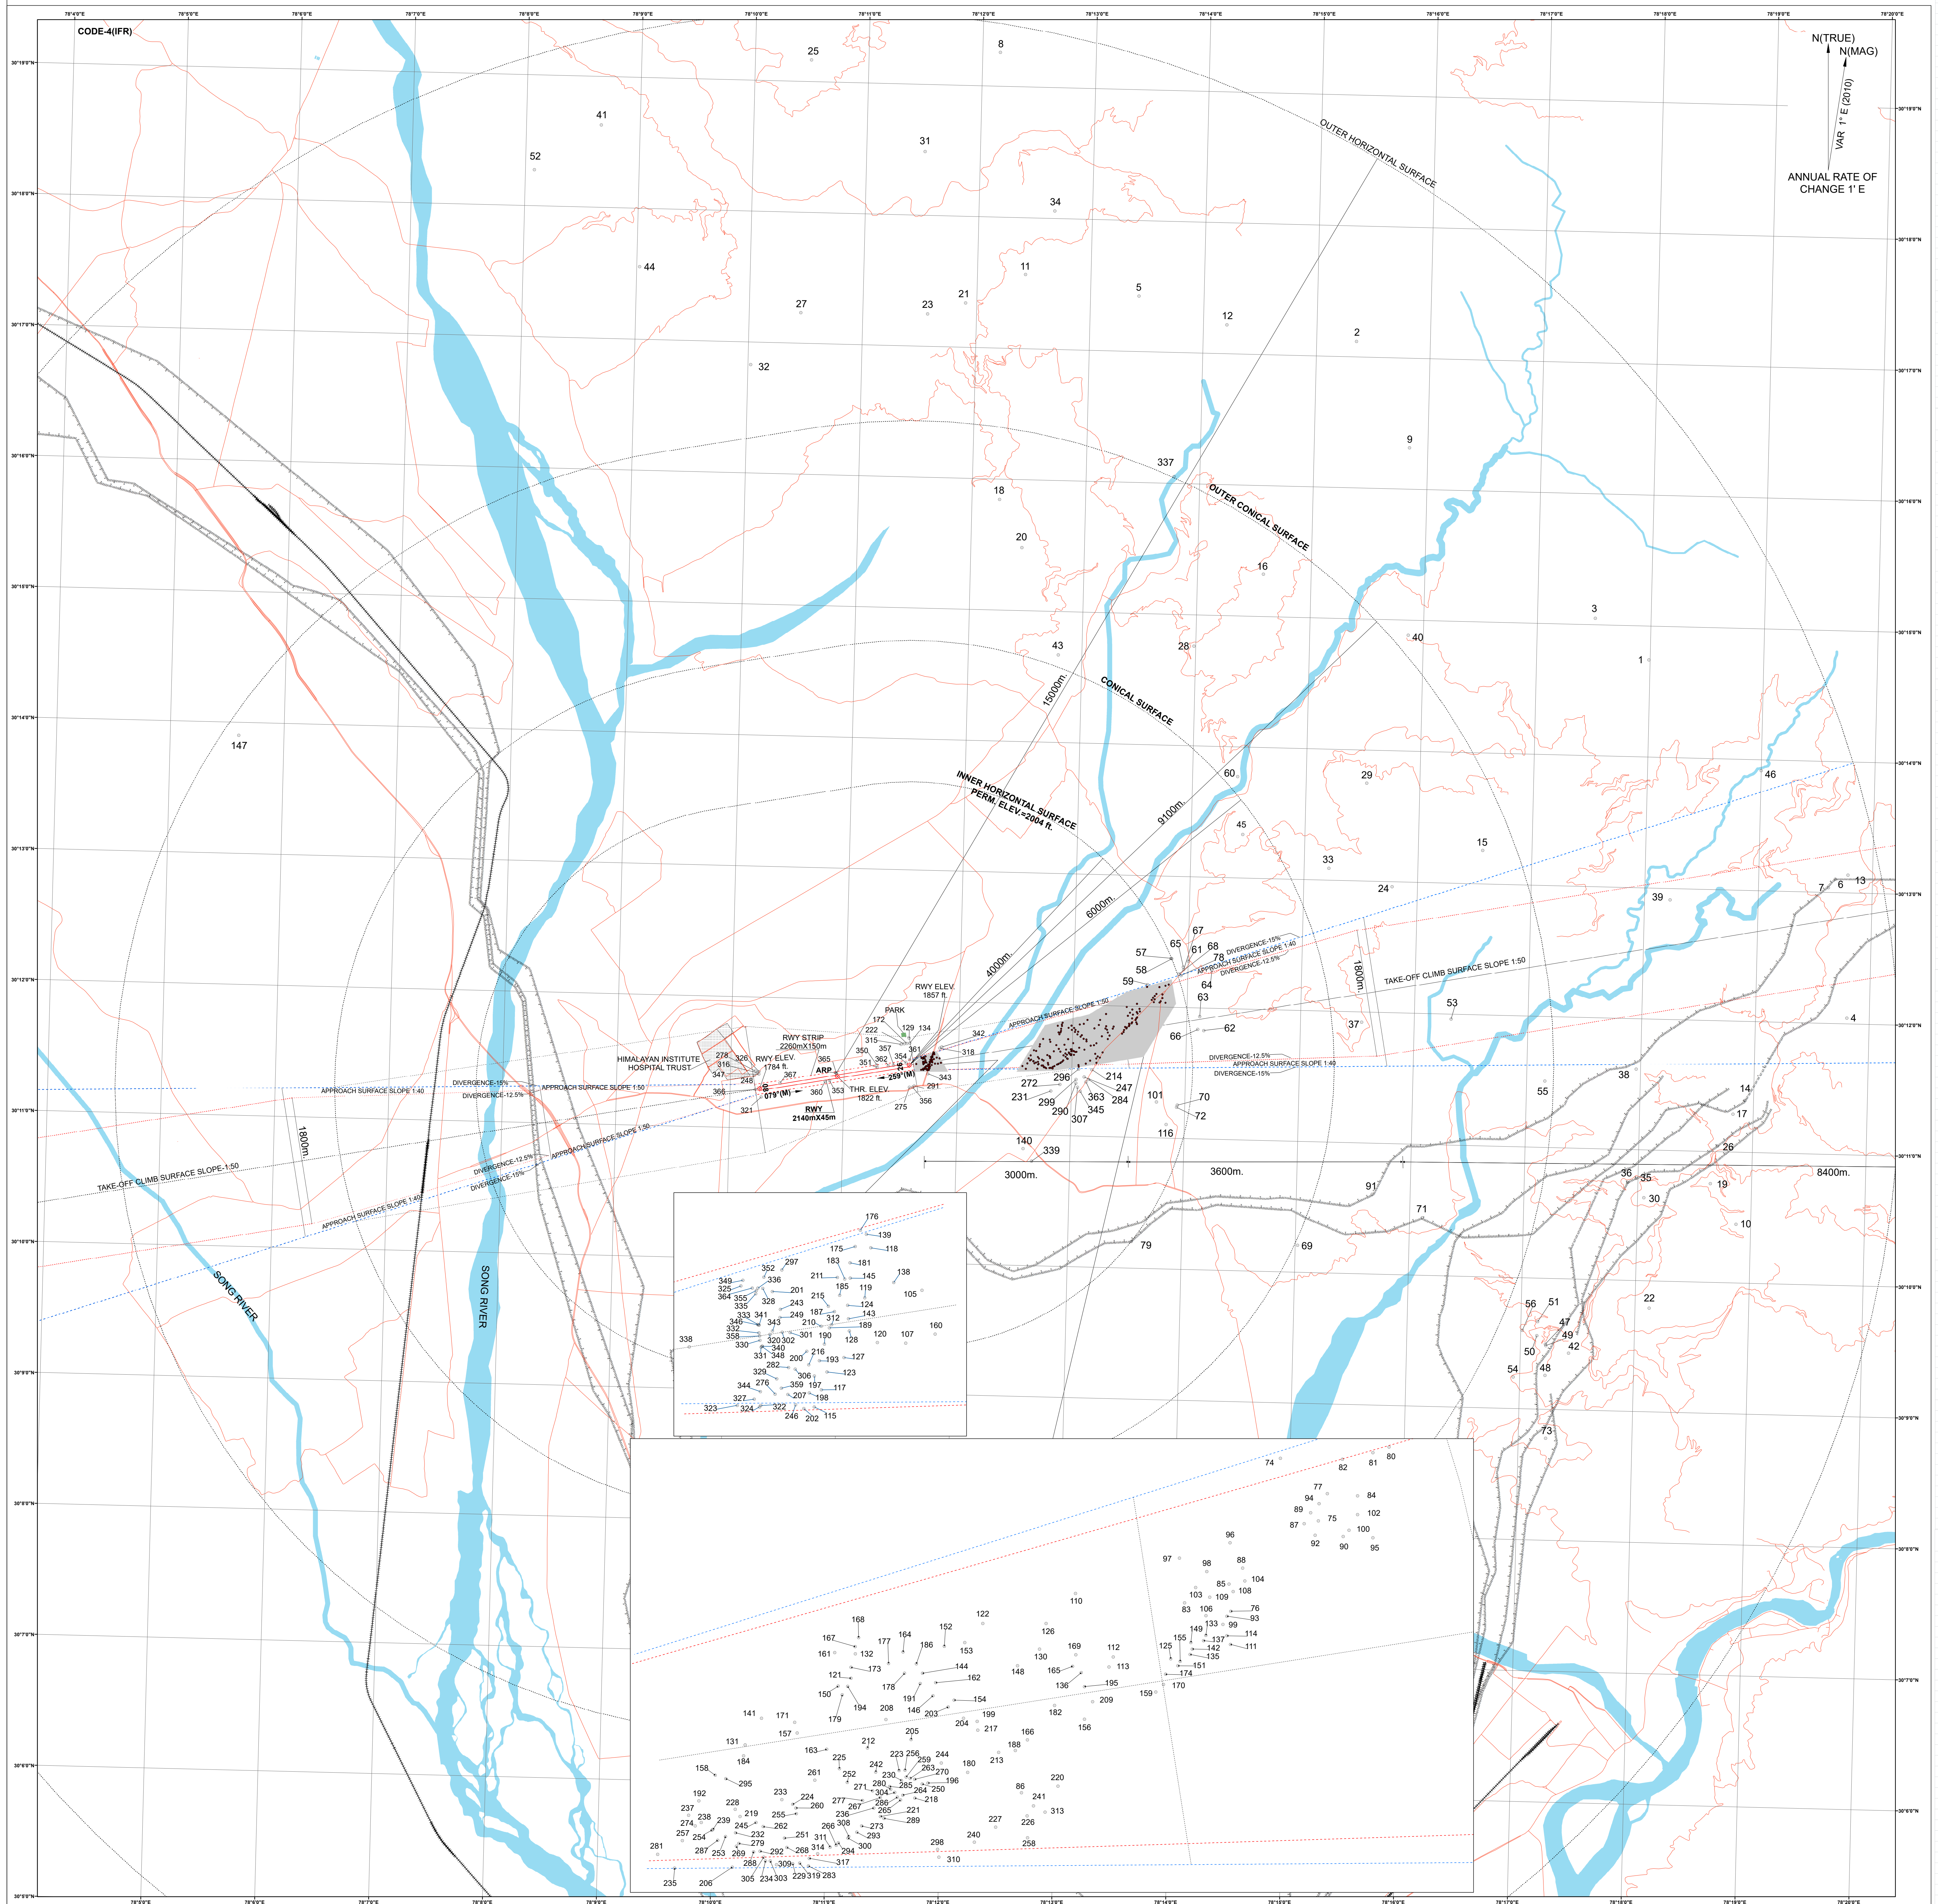

LEGEND	
AERODROME REFRENCE POINT 30° 11' 26.27"N 078° 10' 56.00"E	⌖
ELECTRICAL LINE	ᨓᨓᨓ
ROAD	—
RAILWAY TRACK	++++++
BUILDUP AREA	▨
WATER BODY	🟦
PARK	🟩

ORDER OF ACCURACY	
TAKE-OFF AND APPROACH AREAS	
HORIZONTAL	REMARK
5 M	AT POINT OF ORIGIN INCREASING AT A RATE OF 1 PER 500
VERTICAL	REMARK
0.5 M	IN THE FIRST 300M AND INCREASING AT A RATE OF 1 PER 1000
OTHER AREAS	
HORIZONTAL	REMARK
5 M	WITHIN 5000M OF THE ARP AND 12M BEYOND THAT AREA
VERTICAL	REMARK
1 M	WITHIN 1500M OF THE ARP INCREASING AT A RATE OF 1 PER 1000

SCALE 1:20,000

METRES 0 1000 2000 3000 4000 5000 6000

FEETS 2,500 0 2,500 5,000 7,500 10,000 12,500 15,000 17,500 20,000

NOTE:-
1. OBSTACLE SHOWN ARE THOSE WHICH PENETRATE THE SURFACE SPECIFIED IN ANNEX 14, VOL-1, CHAPTER-4 GSR.
2. TORA FOR RWY-08 IS 2140 M.
TORA FOR RWY-26 IS 2140 M.
3. ALL OBSTACLES ARE SHOWN IN THE CHART BASED ON AERONAUTICAL SURVEY MAY 2023.
4. TOPOGRAPHIC FEATURES SOURCE-WORLD TOPO MAP, ESRI & GOOGLE EARTH

AMENDMENT RECORD		
NO	DATE	ENTERED BY

SR.NO	UUID	OBJECT	LATITUDE	LONGITUDE	TOP ELEV. IN FEET	PERM. ELEV. IN FEET	OBSTACLE IN FEET	DIST. FROM ARP IN(M)
1	VIDN_9023	Tree on Hill	30° 14' 44.644" N	078° 17' 59.509" E	6590.8	2840.8	3750.0	12874
2	VIDN_9015	Tree on Hill	30° 17' 07.338" N	078° 15' 21.105" E	6474.0	2840.8	3633.1	12677
3	VIDN_9022	Tree on Hill	30° 15' 03.086" N	078° 17' 30.664" E	6144.9	2840.8	3304.1	12494
4	VIDN_9030	Tree on Hill	30° 12' 02.747" N	078° 19' 48.337" E	5573.7	2348.7	3225.0	14290
5	VIDN_9011	Tree on Hill	30° 17' 25.699" N	078° 13' 25.717" E	5695.1	2840.8	2854.2	11775
6	VIDN_7454	H.T Tower on Hill	30° 13' 06.109" N	078° 19' 40.626" E	5519.3	2727.0	2792.3	14371
7	VIDN_7455	H.T Tower on Hill	30° 13' 02.341" N	078° 19' 37.019" E	5510.4	2719.4	2791.0	14253
8	VIDN_9090	Tree on Hill	30° 19' 15.723" N	078° 12' 09.333" E	5537.1	2840.8	2696.3	14596
9	VIDN_9016	Tree on Hill	30° 16' 19.198" N	078° 15' 50.385" E	5503.8	2840.8	2662.9	11978
10	VIDN_9033	Tree on Hill	30° 10' 27.051" N	078° 18' 52.476" E	5454.5	2840.8	2613.7	12883
11	VIDN_9010	Tree on Hill	30° 17' 34.393" N	078° 12' 25.544" E	5449.5	2840.8	2608.6	11592
12	VIDN_9014	Tree on Hill	30° 17' 13.438" N	078° 14' 12.496" E	5443.8	2840.8	2602.9	11917
13	VIDN_7453	H.T Tower on Hill	30° 13' 08.240" N	078° 19' 47.196" E	5264.3	2739.2	2525.2	14557
14	VIDN_7418	H.T Tower on Hill	30° 11' 23.942" N	078° 18' 55.751" E	5331.5	2840.8	2490.7	12840
15	VIDN_9026	Tree on Hill	30° 13' 15.616" N	078° 16' 34.205" E	5152.1	2727.8	2424.2	9657
16	VIDN_9017	Tree on Hill	30° 15' 19.685" N	078° 14' 34.913" E	4669.1	2325.3	2343.8	9274
17	VIDN_9031	Tree on Hill	30° 11' 17.427" N	078° 18' 49.513" E	5157.1	2840.8	2316.3	12676
18	VIDN_9012	Tree on Hill	30° 15' 50.954" N	078° 12' 14.676" E	3967.4	1748.4	2219.0	8422
19	VIDN_9032	Tree on Hill	30° 10' 45.298" N	078° 18' 38.429" E	5029.7	2840.8	2188.8	12441
20	VIDN_9013	Tree on Hill	30° 15' 29.111" N	078° 12' 27.115" E	3903.1	1782.3	2120.8	7869
21	VIDN_9009	Tree on Hill	30° 17' 20.590" N	078° 11' 54.212" E	4948.1	2840.8	2107.3	11027
22	VIDN_9034	Tree on Hill	30° 09' 47.706" N	078° 18' 07.750" E	4867.4	2840.8	2026.6	11949
23	VIDN_9008	Tree on Hill	30° 17' 15.215" N	078° 11' 34.330" E	4845.0	2840.8	2004.2	10799
24	VIDN_9049	Tree on Hill	30° 12' 57.967" N	078° 15' 46.831" E	4490.7	2507.3	1983.4	8279
25	VIDN_9092	Tree on Hill	30° 19' 10.168" N	078° 10' 29.676" E	4748.8	2840.8	1908.0	14310
26	VIDN_7419	H.T Tower on Hill	30° 11' 02.728" N	078° 18' 41.686" E	4730.7	2840.8	1889.8	12484
27	VIDN_9005	Tree on Hill	30° 17' 14.240" N	078° 10' 27.399" E	4644.0	2840.8	1803.2	10748
28	VIDN_9037	Tree on Hill	30° 14' 45.972" N	078° 13' 59.174" E	3924.2	2140.4	1783.8	7866
29	VIDN_9025	Tree on Hill	30° 13' 45.025" N	078° 15' 32.135" E	4197.3	2486.5	1710.9	8536
30	VIDN_5320	Temple on Hill	30° 10' 38.208" N	078° 18' 03.480" E	4499.0	2840.8	1658.2	11537
31	VIDN_9091	Tree on Hill	30° 18' 29.512" N	078° 11' 30.828" E	4434.7	2840.8	1593.8	13073
32	VIDN_9004	Tree on Hill	30° 16' 49.916" N	078° 10' 01.526" E	4402.9	2840.8	1562.1	10077
33	VIDN_9027	Tree on Hill	30° 13' 05.706" N	078° 15' 13.212" E	3907.0	2369.1	1537.9	7534
34	VIDN_9089	Tree on Hill	30° 18' 03.740" N	078° 12' 40.144" E	4341.4	2840.8	1500.6	12558
35	VIDN_7450	H.T Tower	30° 10' 46.965" N	078° 17' 59.332" E	4323.8	2840.8	1482.9	11395
36	VIDN_7449	H.T Tower	30° 10' 45.047" N	078° 17' 54.815" E	4303.1	2840.8	1462.3	11281
37	VIDN_9029	Tree on Hill	30° 11' 55.543" N	078° 15' 32.475" E	3627.2	2272.9	1354.3	7454
38	VIDN_9079	Tree on Hill	30° 11' 37.126" N	078° 17' 57.876" E	4022.8	2840.8	1181.9	11295
39	VIDN_9078	Tree on Hill	30° 12' 54.954" N	078° 18' 13.642" E	3520.1	2348.7	1171.4	12025
40	VIDN_9024	Tree on Hill	30° 14' 53.289" N	078° 15' 52.165" E	3963.6	2840.8	1122.8	10172
41	VIDN_9071	Tree on Hill	30° 18' 38.057" N	078° 08' 39.541" E	3949.3	2840.8	1108.5	13795
42	VIDN_9068	Tree on Hill	30° 09' 26.208" N	078° 17' 25.734" E	3821.9	2840.8	981.1	11068
43	VIDN_9018	Tree on Hill	30° 14' 40.476" N	078° 12' 47.750" E	2783.9	1827.2	956.8	6689
44	VIDN_9070	Tree on Hill	30° 17' 33.475" N	078° 09' 01.618" E	3744.1	2840.8	903.2	11720
45	VIDN_9038	Tree on Hill	30° 13' 20.150" N	078° 14' 27.391" E	3158.9	2287.2	871.7	6656
46	VIDN_9077	Tree on Hill	30° 13' 55.185" N	078° 19' 00.080" E	3640.0	2840.8	799.2	13741
47	VIDN_7064	Cellphone Mast	30° 09' 30° 116" N	078° 17' 13.417" E	3619.0	2840.8	778.1	10717
48	VIDN_9069	Tree on Hill	30° 09' 15.707" N	078° 17' 13.601" E	3614.2	2840.8	773.4	10878
49	VIDN_7063	Cellphone Mast	30° 09' 29.404" N	078° 17' 13.695" E	3610.5	2840.8	769.6	10732
50	VIDN_9072	Tree on Hill	30° 09' 33.849" N	078° 17' 08.842" E	3473.7	2840.8	632.8	10564
51	VIDN_7069	Cellphone Mast on Hill	30° 09' 40.257" N	078° 17' 09.110" E	3427.0	2840.8	586.1	10507
52	VIDN_9035	Tree on Hill	30° 18' 16.775" N	078° 08' 04.814" E	3411.3	2840.8	570.4	13451
53	VIDN_9083	Tree on Hill	30° 11' 57.998" N	078° 16' 19.589" E	2917.0	2355.1	561.8	8715
54	VIDN_7062	Cellphone Mast	30° 09' 14.583" N	078° 16' 56.863" E	3363.3	2840.8	522.5	10477
55	VIDN_9082	Tree on Hill	30° 11' 30° 645" N	078° 17' 09.871" E	3276.4	2786.8	489.6	10007
56	VIDN_9073	Tree on Hill	30° 09' 36.140" N	078° 17' 01.096" E	3310.5	2840.8	469.7	10345
57	VIDN_7023	Cellphone Mast	30° 12' 22.692" N	078° 13' 51.104" E	2399.8	2004.2	395.6	4998
58	VIDN_7024	Cellphone Mast	30° 12' 22.466" N	078° 13' 51.502" E	2392.8	2004.2	388.6	5006
59	VIDN_6346	Tree	30° 12' 10.422" N	078° 13' 39.086" E	2340.2	2004.2	336.0	4571
60	VIDN_9215	HILL TOP	30° 13' 46.607" N	078° 14' 23.885" E	2510.5	2193.2	317.2	7045
61	VIDN_7068	Cellphone Mast	30° 12' 21.641" N	078° 14' 00.352" E	2347.5	2038.3	309.2	5220
62	VIDN_5323	Building, Sintex Tank Top - 740.22 m	30° 11' 49.986" N	078° 14' 09.325" E	2428.5	2127.2	301.3	5225
63	VIDN_9076	Tree on Hill	30° 11' 56.233" N	078° 14' 06.967" E	2424.5	2125.4	299.1	5193
64	VIDN_5321	Building (U/C), Shed Top - 750.40 m	30° 12' 17.696" N	078° 14' 12.776" E	2461.9	2165.7	296.2	5499
65	VIDN_5287	Temple Top	30° 12' 18.749" N	078° 13' 57.708" E	2308.7	2022.1	286.5	5124
66	VIDN_5322	Building, Staircase Room Top - 728.34 m	30° 11' 50.349" N	078° 14' 06.076" E	2389.5	2121.7	267.8	5141
67	VIDN_5294	Building Top	30° 12' 17.642" N	078° 13' 57.888" E	2284.3	2020.9	263.4	5118
68	VIDN_5292	Building(U/C) Top	30° 12' 15.560" N	078° 13' 55.521" E	2270.9	2007.5	263.4	5038
69	VIDN_9048	Tree on Hill	30° 10' 12.668" N	078° 15' 01.471" E	2577.1	2339.1	238.0	6950
70	VIDN_5314	Temple on Hill	30° 11' 15.436" N	078° 13' 56.312" E	2237.9	2004.2	233.6	4837
71	VIDN_7445	H.T Tower on Hill	30° 10' 26.601" N	078° 16' 06.907" E	2679.1	2456.9	222.2	8522
72	VIDN_9041	Tree on Hill	30° 11' 14.468" N	078° 13' 55.926" E	2215.8	2004.2	211.5	4829
73	VIDN_9039	Tree on Hill	30° 08' 46.929" N	078° 17' 14.700" E	3036.7	2840.8	195.8	11263
74	VIDN_6347	Group of Trees	30° 12' 09.30° " N	078° 13' 38.805" E	2272.5	2088.5	184.0	4554
75	VIDN_6342	Group of Trees	30° 12' 03.649" N	078° 13' 42.972" E	2263.8	2086.6	177.2	4614
76	VIDN_6311	Group of Trees	30° 11' 55.164" N	078° 13' 33.965" E	2230.3	2068.0	162.3	4320
77	VIDN_6345	Tree	30° 12' 06.145" N	078° 13' 43.853" E	2248.4	2089.1	159.4	4657
78	VIDN_5288	Building, Staircase Room Top - 694.99 m	30° 12' 14.977" N	078° 13' 56.592" E	2280.1	2129.5	150.6	5060
79	VIDN_7441	H.T Tower	30° 10' 12.526" N	078° 13' 33.689" E	1932.6	1782.2	150.4	4793
80	VIDN_5290	Building, Staircase Room Top - 685.84 m	30° 12' 10.567" N	078° 13' 50.243" E	2250.1	2101.7	148.4	4859
81	VIDN_5291	BUILDING	30° 12' 09.995" N	078° 13' 48.549" E	2244.1	2098.6	145.5	4810
82	VIDN_5276	Temple Shed Top	30° 12' 09.331" N	078° 13' 45.354" E	2235.8	2092.8	142.9	4722
83	VIDN_5404	Overhead Water Tank	30° 11' 55.814" N	078° 13' 29.078" E	2199.1	2059.8	139.3	4197
84	VIDN_5275	Building, Staircase Room Top - 680.70 m.	30° 12' 06.008" N	078° 13' 47.041" E	2233.2	2094.5	138.7	4738
85	VIDN_7364	Communication Antenna	30° 11' 57.642" N	078° 13' 33.708" E	2207.0	2068.5	138.5	4330
86	VIDN_7030	CELLPHONE MAST	30° 11' 38.068" N	078° 13' 12.365" E	2161.7	2024.5	137.2	3668
87	VIDN_5282	Building, Sintex Tank Top - 675.63 m.	30° 12' 03.339" N	078° 13' 41.481" E	2216.6	2084.0	132.6	4573
88	VIDN_6314	Group of Trees	30° 11' 59.149" N	078° 13' 35.109" E	2201.5	2071.4	130.1	4377
89	VIDN_5280	Building, Staircase Room Top - 674.45 m.	30° 12' 04.361" N	078° 13' 42.140" E	2212.7	2085.5	127.3	4598
90	VIDN_5286	Building, Iron Rod Top - 675.97 m.	30° 12' 02.259" N	078° 13' 45.626" E	2217.7	2090.7	127.0	4673
91	VIDN_7446	H.T Tower on Hill	30° 10' 36.818" N	078° 15' 40.201" E	2475.5	2350.8	124.8	7758
92	VIDN_5284	Building, Staircase Room Top - 673.71 m.	30° 12' 02.321" N	078° 13' 42.662" E	2210.3	2085.6	124.7	4596
93	VIDN_6310	Group of Trees	30° 11' 54.705" N	078° 13' 33.574" E	2190.9	2067.2	123.7	4307
94	VIDN_5278	Building, Staircase Room Top - 673.78 m.	30° 12' 05.233" N	078° 13' 42.997" E	2210.5	2087.3	123.3	4627
95	VIDN_5271	Building, Sintex Tank Top - 676.41 m.	30° 12' 02.211" N	078° 13' 48.770" E	2219.2	2096.1	123.0	4754
96	VIDN_5242	Building, Staircase Room Top - 668.04 m.	30° 12' 01.448" N	078° 13' 33.714" E	2191.7	2069.9	121.9	4358
97	VIDN_6318	Group of Trees	30° 11' 59.908" N	078° 13' 28.421" E	2176.9	2060.2	116.8	4209
98	VIDN_6316	Group of Trees	30° 11' 58.763" N	078° 13' 31.331" E	2181.4	2064.8	116.6	4276
99	VIDN_6336	Group of Trees	30° 11' 53.922" N	078° 13' 33.182" E	2181.4	2066.2	115.2	4292
100	VIDN_8011	Mobile Road Traffic	30° 12' 02.858" N	078° 13' 46.238" E	2206.7	2092.0	114.7	4693
101	VIDN_7033	Cellphone Mast	30° 11' 16.677" N	078° 13' 45.231" E	2118.8	2004.2	114.6	4539
102	VIDN_5273	Building Top	30° 12' 04.30° " N	078° 13' 47.096" E	2208.5	2094.0	114.4	4726
103	VIDN_6308	Group of Trees	30° 11' 57.245" N	078° 13' 30.203" E	2168.8	2062.3	106.5	4236
104	VIDN_5244	Building, Staircase Room Top - 663.64 m.	30° 11' 57.971" N	078° 13' 35.368" E	2177.3	2071.4	105.8	4375
105	VIDN_6172	Group of Trees	30° 11' 34.221" N	078° 11' 50.303" E	1985.9	1881.3	104.5	1474
106	VIDN_6319	Group of Trees	30° 11' 54.702" N	078° 13' 31.360" E	2162.9	2063.3	99.6	4249
107	VIDN_6166	Group of Trees	30° 11' 31.777" N	078° 11' 49.513" E	1976.9	1879.1	97.9	1442
108	VIDN_5247	Building, Sintex Tank Top - 659.94 m.	30° 11' 56.967" N	078° 13' 34.176" E	2165.1	2069.0	96.1	4337
109	VIDN_5246	Building, Staircase Room Top - 658.26 m.	30° 11' 56.409" N	078° 13' 31.710" E	2159.6	2064.6	95.1	4269
110	VIDN_6302	Group of Trees	30° 11' 56.429" N	078° 13' 17.537" E	2133.6	2040.1	93.5	3900
111	VIDN_6338	Group of Trees	30° 11' 52.133" N	078° 13' 34.016" E	2160.3	2067.0	93.3	4303
112	VIDN_6300	Group of Trees	30° 11' 50.728" N	078° 13' 21.690" E	2138.2	2045.2	93.0	3971
113	VIDN_6299	Group of Trees	30° 11' 49.779" N	078° 13' 21.259" E	2135.2	2044.1	91.1	3954
114	VIDN_6337	Group of Trees	30° 11' 52.900" N	078° 13' 33.620" E	2156.6	2066.6	90.0	4297
115	VIDN_6188	Group of Trees	30° 11' 28.750" N	078° 11' 44.778" E	1959.5	1869.8	89.7	1308
116	VIDN_7034	Cellphone Mast	30° 11' 06.523" N	078° 13' 50.682" E	2093.6	2004.2	89.4	4715
117	VIDN_6187	Group of Trees	30° 11' 29.543" N	078° 11' 45.128" E	1959.7	1870.7	89.0	1319
118	VIDN_6185	Group of Trees	30° 11' 36.105" N	078° 11' 47.547" E	1963.5	1877.3	86.2	1412
119	VIDN_6164	Group of Trees	30° 11' 33.805" N	078° 11' 47.296" E	1961.8	1876.0	85.8	1392
120	VIDN_6167	Group of Trees	30° 11' 31.769" N	078° 11' 48.018" E	1961.7	1876.5	85.3	1402
121	VIDN_6294	Tree	30° 11' 48.175" N	078° 12' 54.074" E	2080.3	1996.6	83.8	3231
122	VIDN_6305	Group of Trees	30° 11' 53.484" N	078° 13' 07.833" E	2105.5	2022.3	83.3	3626
123	VIDN_6170	Group of Trees	30° 11' 30° 366" N	078° 11' 45.401" E	1952.9	1871.5	81.5	1328
124	VIDN_6163	Group of Trees	30° 11' 33.443" N	078° 11' 46.405" E	1955.7	1874.3	81.4	1367
125	VIDN_5262	Building, Sintex Tank Top - 650.87 m.	30° 11' 50.675" N	078° 13' 27.756" E	2135.4	2055.7	79.7	4130
126	VIDN_6303	Group of Trees	30° 11' 53.626" N	078° 13' 14.518" E	2113.5	2033.9	79.7	3802
127	VIDN_6169	Group of Trees	30° 11' 31.046" N	078° 11' 46.280" E	1952.4	1873.2	79.2	1354
128	VIDN_6168	Group of Trees	30° 11' 32.271" N	078° 11' 46.524" E	1951.1	1874.1	77.0	1365
129	VIDN_5360	Terminal, Antenna Top - 590.06 m.	30° 11' 43.219" N	078° 11' 33.910" E	1935.9	1858.9	76.9	1141
130	VIDN_6304	Group of Trees	30° 11' 51.278" N	078° 13' 13.884" E	2108.6	2031.9	76.7	3770
131	VIDN_6278	Tree	30° 11' 41.837" N	078° 12' 43.077" E	2049.8	1975.3	74.5	2905
132	VIDN_5226	Building, Staircase Room Top - 631.36 m.	30° 11' 50.409" N	078° 12' 54.471" E	2071.3	1998.1	73.3	3257
133	VIDN_7205	Electric Pole	30° 11' 52.886" N	078° 13' 31.397" E	2135.0	2062.7	72.3	4239
134	VIDN_7307	Flood Light	30° 11' 40.932" N	078° 11' 34.361" E	1931.4	1859.3	72.1	1122
135	VIDN_5267	Building, Staircase Room Top - 649.23 m.	30° 11' 51.121" N	078° 13' 29.792" E	2130.0	2059.3	70.7	4186
136	VIDN_6301	Group of Trees	30° 11' 49.199" N	078° 13' 18.352" E	2109.1	2038.9	70.2	3875
137	VIDN_5269	Building, Sintex Tank Top - 649.90 m.	30° 11' 52.415" N	078° 13' 31.175" E	2132.2	2062.2	70.0	4230
138	VIDN_6173	Group of Trees	30° 11' 34.541" N	078° 11' 48.801" E	1948.6	1878.9	69.7	1436
139	VIDN_6186	Group of Trees	30° 11' 36.720" N	078° 11' 47.302" E	1946.4	1877.1	69.4	1410
140	VIDN_7025	Cellphone Mast	30° 10' 53.904" N	078° 12' 35.543" E	2073.5	2004.2	69.3	2845
141	VIDN_6277	Tree	30° 11' 44.315" N	078° 12' 44.747" E	2047.8	1979.0	68.8	2963
142	VIDN_7203	Electric Pole	30° 11' 51.619" N	078° 13' 30.005" E	2126.8	2059.9	66.9	4195
143	VIDN_6165	Group of Trees	30° 11' 32.828" N	078° 11' 46.467" E	1940.5	1874.2	66.3	1366
144	VIDN_6292	Group of Trees	30° 11' 48.788" N	078° 13' 01.600" E	2075.4	2009.8	65.7	3432
145	VIDN_6162	Group of Trees	30° 11' 34.689" N	078° 11' 46.505" E	1939.6	1874.9	64.7	1376
146	VIDN_6291	Group of Trees	30° 11' 46.748" N	078° 13' 02.761" E	2075.4	2011.0	64.3	3451
147	VIDN_9059	Tree on Hill	30° 13' 54.162" N	078° 05' 36.340" E	2466.7	2402.5	64.3	9692
148	VIDN_6306	Group of Trees	30° 11' 49.683" N	078° 13' 11.622" E	2091.5	2027.4	64.1	3700
149	VIDN_5270	Building Top	30° 11' 52.212" N	078° 13' 29.841" E	2123.6	2059.8	63.8	4194
150	VIDN_5209	BUILDING	30° 11' 47.412" N	078° 12' 52.739" E	2057.4	1994.0	63.4	3191
151	VIDN_5265	Building Top	30° 11' 50.050" N	078° 13' 28.534" E	2119.9	2056.8	63.2	4147
152	VIDN_5240	Building, Shed Top - 633.25 m.	30° 11' 51.314" N	078° 13' 03.836" E	2077.6	2014.6	63.0	3507
153	VIDN_6307	Group of Trees	30° 11' 51.686" N	078° 13' 05.995" E	2081.4	2018.4	62.9	3566
154	VIDN_6290	Group of Trees	30° 11' 46.399" N	078° 13' 05.018" E	2077.7	2014.8	62.9	3508
155	VIDN_7202	Electric Pole	30° 11' 50.458" N	078° 13' 28.761" E	2119.7	2057.3	62.3	4156
156	VIDN_6298	Group of Trees	30° 11' 44.934" N	078° 13' 18.809" E	2100.4	2038.1	62.3	3865
157	VIDN_6275	Group of Trees	30° 11' 43.031" N	078° 12' 48.543" E	2047.2	1985.1	62.1	3056
158	VIDN_6279	Tree	30° 11' 38.977" N	078° 12' 40.002" E	2029.2	1968.9	60.3	2811
159	VIDN_5263	Building, Sintex Tank Top - 643.78 m.	30° 11' 47.599" N	078° 13' 26.272" E	2112.1	2052.0	60.2	4075
160	VIDN_6171	Group of Trees	30° 11' 32.221" N	078° 11' 51.059" E	1941.6	1881.9	59.7	1485
161	VIDN_5227	Building, Staircase Room Top - 626.04 m.	30° 11' 50.479" N	078° 12' 52.288" E	2053.9	1994.3	59.6	3200
162	VIDN_5221	Building, Staircase Room Top - 631.31 m.	30° 11' 47.958" N	078° 13' 03.023" E	2071.2	2011.9	59.3	3464
163	VIDN_6273	Group of Trees	30° 11' 41.599" N	078° 12' 51.695" E	2049.0	1990.1	59.0	3132
164	VIDN_5326	Building, Sintex Tank Top - 629.66 m.	30° 11' 50.690" N	078° 12' 59.500" E	2065.8	2006.8	58.9	3390
165	VIDN_5237	Building, Sintex Tank Top - 638.94 m.	30° 11' 49.770" N	078° 13' 17.419" E	2096.2	2037.5	58.8	3853
166	VIDN_6289	Group of Trees	30° 11' 42.929" N	078° 13' 12.844" E	2085.8	2027.1	58.8	3698
167	VIDN_7169	Electric Pole	30° 11' 51.080" N	078° 12' 54.435" E	2056.6	1998.2	58.4	3260
168	VIDN_7220	Electric Pole	30° 11' 51.912" N	078° 12' 54.767" E	2057.2	1999.1	58.1	3275
169	VIDN_5238	BUILDING	30° 11' 50.833" N	078° 13' 17.739" E	2096.1	2038.4	57.7	3868
170	VIDN_5264	Building, Staircase Room Top - 642.50 m.	30° 11' 48.311" N	078° 13' 27.058" E	2107.9	2053.6	54.3	4099
171	VIDN_5176	Building, Staircase Room Top - 621.41 m.	30° 11' 44.016" N	078° 12' 48.242" E	2038.7	1985.0	53.7	3053
172	VIDN_7306	Flood Light	30° 11' 40.697" N	078° 11' 32.832" E	1931.2	1878.8	52.4	1081
173	VIDN_7168	Electric Pole	30° 11' 49.173" N	078° 12' 54.051" E	2048.7	1996.9	51.9	3237
174	VIDN_8010	Mobile Road Traffic	30° 11' 49.238" N	078° 13' 27.246" E	2106.0	2054.2	51.8	4109
175	VIDN_7264	Light Pole	30° 11' 36.147" N	078° 11' 46.728" E	1927.6	1875.9	51.7	1391
176	VIDN_7263	Light Pole	30° 11' 36.897" N	078° 11' 46.975" E	1928.2	1876.6	51.7	1403
177	VIDN_7223	Electric Pole	30° 11' 49.613" N	078° 12' 57.996" E	2055.5	2003.9	51.6	3343
178	VIDN_7171	Electric Pole	30° 11' 48.743" N	078° 12' 59.705" E	2058.0	2006.5	51.5	3382
179	VIDN_5210	Building, Sintex Tank Top - 623.54 m.	30° 11' 46.639" N	078° 12' 53.196" E	2045.7	1994.5	51.2	3199
180	VIDN_6296	Group of Trees	30° 11' 39.805" N	078° 13' 06.623" E	2066.2	2015.2	51.0	3521
181	VIDN_7265	Light Pole	30° 11' 35.391" N	078° 11' 46.475" E	1925.9	1875.1	50.8	1380
182	VIDN_5233	Building Top	30° 11' 46.131" N	078° 13' 15.620" E	2083.3	2033.0	50.2	3786
183	VIDN_7266	Light Pole	30° 11' 34.644" N	078° 11' 46.219" E	1924.6	1874.4	50.2	1368
184	VIDN_5177	Building, Sintex Tank Top - 617.17 m..	30° 11' 40.833" N	078° 12' 42.937" E	2024.8	1974.7	50.2	2897
185	VIDN_7267	Light Pole	30° 11' 33.898" N	078° 11' 45.969" E	1923.7	1873.7	50.0	1358
186	VIDN_5224	Building Top	30° 11' 49.650" N	078° 13' 00.928" E	2058.5	2008.9	49.6	3420
187	VIDN_7268	Light Pole	30° 11' 33.137" N	078° 11' 45.713" E	1921.8	1873.0	48.8	1347
188	VIDN_6288	Group of Trees	30° 11' 41.917" N	078° 13' 11.587" E	2073.1	2024.5	48.6	3661
189	VIDN_7269	Light Pole	30° 11' 32.395" N	078° 11' 45.468" E	1920.8	1872.3	48.4	1337
190	VIDN_7270	Light Pole	30° 11' 31.642" N	078° 11' 45.226" E	1919.6	1871.6	48.0	1328
191	VIDN_7173	Electric Pole	30° 11' 47.829" N	078° 13' 01.389" E	2057.0	2009.1	47.9	3421
192	VIDN_6260	Group of Trees	30° 11' 36.605" N	078° 12' 38.334" E	2012.9	1965.2	47.7	2757
193	VIDN_7271	Light Pole	30° 11' 30°872"N	078° 11' 44.980" E	1918.1	1870.9	47.1	1318
194	VIDN_7166	Electric Pole	30° 11' 47.424" N	078° 12' 53.740" E	2042.8	1995.7	47.1	3218
195	VIDN_5236	Building, Sintex Tank Top - 635.80 m.	30° 11' 47.936" N	078° 13' 18.721" E	2085.9	2039.1	46.9	3877
196	VIDN_6286	Group of Trees	30° 11' 38.753" N	078° 13' 02.467" E	2054.4	2007.6	46.8	3406
197	VIDN_7229	Light Pole	30° 11' 30° 159" N	078° 11' 44.744" E	1916.8	1870.2	46.6	1310
198	VIDN_7230	Light Pole	30° 11' 29.383" N	078° 11' 44.492" E	1915.9	1869.5	46.4	1301
199	VIDN_5219	Building, Sintex Tank Top - 629.36 m.	30° 11' 44.493" N	078° 13' 07.494" E	2064.8	2018.4	46.4	3564
200	VIDN_6177	Group of Trees	30° 11' 31.293" N	078° 11' 44.305" E	1916.1	1869.9	46.2	1302
201	VIDN_6025	GROUP OF TREE	30° 11' 33.992" N	078° 11' 42.412" E	1913.4	1867.6	45.8	1265
202	VIDN_7231	Light Pole	30° 11' 28.659" N	078° 11' 44.231" E	1914.2	1868.8	45.4	1293
203	VIDN_7175	Electric Pole	30° 11' 45.754" N	078° 13' 04.400" E	2057.9	2013.5	44.4	3488
204	VIDN_7174	Electric Pole	30° 11' 44.769" N	078° 13' 06.045" E	2059.4	2016.0	43.4	3527
205	VIDN_5215	Building, Sintex Tank Top - 624.58 m.	30° 11' 42.697" N	078° 13' 00.573" E	2049.1	2005.8	43.3	3372
206	VIDN_6268	Group of Trees	30° 11' 30°599"N	078° 12' 42.036" E	2012.7	1969.4	43.3	2841
207	VIDN_6179	Group of Trees	30° 11' 29.296" N	078° 11' 43.368" E	1910.4	1867.6	42.8	1271
208	VIDN_5211	Building (U/C) Top	30° 11' 44.479" N	078° 12' 57.859" E	2044.4	2001.8	42.6	3309
209	VIDN_5235	Building, Sintex Tank Top - 634.75 m.	30° 11' 46.571" N	078° 13' 19.631" E	2082.5	2040.1	42.4	3894
210	VIDN_6176	Group of Trees	30° 11' 32.450" N	078° 11' 45.033" E	1913.3	1871.6	41.7	1326
211	VIDN_6174	Group of Trees	30° 11' 34.710" N	078° 11' 45.825" E	1915.4	1873.8	41.6	1358
212	VIDN_5212	Building, Shed Top - 621.51 m.	30° 11' 41.826" N	078° 12' 55.995" E	2039.1	1997.6	41.5	3247
213	VIDN_5217	TEMPLE	30° 11' 41.718" N	078° 13' 09.837" E	2060.7	2021.4	39.2	3613
214	VIDN_5303	Building, Sintex Tank Top - 622.80 m.	30° 11' 30° 790" N	078° 13' 10.827" E	2043.3	2004.2	39.0	3611
215	VIDN_6175	Group of Trees	30° 11' 33.380" N	078° 11' 45.385" E	1911.0	1872.5	38.5	1340
216	VIDN_6178	Group of Trees	30° 11' 30° 676" N	078° 11' 44.430" E	1908.1	1869.9	38.2	1303
217	VIDN_7224	Electric Pole	30° 11' 43.694" N	078° 13' 07.587" E	2055.1	2018.3	36.8	3562
218	VIDN_6285	Group of Trees	30° 11' 37.340" N	078° 13' 01.116" E	2041.4	2004.8	36.6	3366
219	VIDN_5174	Building, Sintex Tank Top - 612.20 m.	30° 11' 35.259" N	078° 12' 42.735" E	2008.5	1972.3	36.2	2870
220	VIDN_7216	Electric Pole	30° 11' 38.761" N	078° 13' 16.184" E	2067.5	2031.3	36.2	3771
221	VIDN_6284	Group of Trees	30° 11' 35.579" N	078° 12' 57.546" E	2033.6	1998.0	35.6	3265
222	VIDN_7305	Flood Light	30° 11' 40.442" N	078° 11' 31.390" E	1930.7	1895.9	34.8	1043
223	VIDN_5200	Building, Sintex Tank Top - 620.84 m.	30° 11' 39.823" N	078° 12' 59.387" E	2036.9	2002.7	34.1	3328
224	VIDN_5172	Building, Sintex Tank Top - 614.46 m.	30° 11' 36.484" N	078° 12' 48.251" E	2015.9	1982.3	33.7	3021
225	VIDN_5207	Building, Sintex Tank Top - 617.35 m.	30° 11' 39.875" N	078° 12' 53.082" E	2025.4	1991.8	33.6	3161
226	VIDN_5295	Building, Staircase Room Top - 627.18 m.	30° 11' 35.952" N	078° 13' 13.010" E	2057.7	2024.8	32.8	3679
227	VIDN_5298	Building, Sintex Tank Top - 625.20 m.	30° 11' 34.860" N	078° 13' 09.720" E	2051.2	2018.8	32.4	3588
228	VIDN_6276	Group of Trees	30° 11' 35.904" N	078° 12' 42.202" E	2003.9	1971.6	32.3	2858
229	VIDN_6270	Group of Trees	30° 11' 31.055" N	078° 12' 48.407" E	2012.8	1980.6	32.3	3012
230	VIDN_5199	Building, Sintex Tank Top - 620.30 m.	30° 11' 38.917" N	078° 12' 59.663" E	2035.1	2002.9	32.2	3332
231	VIDN_6269	Tree	30° 11' 20.553" N	078° 12' 49.360" E	2036.1	2004.2	31.8	3039
232	VIDN_6272	Tree	30° 11' 33.761" N	078° 12' 42.290" E	2002.8	1971.0	31.8	2854
233	VIDN_5178	Building, Staircase Room Top - 613.32 m	30° 11' 36.908" N	078° 12' 47.093" E	2012.2	1980.4	31.8	2991
234	VIDN_5164	Building, Staircase Room Top - 611.78 m	30° 11' 31.248" N	078° 12' 45.523" E	2007.1	1975.6	31.5	2935
235	VIDN_6264	Group of Trees	30° 11' 30° 387" N	078° 12' 35.962" E	1990.3	1958.8	31.4	2678
236	VIDN_6287	Group of Trees	30° 11' 36.339" N	078° 12' 56.809" E	2028.4	1997.0	31.4	3248
237	VIDN_6261	Group of Trees	30° 11' 35.242" N	078° 12' 37.297" E	1993.6	1962.9	30.8	2725
238	VIDN_7127	Electric Pole	30° 11' 34.626" N	078° 12' 38.647" E	1995.2	1965.0	30.2	2759
239	VIDN_7128	Electric Pole	30° 11' 34.012" N	078° 12' 39.912" E	1996.9	1967.0	29.9	2791
240	VIDN_5300	Building(U/C), Staircase Room Top-623.06 m	30° 11' 33.438" N	078° 13' 07.513" E	2044.1	2014.4	29.7	3527
241	VIDN_5229	Building, Staircase Room Top - 626.63 m	30° 11' 36.883" N	078° 13' 13.661" E	2055.9	2026.3	29.6	3699
242	VIDN_7180	Electric Pole	30° 11' 39.640" N	078° 12' 56.924" E	2027.5	1998.4	29.1	3262
243	VIDN_6184	Group of Trees	30° 11' 33.185" N	078° 11' 42.857" E	1897.1	1868.1	29.0	1272
244	VIDN_5216	Building, Staircase Room Top - 621.67 m	30° 11' 40.612" N	078° 13' 03.825" E	2039.6	2010.7	28.9	3449
245	VIDN_7142	Electric Pole	30° 11' 34.746" N	078° 12' 44.424" E	2003.6	1975.0	28.6	2913
246	VIDN_6357	Tree	30° 11' 28.828" N	078° 11' 43.78° " E	1896.5	1868.1	28.4	1281
247	VIDN_5188	Building, Sintex Tank Top - 619.56 m	30° 11' 27.344" N	078° 13' 06.792" E	2032.6	2004.2	28.4	3501
248	VIDN_6085	Group of Trees	30° 11' 24.319" N	078° 10' 12.772" E	1819.4	1791.2	28.1	1159
249	VIDN_6183	Group of Trees	30° 11' 32.812" N	078° 11' 42.851" E	1896.1	1867.9	28.1	1270
250	VIDN_7176	Electric Pole	30° 11' 38.642" N	078° 13' 01.866" E	2034.3	2006.6	27.7	3390
251	VIDN_5168	Building, Sintex Tank Top - 611.90 m	30° 11' 33.374" N	078° 12' 47.473" E	2007.5	1979.8	27.7	2991
252	VIDN_7164	Electric Pole	30° 11' 38.636" N	078° 12' 53.949" E	2020.5	1992.9	27.7	3179
253	VIDN_7129	Electric Pole	30° 11' 33.398" N	078° 12' 41.250" E	1996.6	1969.0	27.6	2825
254	VIDN_5153	Building, Pole Top - 607.81 m	30° 11' 33.950" N	078° 12' 39.793" E	1994.1	1966.7	27.4	2788
255	VIDN_5170	Building, Staircase Room Top - 612.66 m.	30° 11' 35.653" N	078° 12' 48.660" E	2010.0	1982.7	27.3	3029
256	VIDN_7179	Electric Pole	30° 11' 39.865" N	078° 13' 00.005" E	2031.0	2003.8	27.2	3345
257	VIDN_6262	Tree	30° 11' 32.924" N	078° 12' 36.710" E	1987.7	1961.0	26.7	2703
258	VIDN_7218	Electric Pole	30° 11' 33.937" N	078° 13' 13.106" E	2050.7	2024.3	26.5	3677
259	VIDN_5198	Building, Staircase Room Top - 618.79 m.	30° 11' 39.251" N	078° 13' 00.153" E	2030.1	2003.8	26.3	3347
260	VIDN_5171	Building, Staircase Room Top - 612.34 m.	30° 11' 36.174" N	078° 12' 48.607" E	2009.0	1982.8	26.2	3029
261	VIDN_5208	Building, Sintex Tank Top - 613.57 m.	30° 11' 38.742" N	078° 12' 50.519" E	2013.0	1987.0	26.0	3089
262	VIDN_7141	Electric Pole	30° 11' 34.384" N	078° 12' 45.194" E	2001.9	1976.2	25.7	2933
263	VIDN_5196	Building, Staircase Room Top - 618.79 m.	30° 11' 39.126" N	078° 13' 00.568" E	2030.1	2004.5	25.6	3357
264	VIDN_5195	Building, Staircase Room Top - 618.21 m.	30° 11' 37.580" N	078° 12' 59.836" E	2028.2	2002.7	25.6	3332
265	VIDN_5194	Building, Staircase Room Top - 618.03 m.	30° 11' 37.126" N	078° 12' 59.611" E	2027.6	2002.1	25.5	3325
266	VIDN_6280	Group of Trees	30° 11' 32.847" N	078° 12' 52.934" E	2014.5	1989.0	25.5	3136
267	VIDN_5203	Building Top	30° 11' 37.316" N	078° 12' 57.476" E	2023.8	1998.5	25.3	3269
268	VIDN_6271	Group of Trees	30° 11' 32.537" N	078° 12' 47.744" E	2005.1	1979.9	25.1	2997
269	VIDN_5163	Building, Staircase Room Top - 608.24 m.	30° 11' 32.513" N	078° 12' 42.416" E	1995.5	1970.7	24.8	2854
270	VIDN_7178	Electric Pole	30° 11' 39.048" N	078° 13' 01.057" E	2029.9	2005.3	24.5	3370
271	VIDN_5204	Building, Staircase Room Top - 616.25 m.	30° 11' 37.909" N	078° 12' 56.642" E	2021.8	1997.3	24.5	3249
272	VIDN_6282	Group of Trees	30° 11' 23.678" N	078° 12' 54.096" E	2028.6	2004.2	24.4	3162
273	VIDN_5183	Building, Sintex Tank Top - 615.23 m.	30° 11' 34.656" N	078° 12' 55.585" E	2018.5	1994.3	24.2	3211
274	VIDN_5252	Building, Sintex Tank Top - 605.94 m.	30° 11' 34.293" N	078° 12' 38.021" E	1988.0	1963.8	24.2	2741
275	VIDN_6205	Group of Trees	30° 11' 20.662" N	078° 11' 34.790" E	1929.0	1905.3	23.7	1052
276	VIDN_6181	GROUP OF TREE	30° 11' 29.30° " N	078° 11' 42.691" E	1890.1	1866.4	23.7	1253
277	VIDN_7161	Electric Pole	30° 11' 37.005" N	078° 12' 55.608" E	2018.6	1995.2	23.5	3218
278	VIDN_6088	Group of Trees	30° 11' 26.355" N	078° 10' 13.230" E	1825.4	1802.2	23.2	1145
279	VIDN_7130	Electric Pole	30° 11' 32.780" N	078° 12' 42.661" E	1994.2	1971.3	23.0	2862
280	VIDN_7159	Electric Pole	30° 11' 38.088" N	078° 12' 58.544" E	2023.3	2000.6	22.7	3300
281	VIDN_5162	Building, Sintex Tank Top - 603.14 m	30° 11' 31.614" N	078° 12' 34.137" E	1978.8	1956.1	22.7	2632
282	VIDN_6182	Group of Trees	30° 11' 30° 527" N	078° 11' 43.364" E	1890.6	1868.0	22.6	1274
283	VIDN_5166	Building, Staircase Room Top - 611.36 m	30° 11' 30° 877" N	078° 12' 50.070" E	2005.7	1983.4	22.4	3056
284	VIDN_5307	Building, Staircase Room Top - 617.65 m	30° 11' 26.264" N	078° 13' 09.153" E	2026.4	2004.2	22.1	3564
285	VIDN_5202	Building, Staircase Room Top - 616.36 m	30° 11' 38.354" N	078° 12' 58.429" E	2022.1	2000.5	21.6	3298
286	VIDN_7158	Electric Pole	30° 11' 37.381" N	078° 12' 59.274" E	2022.7	2001.6	21.1	3317
287	VIDN_6265	Group of Trees	30° 11' 33.039" N	078° 12' 40.445" E	1988.0	1967.5	20.4	2803
288	VIDN_7132	Electric Pole	30° 11' 32.068" N	078° 12' 44.254" E	1994.2	1973.7	20.4	2903
289	VIDN_7156	Electric Pole	30° 11' 35.415" N	078° 12' 57.917" E	2018.7	1998.6	20.1	3275
290	VIDN_6353	Group of Trees	30° 11' 24.446" N	078° 13' 02.496" E	2024.2	2004.2	19.9	3386
291	VIDN_9194	Hoarding Top	30° 11' 21.348" N	078° 11' 37.292" E	1892.7	1874.0	18.8	1115
292	VIDN_5165	Building, Staircase Room Top - 607.68 m.	30° 11' 32.126" N	078° 12' 44.936" E	1993.7	1974.9	18.7	2921
293	VIDN_7154	Electric Pole	30° 11' 34.070" N	078° 12' 55.089" E	2011.5	1993.2	18.3	3196
294	VIDN_7152	Electric Pole	30° 11' 33.078" N	078° 12' 53.160" E	2007.7	1989.5	18.2	3143
295	VIDN_9200	Spot Elevation	30° 11' 38.697" N	078° 12' 41.125" E	1989.0	1970.7	18.2	2839
296	VIDN_5190	Building, Sintex Tank Top - 616.41 m.	30° 11' 30° 908" N	078° 13' 03.768" E	2022.3	2004.2	18.1	3422
297	VIDN_9202	Spot Elevation	30° 11' 34.992" N	078° 11' 42.884" E	1886.8	1868.8	18.0	1283
298	VIDN_5192	Building, Sintex Tank Top - 617.34 m.	30° 11' 32.694" N	078° 13' 03.654" E	2025.4	2007.5	17.9	3422
299	VIDN_5186	Building, Sintex Tank Top - 616.25 m.	30° 11' 26.085" N	078° 13' 02.493" E	2021.8	2004.2	17.5	3385
300	VIDN_5184	Building, Sintex Tank Top - 612.31 m.	30° 11' 33.517" N	078° 12' 54.168" E	2008.9	1991.4	17.5	3170
301	VIDN_9203	Spot Elevation	30° 11' 32.127" N	078° 11' 43.400" E	1885.7	1868.6	17.0	1281
302	VIDN_8070	AIRPORT WIRE FENCING TOP	30° 11' 32.131" N	078° 11' 42.982" E	1884.8	1867.9	16.9	1270
303	VIDN_7135	Electric Pole	30° 11' 31.240" N	078° 12' 46.038" E	1993.3	1976.5	16.8	2949
304	VIDN_5201	Building Top	30° 11' 37.804" N	078° 12' 58.987" E	2017.9	2001.3	16.6	3311
305	VIDN_7134	Electric Pole	30° 11' 31.580" N	078° 12' 45.323" E	1991.8	1975.4	16.4	2930
306	VIDN_9204	Spot Elevation	30° 11' 30° 458" N	078° 11' 43.721" E	1885.0	1868.6	16.4	1284
307	VIDN_6352	Group of Trees	30° 11' 22.567" N	078° 13' 03.434" E	2020.4	2004.2	16.2	3412
308	VIDN_7153	Electric Pole	30° 11' 33.671" N	078° 12' 54.258" E	2007.7	1991.6	16.1	3173
309	VIDN_7136	Electric Pole	30° 11' 30° 936" N	078° 12' 46.704" E	1993.5	1977.6	15.9	2966
310	VIDN_5191	Building, Sintex Tank Top - 616.72 m.	30° 11' 31.974" N	078° 13' 03.813" E	2023.3	2007.5	15.8	3425
311	VIDN_7151	ELECTRIC POLE	30° 11' 32.658" N	078° 12' 52.314" E	2003.6	1987.9	15.7	3119
312	VIDN_8001	Mobile Road Traffic	30° 11' 32.544" N	078° 11' 45.580" E	1888.2	1872.6	15.7	1341
313	VIDN_8013	Mobile Road Traffic	30° 11' 36.357" N	078° 13' 14.887" E	2043.8	2028.2	15.5	3730
314	VIDN_7150	Electric Pole	30° 11' 32.011" N	078° 12' 51.010" E	2000.4	1985.4	15.0	3083
315	VIDN_7304	FLOOD LIGHT MAST	30° 11' 40.207" N	078° 11' 29.818" E	1929.4	1915.3	14.2	1002
316	VIDN_6089	Group of Trees	30° 11' 25.629" N	078° 10' 14.272" E	1826.7	1813.1	13.6	1117
317	VIDN_7149	Electric Pole	30° 11' 31.582" N	078° 12' 50.140" E	1996.8	1983.7	13.1	3059
318	VIDN_6159	Group of Trees	30° 11' 38.908" N	078° 11' 50.317" E	1975.0	1962.8	12.2	1505
319	VIDN_7148	Electric Pole	30° 11' 31.117" N	078° 12' 49.138" E	1993.9	1981.8	12.1	3032
320	VIDN_8042	MOBILE ROAD TRAFFIC	30° 11' 32.029" N	078° 11' 42.338" E	1878.3	1866.8	11.5	1253
321	VIDN_6095	Group of Trees	30° 11' 14.489" N	078° 10' 16.685" E	1825.0	1814.0	11.0	1113
322	VIDN_7325	Light Pole	30° 11' 28.754" N	078° 11' 41.954" E	1875.4	1864.9	10.5	1232
323	VIDN_8054	MOBILE ROAD TRAFFIC	30° 11' 28.741" N	078° 11' 40.706" E	1872.7	1862.8	9.9	1199
324	VIDN_5356	Watch Tower	30° 11' 28.692" N	078° 11' 41.888" E	1874.7	1864.8	9.9	1230
325	VIDN_8044	Mobile Road Traffic	30° 11' 34.210" N	078° 11' 40.747" E	1874.5	1864.8	9.7	1222
326	VIDN_6092	Group of Trees	30° 11' 26.165" N	078° 10' 15.152" E	1835.6	1826.4	9.3	1093
327	VIDN_8055	Mobile Road Traffic	30° 11' 29.038" N	078° 11' 41.597" E	1873.6	1864.4	9.2	1223
328	VIDN_8041	Mobile Road Traffic	30° 11' 34.122" N	078° 11' 41.902" E	1875.7	1866.8	9.0	1252
329	VIDN_8043	Mobile Road Traffic	30° 11' 29.990" N	078° 11' 42.761" E	1875.2	1866.8	8.4	1257
330	VIDN_7330	Localizer, Pole Top	30° 11' 31.740" N	078° 11' 41.823" E	1874.1	1865.8	8.4	1238
331	VIDN_7331	Localizer, Pole Top	30° 11' 31.423" N	078° 11' 41.892" E	1874.1	1865.8	8.3	1238
332	VIDN_7329	Localizer, Pole Top	30° 11' 32.078" N	078° 11' 41.757" E	1874.1	1865.8	8.3	1238
333	VIDN_7328	Localizer, Pole Top	30° 11' 32.470" N	078° 11' 41.676" E	1874.1	1865.8	8.3	1237
334	VIDN_6189	GROUP OF TREE	30° 11' 27.052" N	078° 11' 44.315" E	1951.7	1943.5	8.2	1293
335	VIDN_5357	Localizer Hut, Lightning Arrester Top	30° 11' 33.872" N	078° 11' 41.539" E	1874.2	1866.1	8.2	1241
336	VIDN_5358	Localizer Hut, Lightning Arrester Top	30° 11' 34.124" N	078° 11' 41.643" E	1874.3	1866.3	8.0	1245
337	VIDN_9216	HILL TOP	30° 16' 03.460" N	078° 13' 46.501" E	2848.4	2840.8	7.5	9682
338	VIDN_4001	Localizer Monitor Antenna,	30° 11' 31.358" N	078° 11' 38.100" E	1865.5	1859.2	6.3	1137
339	VIDN_7026	Cellphone Mast	30° 10' 48.191" N	078° 12' 40.089" E	2010.5	2004.2	6.3	3023
340	VIDN_7327	Localizer, Lightning Arrester Top	30° 11' 31.469" N	078° 11' 41.965" E	1871.8	1865.9	5.9	1240
341	VIDN_7326	Localizer, Lightning Arrester Top	30° 11' 32.438" N	078° 11' 41.760" E	1871.7	1865.9	5.8	1239
342	VIDN_6158	Group of Trees	30° 11' 39.456" N	078° 11' 51.343" E	1975.7	1970.2	5.5	1536
343	VIDN_8032	Airport Boundary Wall With Fencing on Top	30° 11' 32.179" N	078° 11' 42.473" E	1872.5	1867.1	5.4	1257
344	VIDN_8028	Airport Boundary Wall With Fencing on Top	30° 11' 29.392" N	078° 11' 41.912" E	1870.1	1865.1	5.1	1232
345	VIDN_5305	Building, Staircase Room Top - 612.21 m	30° 11' 20.688" N	078° 13' 04.858" E	2008.5	2004.2	4.3	3453
346	VIDN_9144	Localizer, Obstruction Light Top	30° 11' 32.436" N	078° 11' 41.730" E	1869.7	1865.9	3.8	1238
347	VIDN_6091	GROUP OF TREE	30° 11' 24.938" N	078° 10' 15.128" E	1826.7	1822.9	3.8	1095
348	VIDN_9145	Localizer, Obstruction Light Top	30° 11' 31.463" N	078° 11' 41.936" E	1869.4	1865.9	3.5	1240
349	VIDN_8025	Airport Boundary Wall With Fencing on Top	30° 11' 34.470" N	078° 11' 40.842" E	1868.5	1865.1	3.4	1226
350	VIDN_9099	Sign Board	30° 11' 30° 493" N	078° 11' 17.271" E	1847.4	1844.1	3.3	584
351	VIDN_9100	Sign Board	30° 11' 29.353" N	078° 11' 17.560" E	1847.4	1844.1	3.2	585
352	VIDN_8026	Airport Boundary Wall With Fencing on Top	30° 11' 34.631" N	078° 11' 41.950" E	1869.9	1867.0	2.8	1256
353	VIDN_9094	Sign Board	30° 11' 22.872" N	078° 10' 52.569" E	1819.6	1816.9	2.7	139
354	VIDN_9111	Sign Board	30° 11' 31.758" N	078° 11' 32.762" E	1857.9	1855.3	2.6	998
355	VIDN_5359	Localizer Hut Top	30° 11' 34.016" N	078° 11' 41.565" E	1868.5	1866.2	2.4	1242
356	VIDN_9195	Hoarding Top	30° 11' 20.661" N	078° 11' 36.480" E	1888.1	1885.8	2.4	1097
357	VIDN_9105	Sign Board	30° 11' 30° 757" N	078° 11' 26.098" E	1852.7	1850.4	2.3	817
358	VIDN_4002	LOCALIZER ANTENNA TOP	30° 11' 31.942" N	078° 11' 41.791" E	1868.1	1865.8	2.3	1238
359	VIDN_8027	Airport Boundary Wall With Fencing on Top	30° 11' 29.567" N	078° 11' 43.015" E	1869.3	1867.0	2.3	1262
360	VIDN_9093	Sign Board	30° 11' 22.500" N	078° 10' 50.221" E	1816.8	1814.6	2.2	194
361	VIDN_9106	Sign Board	30° 11' 33.200" N	078° 11' 34.532" E	1858.6	1856.6	2.0	1053
362	VIDN_9104	Sign Board	30° 11' 30° 346" N	078° 11' 23.343" E	1851.0	1849.1	1.9	742
363	VIDN_8014	Mobile Road Traffic	30° 11' 25.165" N	078° 13' 07.805" E	2005.7	2004.2	1.5	3528
364	VIDN_9147	Generator Top	30° 11' 34.128" N	078° 11' 41.343" E	1867.1	1865.8	1.3	1237
365	VIDN_9133	Sign Board	30° 11' 26.361" N	078° 10' 55.964" E	1823.1	1822.2	1.0	3
366	VIDN_9115	APPROACH LIGHT	30° 11' 17.925" N	078° 10' 13.546" E	1785.1	1784.1	1.0	1165
367	VIDN_9118	PAPI	30° 11' 21.205" N	078° 10' 26.428" E	1792.2	1792.0	0.2	807

AERONAUTICAL INFORMATION UPTO NOVEMBER 2024

COMPILED BY: CARTO, AIRPORT AUTHORITY OF INDIA

(UPDATED ON- 10-12-2024)

AAI DRG. NO.14/DEHRADUN/2024(CARTO)