
AIRCRAFT PARKING/ DOCKING CHART-APRON C

APRON ELEV.1270 FT

TWR 125.25 MHZ

JAIPUR, INDIA
JAIPUR INTL. AIRPORT

- **DATUM:WGS-84**
- **DIMESNSIONS IN METERS**
- **ELEVATION IN FEET(EGM-08)**

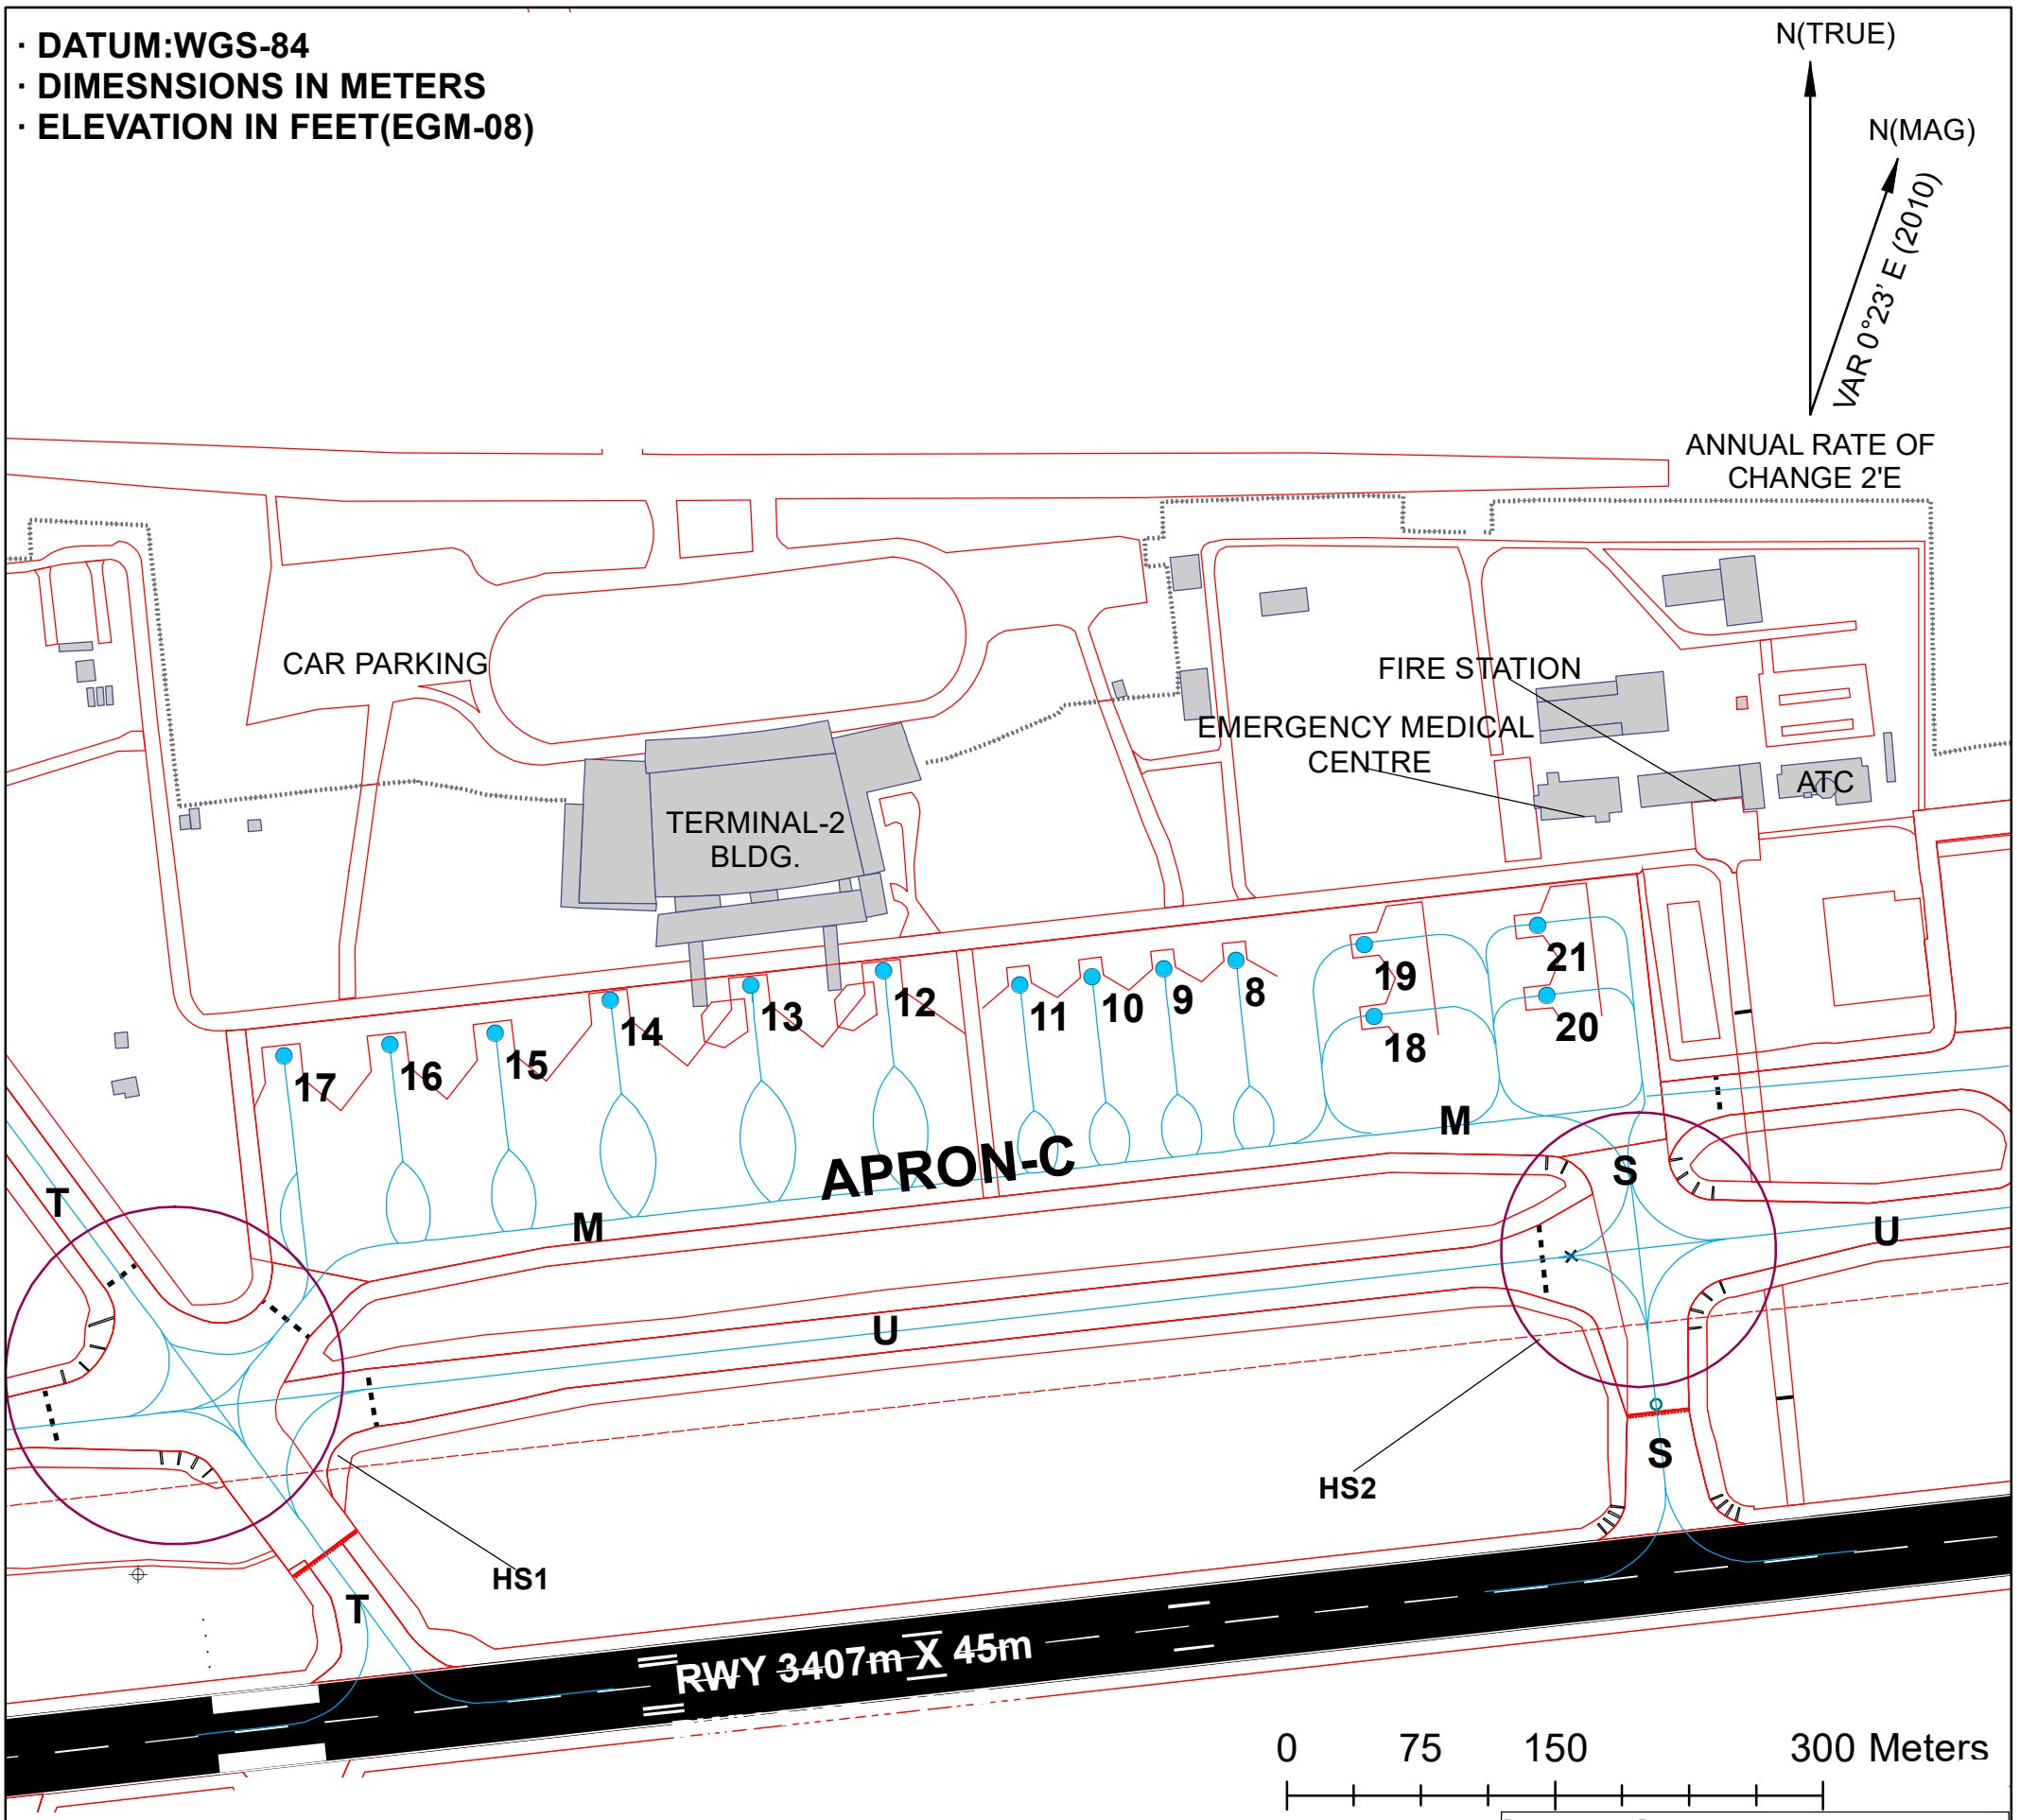

Legend

- AIRCRAFT STAND
- HOTSPOT
- LEAD-IN LINE
- TAXIWAY HOLDING POSITION

Pilot must exercise caution while crossing Hot spot	
HS1	Intersection of TWY U with TWY T & TWY M
HS2	Intersection of TWY S with TWY M & TWY U

STAND NO	COORDINATES FOR AIRCRAFT STAND		PCR	SUITABILITY	STATUS	ELEV (FT)
	LATITUDE	LONGITUDE				
STAND 8	26° 49' 38.066" N	075° 48' 31.236" E	1489/R/C/W/T	UPTO B737/A321	POWER-IN PUSH-BACK	1264
STAND 9	26° 49' 37.929" N	075° 48' 29.776" E	1489/R/C/W/T	UPTO B737/A321	POWER-IN PUSH-BACK	1264
STAND 10	26° 49' 37.791" N	075° 48' 28.317" E	1489/R/C/W/T	UPTO B737/A321	POWER-IN PUSH-BACK	1265
STAND 11	26° 49' 37.655" N	075° 48' 26.858" E	1489/R/C/W/T	UPTO B737/A321	POWER-IN PUSH-BACK	1265
STAND 12	26° 49' 37.924" N	075° 48' 24.103" E	1489/R/C/W/T	UPTO B747-400	POWER-IN PUSH-BACK	1266
STAND 13	26° 49' 37.670" N	075° 48' 21.403" E	1489/R/C/W/T	UPTO B747-400	POWER-IN PUSH-BACK	1266
STAND 14	26° 49' 37.421" N	075° 48' 18.564" E	1489/R/C/W/T	UPTO B747-400	POWER-IN PUSH-BACK	1267
STAND 15	26° 49' 36.839" N	075° 48' 16.228" E	1489/R/C/W/T	UPTO B767-400	POWER-IN PUSH-BACK	1267
STAND 16	26° 49' 36.639" N	075° 48' 14.083" E	1489/R/C/W/T	UPTO B767-400	POWER-IN PUSH-BACK	1269
STAND 17	26° 49' 36.436" N	075° 48' 11.938" E	1489/R/C/W/T	UPTO B767-400	POWER-IN PUSH-BACK	1270
STAND 18	26° 49' 37.031" N	075° 48' 34.031" E	1489/R/C/W/T	UPTO ATR72/Q 400	POWER-IN POWER-OUT	1262
STAND 19	26° 49' 38.338" N	075° 48' 33.843" E	1489/R/C/W/T	UPTO ATR72/Q 400	POWER-IN POWER-OUT	1263
STAND 20	26° 49' 37.636" N	075° 48' 37.450" E	1489/R/C/W/T	UPTO ATR72	POWER-IN POWER-OUT	1261
STAND 21	26° 49' 38.676" N	075° 48' 37.349" E	1489/R/C/W/T	UPTO ATR72	POWER-IN POWER-OUT	1262

TWY	PCR	WIDTH/SHOULDER
TWY-S	931/R/C/W/T	23m/10.5m
TWY-T	708/F/B/W/T(FOR FIRST 275m SECTION OF 1100m LONG TWY T-FROM THE EDGE OF THE RWY) 532/F/C/W/T(FOR NEXT 305m SECTION OF TWY-T TOWARDS APRON-D) 606/F/B/W/T(FOR LAST 520m SECTION OF TWY-T TOWARDS APRON-D)	23m/10.5m
TWY-U	750/F/B/W/T (BETWEEN RWY 08 BEGINING & TWY T) 931/R/C/W/T (BETWEEN TWY-T & TWY-R)	23m/10.5m
TWY-M	931/R/C/W/T	23m/10.5m

COORDINATE SYSTEM:WGS 1984 ZONE 43 N