AERODROME CHART

22°48'52.39"N
086°10'08.45"E

AD.ELEV. 481ft.

TWR 119.225 /122.1

JAMSHEDPUR / INDIA

JAMSHEDPUR AIRPORT


RWY	DIRECTION	THR CO-ORDINATES	THR ELEV.	BEARING STRENGTH
08	082°	22°48'48.20"N 086°09'59.91"E	474	33/F/B/W/T
26	262°	22°48'51.44"N 086°10'22.44"E	466	

* DATUM :
  HORIZONTAL : WGS-84
  VERTICAL : EGM-08
* DIMENSIONS IN METRES
* ELEVATIONS IN FEET

N (True)
N (Mag)
VAR. 0°30'W(2010)
ANNUAL RATE OF CHANGE 1'E


DECLARED DISTANCES (IN METRES)

RWY	TORA	TODA	ASDA	LDA
08	1030	1030	1030	700
26	1030	1030	1030	980

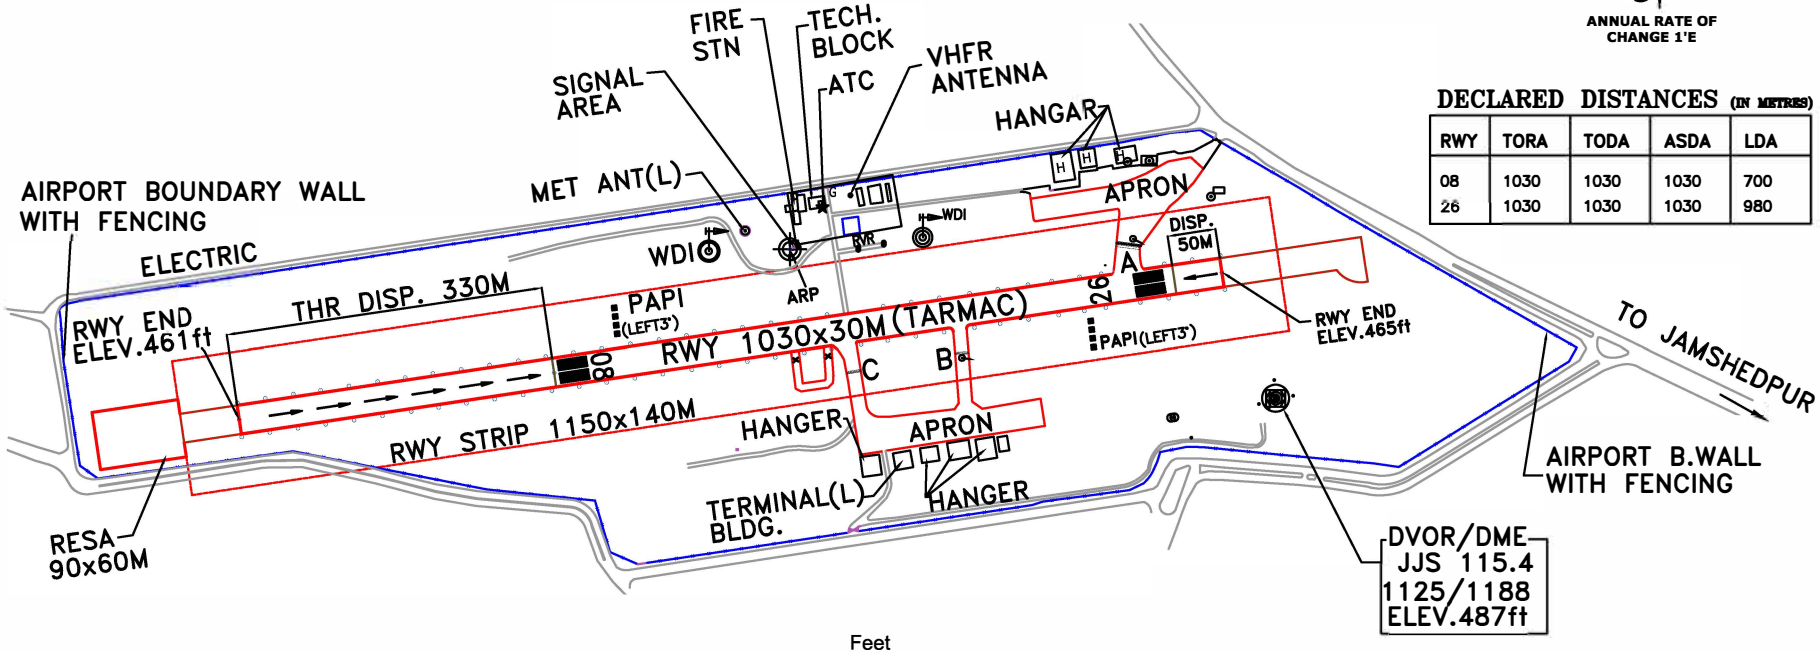

LEGEND	
RWY-HOLDING POSITION	
VOR CHECK POINT	

MARKING AIDS RWY 08/26

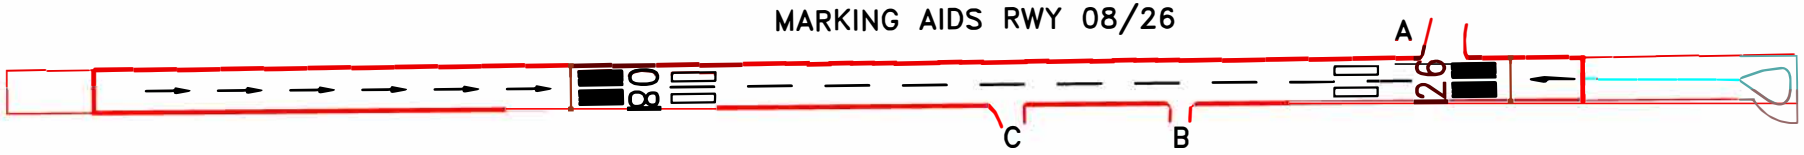

DATE OF AERONAUTICAL INFORMATION
AUGUST 2022

DRG NO.: AAI/AC-56/2022
UPDATED AS ON : 15-11-2022