AIRCRAFT PARKING/ DOCKING CHART


APRON ELEV - 31 ft

TWR 118.1
GND 121.9

MUMBAI, INDIA

APRON - V

CHHATRAPATI SHIVAJI MAHARAJ INTL AIRPORT

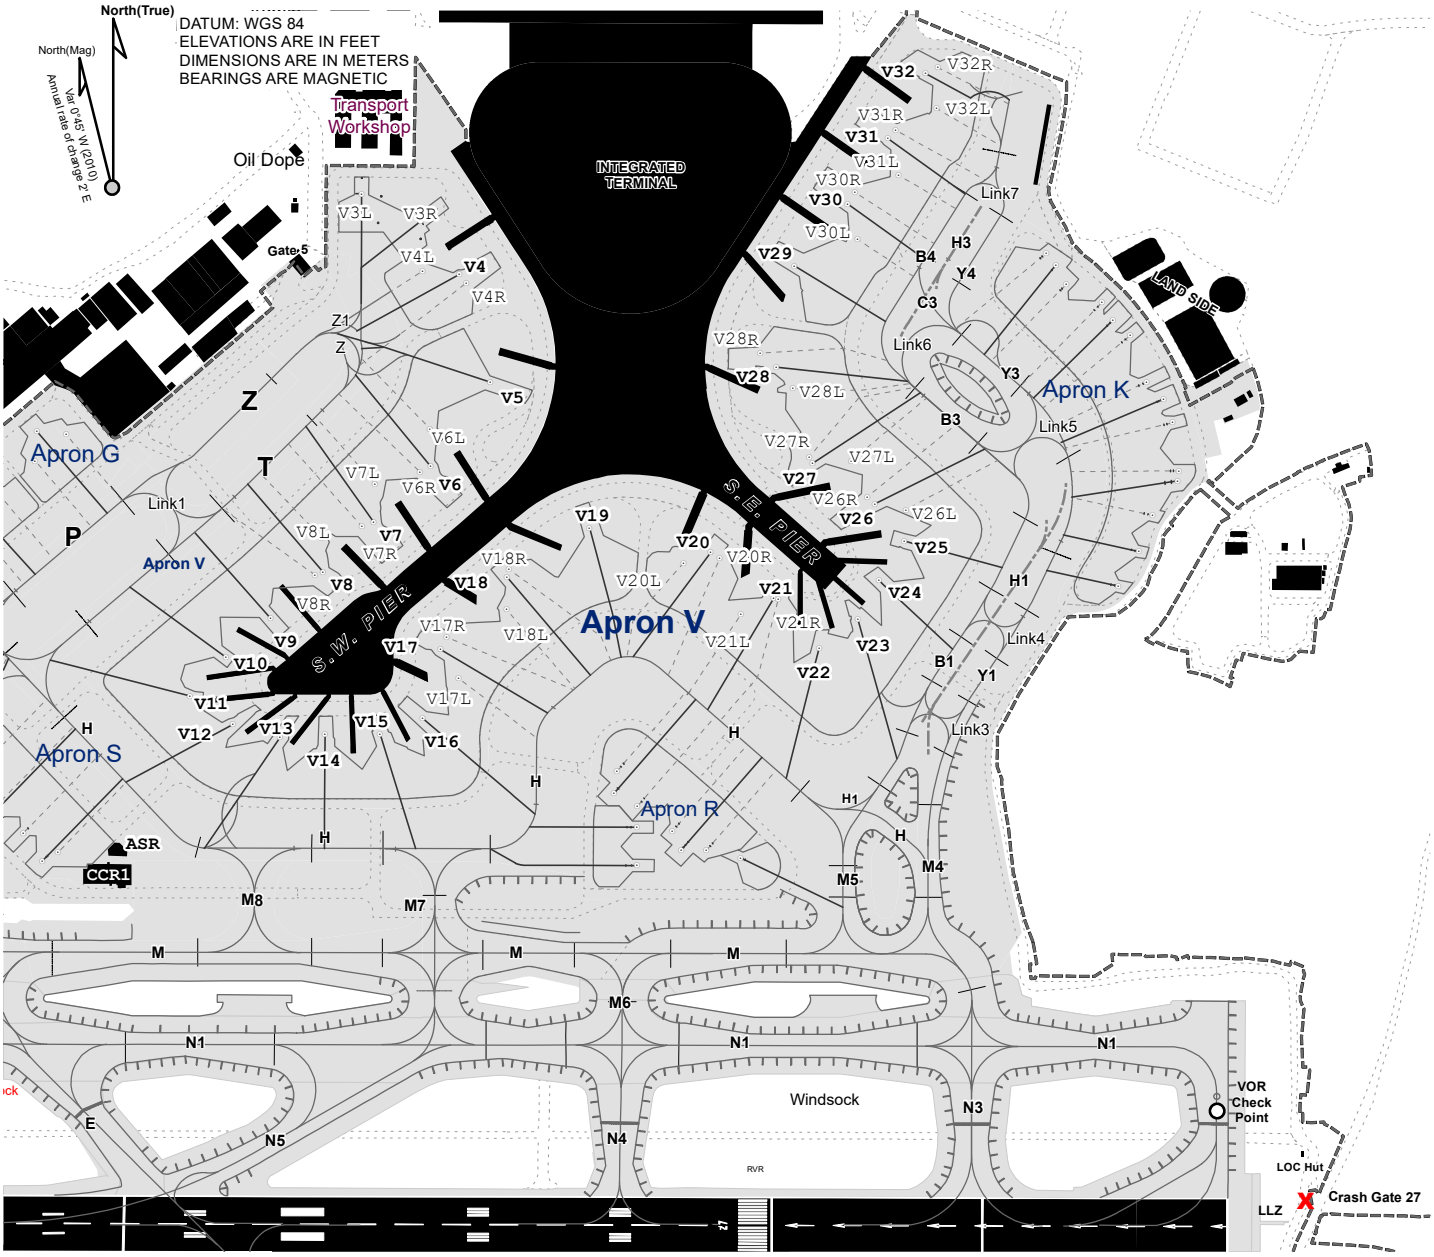

Scale : 1:8000

0 100 200 400 600 800 1,000 Meters

Stand	Latitude	Longitude	Type of Aircraft	PCR Value
V3L	19° 05' 55.127" N	072° 52' 18.278" E	A321, B739	906/R/B/W/T
V3R	19° 05' 54.137" N	072° 52' 20.523" E	A321, B739	931/R/C/W/T
V4L	19° 05' 52.423" N	072° 52' 20.624" E	A321, B739	869/R/A/W/T
V4	19° 05' 52.328" N	072° 52' 21.957" E	B744, A346	1506/R/B/W/T
V4R	19° 05' 52.042" N	072° 52' 22.223" E	A321, B739	906/R/B/W/T
V5	19° 05' 48.638" N	072° 52' 23.150" E	B744, A346	1506/R/B/W/T
V6L	19° 05' 46.992" N	072° 52' 20.998" E	A321, B739	906/R/B/W/T
V6	19° 05' 45.706" N	072° 52' 21.035" E	B744, A346	1506/R/B/W/T
V6R	19° 05' 45.511" N	072° 52' 20.653" E	A321, B739	906/R/B/W/T
V7L	19° 05' 45.067" N	072° 52' 19.035" E	A321, B739	906/R/B/W/T
V7	19° 05' 43.747" N	072° 52' 19.007" E	B744, A346	1506/R/B/W/T
V7R	19° 05' 43.586" N	072° 52' 18.589" E	A321, B739	906/R/B/W/T
V8L	19° 05' 43.175" N	072° 52' 17.147" E	A321, B739	869/R/A/W/T
V8	19° 05' 42.003" N	072° 52' 17.214" E	B744, A346	1506/R/B/W/T
V8R	19° 05' 41.891" N	072° 52' 16.929" E	A321, B739	906/R/B/W/T
V9	19° 05' 40.378" N	072° 52' 15.346" E	B744, A346	1506/R/B/W/T
V10	19° 05' 39.021" N	072° 52' 13.745" E	B744, A346	1506/R/B/W/T
V11	19° 05' 37.664" N	072° 52' 12.469" E	B744, A346	1506/R/B/W/T
V12	19° 05' 36.704" N	072° 52' 14.035" E	B744, A346	1506/R/B/W/T
V13	19° 05' 36.286" N	072° 52' 15.751" E	B744, A346	1765/R/C/W/T
V14	19° 05' 36.435" N	072° 52' 17.384" E	B744, A346	1765/R/C/W/T
V15	19° 05' 36.468" N	072° 52' 19.377" E	B744, A346	1506/R/B/W/T
V16	19° 05' 37.030" N	072° 52' 20.906" E	B744, A346	1765/R/C/W/T
V17L	19° 05' 38.433" N	072° 52' 22.176" E	A321, B739 WL	906/R/B/W/T
V17	19° 05' 39.407" N	072° 52' 21.516" E	B744, A346, A380	1765/R/C/W/T
V17R	19° 05' 39.835" N	072° 52' 21.728" E	A321, B739 WL	906/R/B/W/T
V18L	19° 05' 40.822" N	072° 52' 23.871" E	A321, B739	906/R/B/W/T
V18	19° 05' 41.950" N	072° 52' 23.870" E	B748, A388	1506/R/B/W/T
V18R	19° 05' 42.204" N	072° 52' 23.941" E	A321, B739	906/R/B/W/T

Stand	Latitude	Longitude	Type of Aircraft	PCR Value
V19	19° 05' 43.675" N	072° 52' 26.829" E	B744, A346	1506/R/B/W/T
V20L	19° 05' 42.539" N	072° 52' 30.266" E	A321, B739	906/R/B/W/T
V20	19° 05' 42.905" N	072° 52' 31.232" E	B748, A388	1765/R/C/W/T
V20R	19° 05' 42.697" N	072° 52' 31.559" E	A321, B739	906/R/B/W/T
V21L	19° 05' 40.840" N	072° 52' 32.390" E	A321, B739	906/R/B/W/T
V21	19° 05' 41.362" N	072° 52' 33.539" E	B748, A388	1765/R/C/W/T
V21R	19° 05' 41.343" N	072° 52' 33.704" E	A321, B739	931/R/C/W/T
V22	19° 05' 39.688" N	072° 52' 35.219" E	B744, A346	1765/R/C/W/T
V23	19° 05' 40.695" N	072° 52' 36.595" E	B744, A346	1765/R/C/W/T
V24	19° 05' 42.042" N	072° 52' 37.335" E	B744, A346	1506/R/B/W/T
V25	19° 05' 43.416" N	072° 52' 38.226" E	B744, A346	1506/R/B/W/T
V26L	19° 05' 44.492" N	072° 52' 38.265" E	A321, B739	931/R/C/W/T
V26	19° 05' 44.673" N	072° 52' 37.147" E	B744, A346	1175/R/A/W/T
V26R	19° 05' 44.901" N	072° 52' 36.854" E	A321, B739	906/R/B/W/T
V27L	19° 05' 46.145" N	072° 52' 36.268" E	A321, B739	906/R/B/W/T
V27	19° 05' 46.043" N	072° 52' 34.872" E	B744, A346	1175/R/A/W/T
V27R	19° 05' 46.250" N	072° 52' 34.740" E	A321, B739	906/R/B/W/T
V28L	19° 05' 48.593" N	072° 52' 34.100" E	A321, B739	931/R/C/W/T
V28	19° 05' 49.326" N	072° 52' 33.484" E	B744, A346	1175/R/A/W/T
V28R	19° 05' 49.799" N	072° 52' 32.902" E	A321, B739	906/R/B/W/T
V29	19° 05' 52.818" N	072° 52' 34.074" E	B744, A346	1506/R/B/W/T
V30L	19° 05' 53.790" N	072° 52' 36.290" E	A321, B739	931/R/C/W/T
V30	19° 05' 54.980" N	072° 52' 35.968" E	B744, A346	1175/R/A/W/T
V30R	19° 05' 55.390" N	072° 52' 36.227" E	A321, B739	869/R/A/W/T
V31L	19° 05' 56.000" N	072° 52' 37.794" E	A321, B739	717/R/C/W/T
V31	19° 05' 57.247" N	072° 52' 37.391" E	B744, A346	1506/R/B/W/T
V31R	19° 05' 57.542" N	072° 52' 37.666" E	A321, B739	906/R/B/W/T
V32L	19° 05' 58.310" N	072° 52' 39.100" E	A321, B739	906/R/B/W/T
V32	19° 05' 59.508" N	072° 52' 38.720" E	B772, B744	1175/R/A/W/T
V32R	19° 05' 59.723" N	072° 52' 39.155" E	A321, B739	906/R/B/W/T

Taxiway	PCR	Width
H (BTN.M5 - M4)	1506/R/B/W/T	23m
Taxilane H (BTN. TXL P - M7)	1506/R/B/W/T	23m
Taxilane H (BTN.M7 - M5)	1506/R/B/W/T	25m
Taxilane H1	1175/R/A/W/T	23m
Taxilane H3	1506/R/B/W/T	23m
Z	906/R/B/W/T	15m
Z1	906/R/B/W/T	15m
Taxilane T	1765/R/C/W/T	23m
Taxilane P	1506/R/B/W/T	23m
B1	906/R/B/W/T	18m
Y1	906/R/B/W/T	18m
Taxilane B3	1506/R/B/W/T	23m
Taxilane Y3	1506/R/B/W/T	23m
B4	906/R/B/W/T	18m
Y4	906/R/B/W/T	18m
E	1506/R/B/W/T	23m
Link 3	906/R/B/W/T	18m
Link C3	906/R/B/W/T	18m
Link 1 (Northern Segment)	1506/R/B/W/T	18m
Link 1 (Southern Segment)	1506/R/B/W/T	23m
Link 4	906/R/B/W/T	18m
Link 5 (Northern Segment)	1765/R/C/W/T	23m
Link 5 (Southern Segment)	1765/R/C/W/T	18m
Link 6	1765/R/C/W/T	23m
Link 7	906/R/B/W/T	18m
M	1765/R/C/W/T	25m
M (BTN. M6-M7)	1400/R/D/W/T	23m
M4 (BTN. TXL H1-M)	1506/R/B/W/T	23m
M4 (BTN. M-N1)	1506/R/B/W/T	25m
M5	1175/R/A/W/T	25m
M6	1765/R/C/W/T	25m
M7	1765/R/C/W/T	25m
M8	1765/R/C/W/T	23m
N1	1765/R/C/W/T	25m
N3	1765/R/C/W/T	25m
N4	1506/R/B/W/T	23m

NOTE:-

1. Taxilane centerline lights of Code E Taxilane H1 and H3 are alternate orange and green wherein first light at point of tangency is of orange color.
2. Taxiways/taxilane B1, Y1, B3, Y3, B4, Y4, link 4, Link 5 (southern segment), Link 6 and Link 7 are provided with Standard centerline marking and lights. Link 3 and Link C3 are code C compliant marked with standard centerline marking but not provided with centerline lights.
3. Width of Link 5 Northern Segment, Link 6, Taxilane B3 and Taxilane Y3 is 23m and are compatible for Aircraft up to Code E. However rest of the portion of TWY B1/B4 & TWY Y1/Y4 are 18m wide and compatible for Aircraft up to Code C.
4. Aircraft taxiing on parallel code C TWYs B1/Y1 and TWY B4/Y4 shall not exceed taxiing speed of 10 knots.
5. All Aircraft parking stands are power in push back.
6. All stands are Contact Stands, except Stands V3L and V3R
7. All Aircraft parking stands are provided with A-VDGS (except V28, V30, V31 and V32).

NOTE : AERONAUTICAL GROUND LIGHTS ARE NOT SHOWN IN THIS CHART

Coordinate System : WGS 1984 UTM Zone 43 N