AERODROME CHART

ARP
25° 35' 37.18"N
085° 05' 31.15"E

AD. ELEV 175ft

TWR 118.300


PATNA, INDIA
JAI PRAKASH NARAYAN INT'L. AIRPORT PATNA


RWY	DIRECTION	THR CO-ORDINATES	THR ELEV.	BEARING STRENGTH
07	69	25°35'19.10"N 085°04'53.40"E	175ft	503/F/C/W/T
25	249	25°35'37.55"N 085°05'44.80"E	175ft	

DATUM :
HORIZONTAL : WGS - 84
VERTICAL : EGM - 08
ELEVATIONS IN FEET
DIMENSION IN METRES

DECLARED DISTANCES (IN METRES)				
RWY	TORA	TODA	ASDA	LDA
07	2072	2072	2072	1677
25	2072	2072	2072	1938

LEGEND	
DVOR CHECK POINT	
RWY HOLDING POINT	

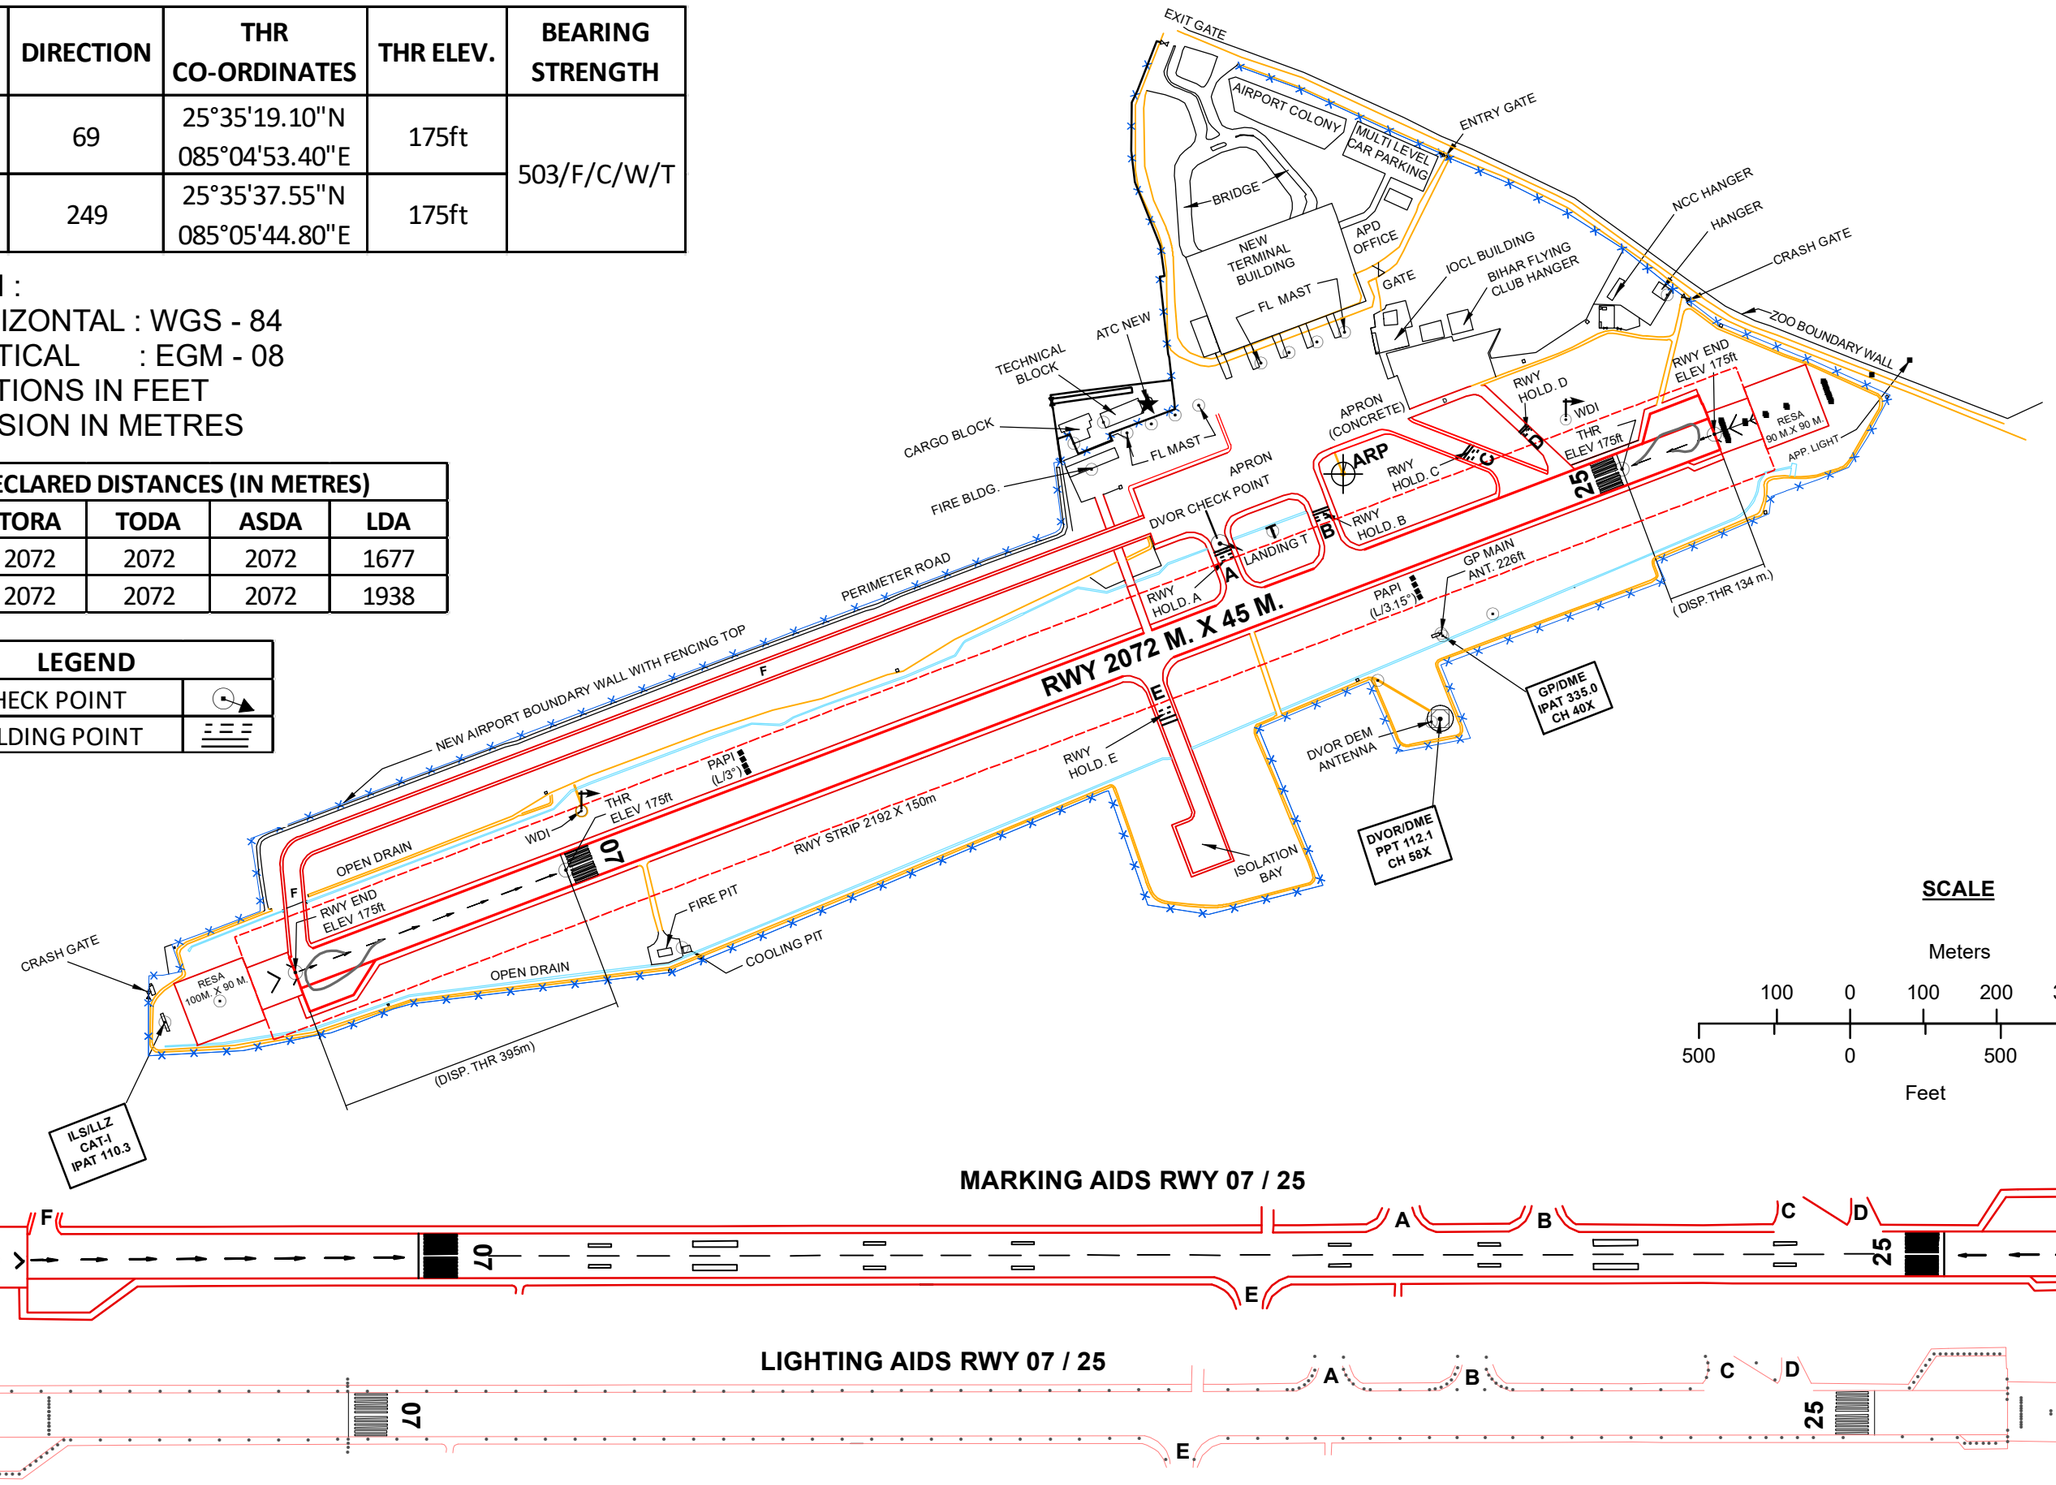

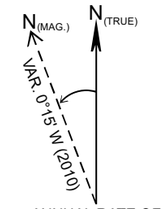


SCALE

Meters
100 0 100 200 300 400
500 0 500 1,000
Feet

MARKING AIDS RWY 07 / 25

LIGHTING AIDS RWY 07 / 25

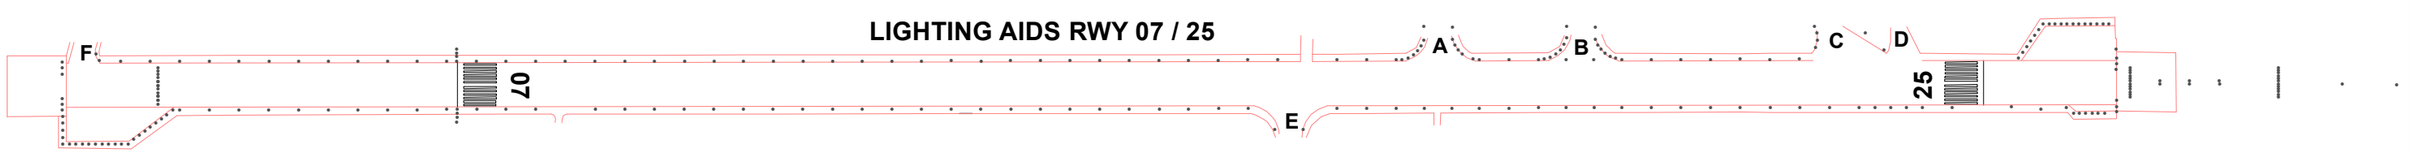

DATE OF AERONAUTICAL INFORMATION
JANUARY 2026.

(UPDATED ON- 10.07.2026)

DRG. NO. - AAI/28-AC/2025