AERODROME CHART

11°46'51.58"N
78°03'51.09"E

AD.ELEV. 1010ft

TWR 122.400
BACK UP 118.850

SALEM, INDIA

SALEM AIRPORT

RWY	DIRECTION	THR CO-ORDINATES	THR ELEV.	PCR STRENGTH
04	036°	11°46'31.98"N 78°03'35.50"E	987ft	360/F/B/W/T
22	216°	11°47'21.11"N 78°04'09.54"E	1010ft	

* DATUM :
HORIZONTAL : WGS-84
VERTICAL : EGM-08
* DIMENSIONS IN METRES
* BEARINGS ARE MAGNETIC
* ELEVATIONS IN FEET

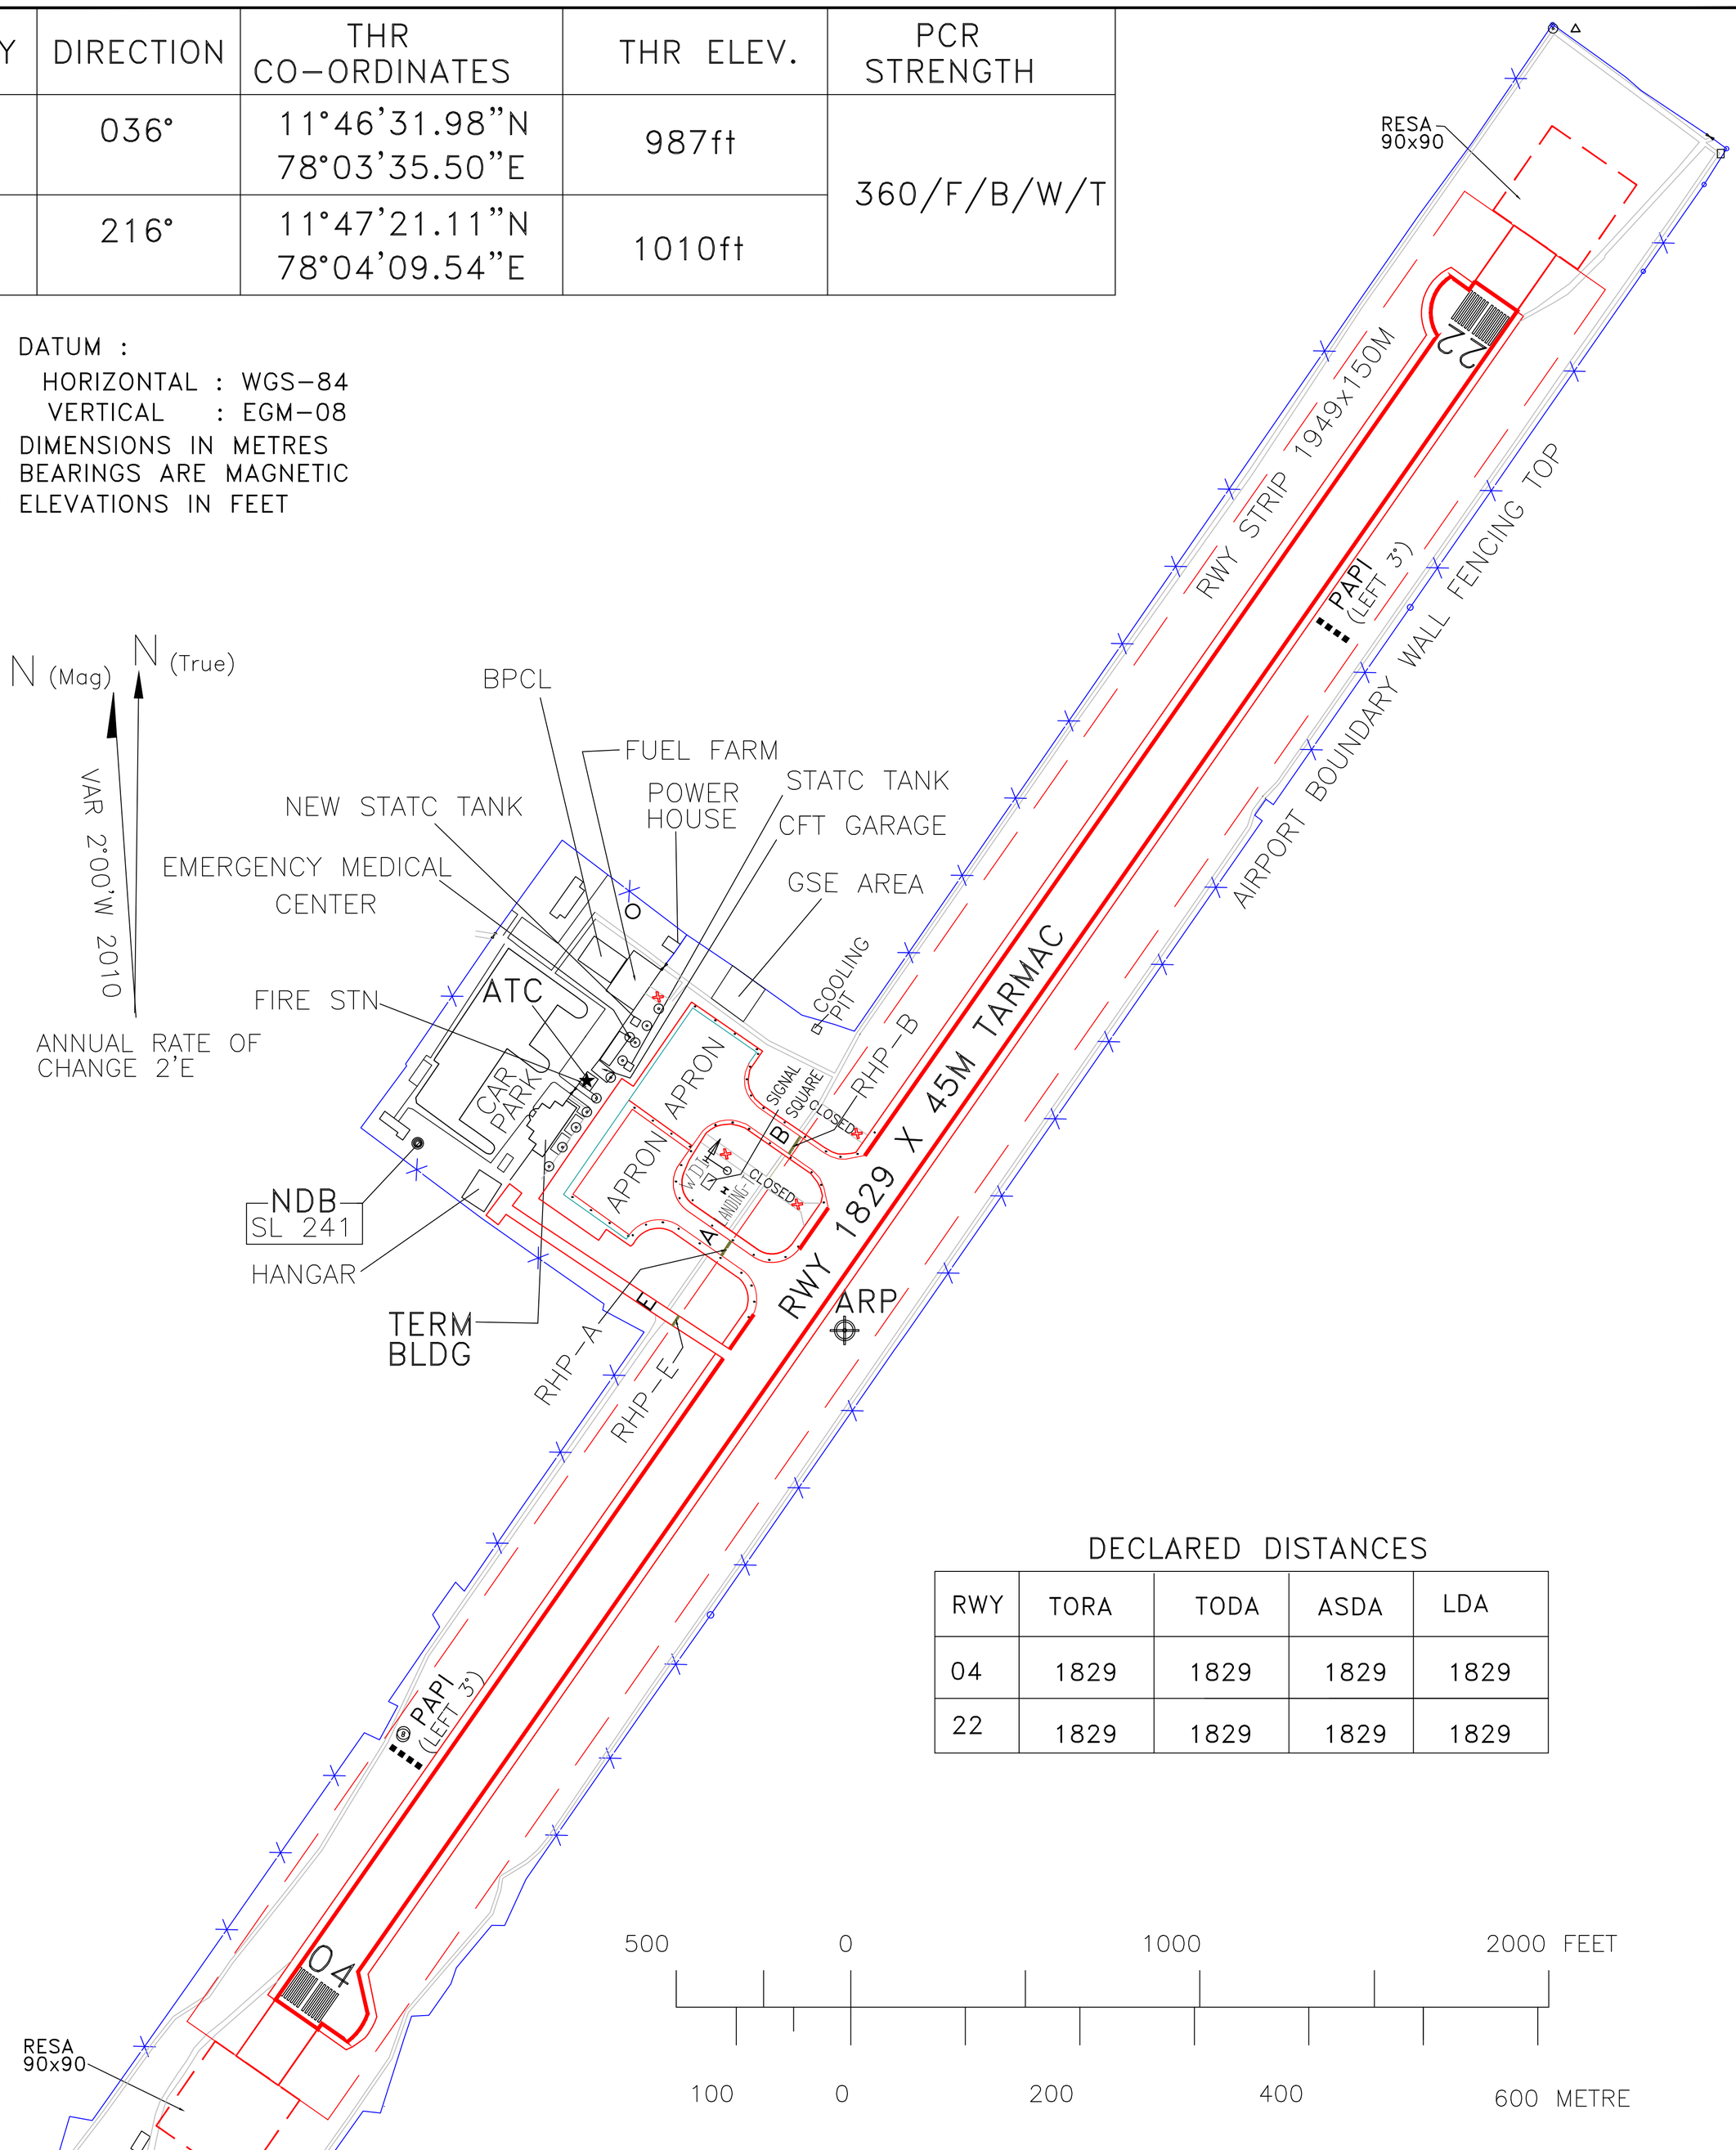

DECLARED DISTANCES

RWY	TORA	TODA	ASDA	LDA
04	1829	1829	1829	1829
22	1829	1829	1829	1829

500 0 1000 2000 FEET

100 0 200 400 600 METRE

MARKING AIDS RUNWAY 04/22

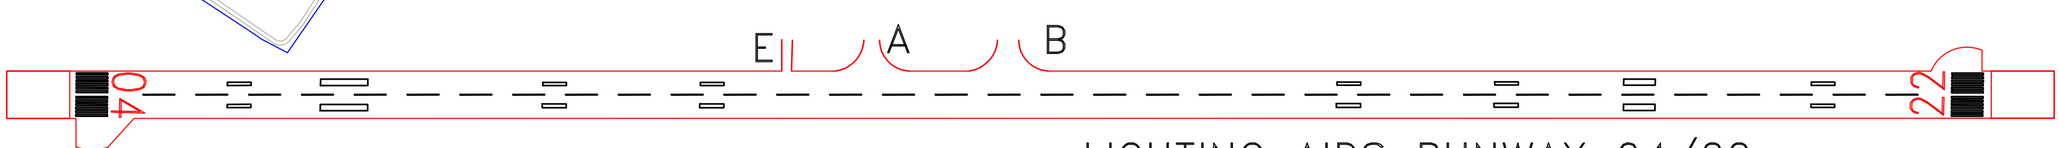

LIGHTING AIDS RUNWAY 04/22

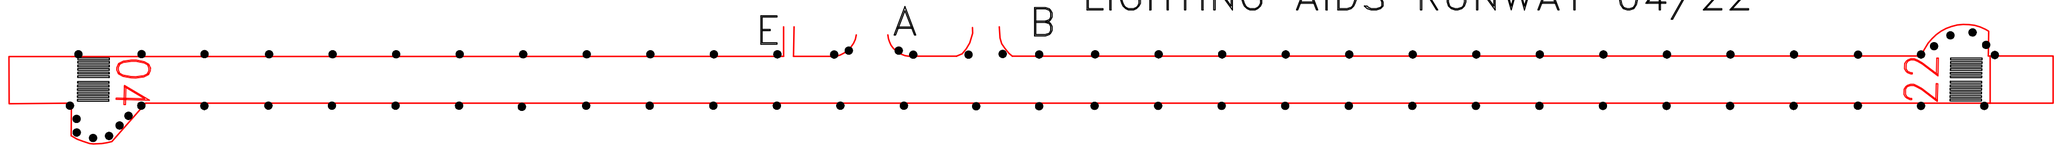

DATE OF AERONAUTICAL INFORMATION
DESEMBER 2025

DRG NO.: AAI/AC-23/2022
UPDATED AS ON 16.01.2026