
AIRCRAFT PARKING/
DOCKING CHART

APRON ELEV 995ft.

TWR 122.400
BACK UP 118.850

SALEM, INDIA

SALEM AIRPORT

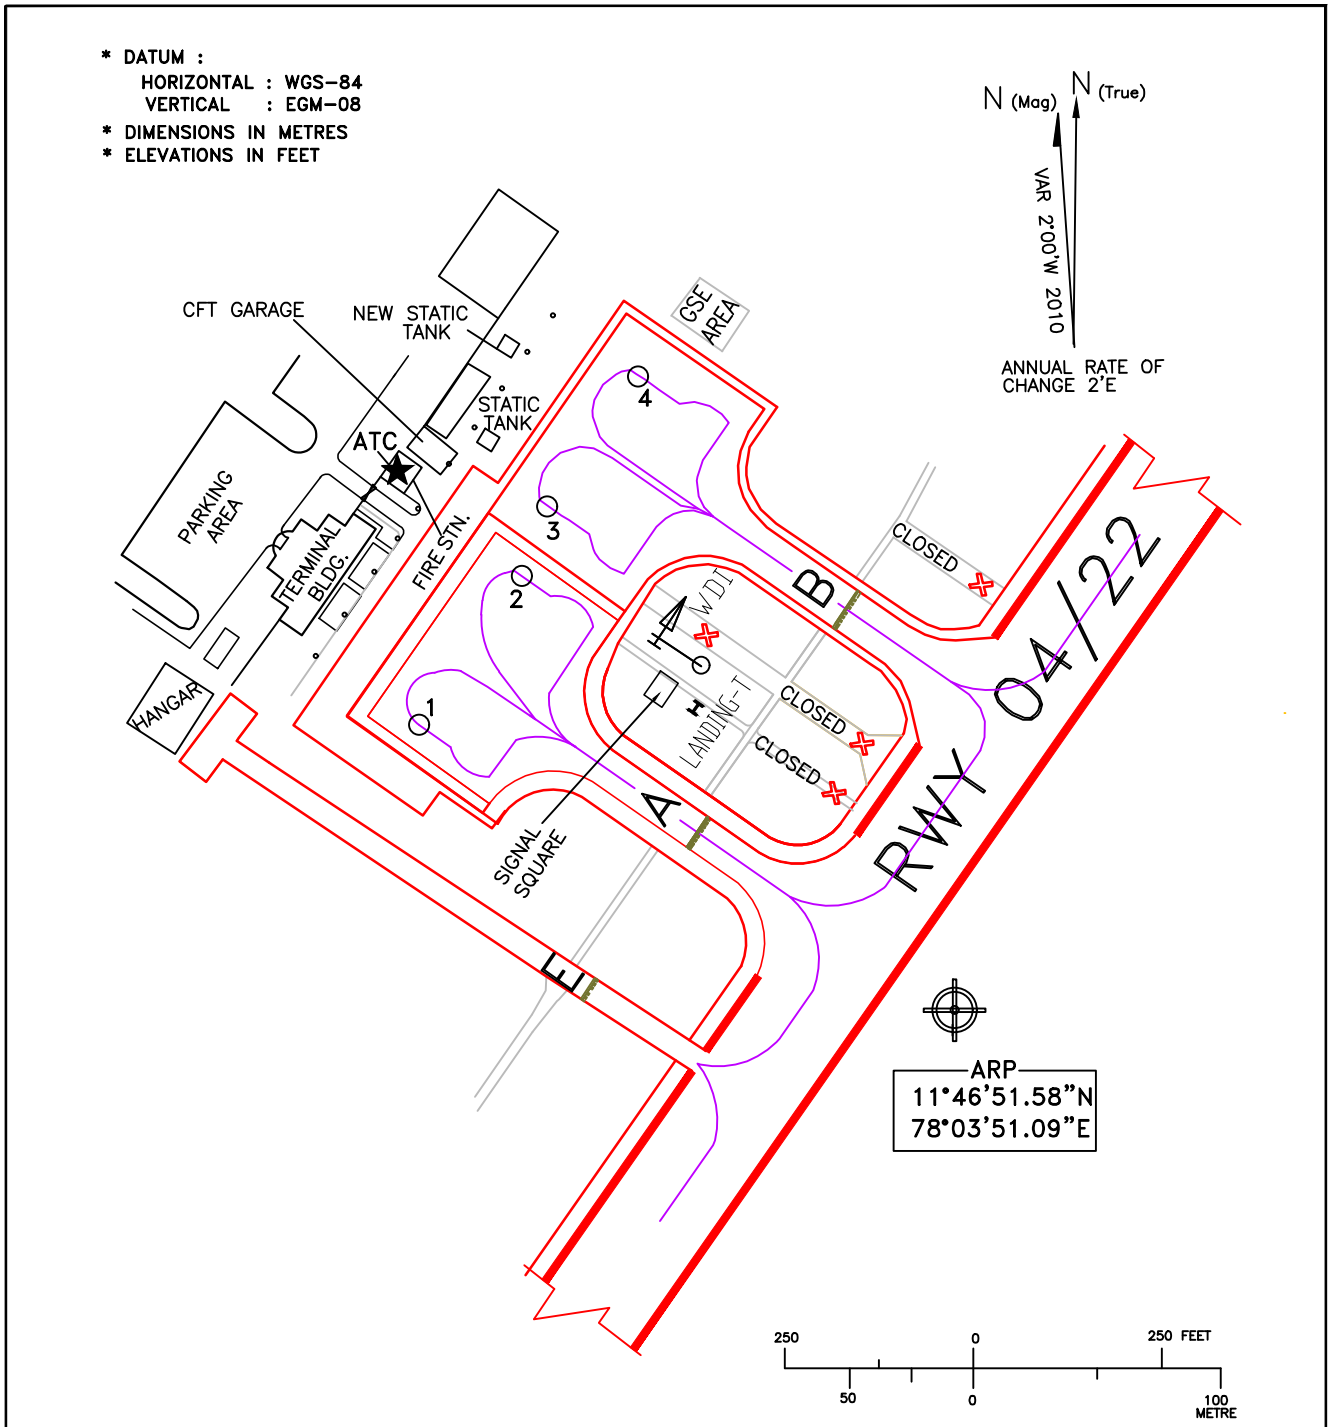

LEGEND	
AIRCRAFT STAND	4
TAXI–HOLDING POSITION	

STAND No.	WGS CO–ORDINATES FOR AIRCRAFT STANDS	SUITABLITY	STATUS	PCR	ELEV.
1.	11°46'55.23587"N 078°03'43.91388"E	AT72	POWER IN/POWER OUT	465/F/B/W/T	995ft
2.	11°46'57.20569"N 078°03'45.26066"E	AT72	POWER IN/POWER OUT	465/F/B/W/T	995ft
3.	11°46'57.89300"N 078°03'45.86347"E	AT72	POWER IN/POWER OUT	240/R/B/W/T	995ft
4.	11°46'59.69908"N 078°03'47.10473"E	AT72	POWER IN/POWER OUT	240/R/B/W/T	995ft

TAXIWAY	PCR	WIDTH
A	350/F/B/W/T	15M
B	240/R/B/W/T	18M
E	30/F/C/X/T	9M

DATE OF AERONAUTICAL INFORMATION
DECEMBER 2025

DRG NO.: AAI/PDC–24/2022

UPDATED AS ON 07.05.2026