IFR CODE 4

ALL DISTANCES ARE IN METERS

ELEVATIONS IN FEET (EGM 08)

AERODROME ELEVATION - 2030 Ft

ALL CO-ORDINATES ARE IN "WGS-84" SYSTEM

AERODROME OBSTACLE CHART-TYPE B

HORIZONTAL SCALE 1:20000

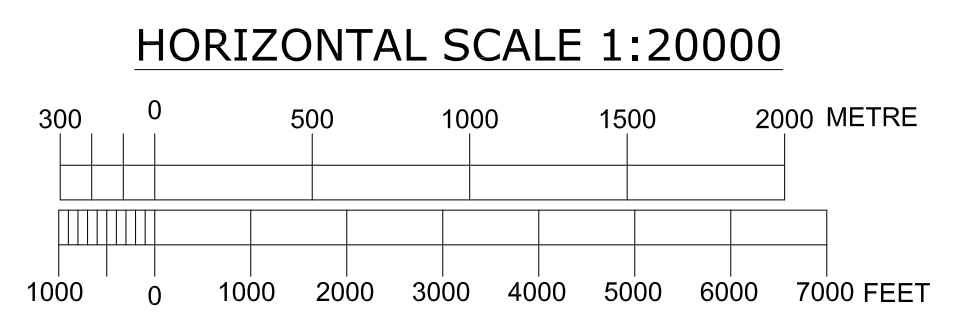

SR.NO	UUID	OBJECT NAME	TOP ELEV. IN FT	DISTANCE FROM ARP	LAT	LONG	RWY 09R-27L			RWY 09L-27R			RWY 10-28		
							PERMISSIBLE IN M	PENETRATION IN M	SURFACE	PERMISSIBLE IN M	PENETRATION IN M	SURFACE	PERMISSIBLE IN M	PENETRATION IN M	SURFACE
~~1~~	~~VOHS_6079~~	~~Tree~~	~~2004~~	~~2608~~	~~17°13'35.786"N~~	~~078°24'32.858"E~~	~~610.6~~	~~0.3~~	~~IN TS~~	~~643.5~~	~~Clear~~	~~IN TS~~	~~-~~	~~-~~	~~-~~
~~2~~	~~VOHS_6080~~	~~Tree~~	~~1993~~	~~2412~~	~~17°13'36.745"N~~	~~078°24'40.460"E~~	~~607.2~~	~~0.3~~	~~IN TS~~	~~640.1~~	~~Clear~~	~~IN TS~~	~~-~~	~~-~~	~~-~~
~~3~~	~~VOHS_6081~~	~~Tree~~	~~1978~~	~~2359~~	~~17°13'39.479"N~~	~~078°24'40.503"E~~	~~602.7~~	~~0.1~~	~~IN APP Funnel 09R / TAKEOFF 27L~~	~~628.1~~	~~Clear~~	~~IN TS~~	~~-~~	~~-~~	~~-~~
4	VOHS_9013	Approach Light	1972	2212	17°13'42.854"N	078°24'44.084"E	600.6	0.4	Within RWY Strip	613.6	Clear	IN TS	-	-	-
5	VOHS_9014	Approach Light	1972	2187	17°13'42.897"N	078°24'45.095"E	600.6	0.5	Within RWY Strip	613.6	Clear	IN TS	-	-	-
~~6~~	~~VOHS_6063~~	~~Group of Tree~~	~~2012~~	~~2187~~	~~17°13'46.554"N~~	~~078°24'42.382"E~~	~~601.6~~	~~11.5~~	~~IN APP Funnel 09R~~	~~607.9~~	~~5.2~~	~~IN APP Funnel 09L~~	~~-~~	~~-~~	~~-~~
~~7~~	~~VOHS_6019~~	~~Group of Tree~~	~~1997~~	~~2259~~	~~17°13'46.069"N~~	~~078°24'39.810"E~~	~~603.1~~	~~5.7~~	~~IN APP Funnel 09R / TAKEOFF 27L~~	~~609.4~~	~~Clear~~	~~IN APP Funnel 09L~~	~~-~~	~~-~~	~~-~~
~~8~~	~~VOHS_6009~~	~~Bush Tree~~	~~2002~~	~~2290~~	~~17°13'45.764"N~~	~~078°24'38.753"E~~	~~603.7~~	~~6.5~~	~~IN APP Funnel 09R / TAKEOFF 27L~~	~~610.0~~	~~0.2~~	~~IN APP Funnel 09L~~	~~-~~	~~-~~	~~-~~
~~9~~	~~VOHS_6010~~	~~Bush Tree~~	~~2001~~	~~2311~~	~~17°13'45.859"N~~	~~078°24'37.872"E~~	~~604.2~~	~~5.6~~	~~IN APP Funnel 09R / TAKEOFF 27L~~	~~610.5~~	~~Clear~~	~~IN APP Funnel 09L~~	~~-~~	~~-~~	~~-~~
~~10~~	~~VOHS_6012~~	~~Bush Tree~~	~~2000~~	~~2482~~	~~17°13'45.811"N~~	~~078°24'31.146"E~~	~~608.2~~	~~1.5~~	~~IN APP Funnel 09R / TAKEOFF 27L~~	~~614.5~~	~~Clear~~	~~IN APP Funnel 09L~~	~~-~~	~~-~~	~~-~~
~~11~~	~~VOHS_6011~~	~~Bush Tree~~	~~2000~~	~~2419~~	~~17°13'45.872"N~~	~~078°24'33.565"E~~	~~606.8~~	~~2.7~~	~~IN APP Funnel 09R / TAKEOFF 27L~~	~~613.1~~	~~Clear~~	~~IN APP Funnel 09L~~	~~-~~	~~-~~	~~-~~
~~12~~	~~VOHS_6067~~	~~Group of Tree~~	~~1994~~	~~2278~~	~~17°13'48.414"N~~	~~078°24'37.531"E~~	~~605.0~~	~~2.8~~	~~IN TS~~	~~610.7~~	~~Clear~~	~~IN APP Funnel 09L~~	~~-~~	~~-~~	~~-~~
~~13~~	~~VOHS_6066~~	~~Group of Tree~~	~~2001~~	~~2275~~	~~17°13'47.363"N~~	~~078°24'38.293"E~~	~~604.0~~	~~6.0~~	~~IN APP Funnel 09R~~	~~610.3~~	~~Clear~~	~~IN APP Funnel 09L~~	~~-~~	~~-~~	~~-~~
~~14~~	~~VOHS_6065~~	~~Group of Tree~~	~~1990~~	~~2209~~	~~17°13'48.009"N~~	~~078°24'40.511"E~~	~~603.2~~	~~3.5~~	~~IN TS~~	~~609.0~~	~~Clear~~	~~IN APP Funnel 09L~~	~~-~~	~~-~~	~~-~~
~~15~~	~~VOHS_6064~~	~~Group of Tree~~	~~1997~~	~~2163~~	~~17°13'48.158"N~~	~~078°24'42.254"E~~	~~603.8~~	~~4.9~~	~~IN TS~~	~~607.9~~	~~0.8~~	~~IN APP Funnel 09L~~	~~-~~	~~-~~	~~-~~
~~16~~	~~VOHS_6068~~	~~Group of Tree~~	~~1997~~	~~2049~~	~~17°13'52.498"N~~	~~078°24'44.020"E~~	~~622.9~~	~~Clear~~	~~IN TS~~	~~606.9~~	~~1.8~~	~~IN APP Funnel 09L~~	~~-~~	~~-~~	~~-~~
~~17~~	~~VOHS_6069~~	~~Group of Tree~~	~~1994~~	~~2008~~	~~17°13'52.771"N~~	~~078°24'45.450"E~~	~~624.1~~	~~Clear~~	~~IN TS~~	~~606.0~~	~~1.9~~	~~IN APP Funnel 09L~~	~~-~~	~~-~~	~~-~~
~~18~~	~~VOHS_6070~~	~~Group of Tree~~	~~1995~~	~~1923~~	~~17°13'53.461"N~~	~~078°24'48.395"E~~	~~627.1~~	~~Clear~~	~~IN TS~~	~~604.3~~	~~3.9~~	~~IN APP Funnel 09L~~	~~-~~	~~-~~	~~-~~
19	VOHS_7028	Windsock 09 Side	1993	1836	17°13'47.956"N	078°24'56.083"E	602.8	4.6	IN TS	601.9	5.5	Within RWY Strip	-	-	-
20	VOHS_9192	PAPI Light	1975	1779	17°13'45.179"N	078°25'01.310"E	601.8	0.1	Within RWY Strip	605.9	Clear	IN TS	-	-	-
21	VOHS_4011	GP Monitor Antenna 09R	1990	2041	17°13'39.077"N	078°24'55.109"E	601.3	5.2	Within RWY Strip	631.3	Clear	IN TS	-	-	-
22	VOHS_4007	GP DME	2010	1987	17°13'39.082"N	078°24'57.721"E	601.5	11.2	Within RWY Strip	631.9	Clear	IN TS	-	-	-
23	VOHS_4005	GP Antenna 09R	2019	1986	17°13'39.125"N	078°24'57.717"E	601.5	13.9	Within RWY Strip	631.8	Clear	IN TS	-	-	-
24	VOHS_9026	CCTV on GP Hut	1981	1979	17°13'39.150"N	078°24'58.073"E	601.5	2.3	Within RWY Strip	631.7	Clear	IN TS	-	-	-
25	VOHS_9044	Lightning Arrestor	1988	1988	17°13'38.990"N	078°24'57.799"E	601.5	4.5	Within RWY Strip	632.4	Clear	IN TS	-	-	-
26	VOHS_9022	Arrester on MET Building	1986	2012	17°13'37.769"N	078°24'57.938"E	604.8	0.5	IN TS	637.7	Clear	IN TS	-	-	-
~~27~~	~~VOHS_6008~~	~~Bush Tree~~	~~1988~~	~~1975~~	~~17°13'37.982"N~~	~~078°24'59.612"E~~	~~604.0~~	~~1.8~~	~~IN TS~~	~~637.3~~	~~Clear~~	~~IN TS~~	~~-~~	~~-~~	~~-~~
28	VOHS_9048	MET Instrument	1992	1958	17°13'38.194"N	078°25'00.190"E	603.3	3.7	IN TS	636.3	Clear	IN TS	-	-	-
29	VOHS_9046	MET Antenna	2002	1930	17°13'39.068"N	078°25'00.585"E	601.7	8.5	Within RWY Strip	632.8	Clear	IN TS	-	-	-
30	VOHS_4021	RVR Antenna	1976	1924	17°13'39.213"N	078°25'00.755"E	601.7	0.6	Within RWY Strip	632.1	Clear	IN TS	-	-	-
31	VOHS_4020	RVR Antenna	1976	1944	17°13'39.204"N	078°24'59.754"E	601.6	0.7	Within RWY Strip	631.9	Clear	IN TS	-	-	-
32	VOHS_9103	Sign Board	1979	1507	17°13'44.699"N	078°25'16.512"E	602.9	0.3	Within RWY Strip	610.1	Clear	IN TS	-	-	-
33	VOHS_9102	Sign Board	1979	1396	17°13'47.168"N	078°25'19.477"E	603.1	0.2	Within RWY Strip	604.2	Clear	Within RWY Strip	-	-	-
34	VOHS_9080	Sign Board	1980	1382	17°13'47.707"N	078°25'19.482"E	603.1	0.5	Within RWY Strip	604.2	Clear	Within RWY Strip	-	-	-
35	VOHS_9079	Sign Board	1982	1291	17°13'51.937"N	078°25'18.443"E	620.7	Clear	IN TS	604.2	0.1	Within RWY Strip	-	-	-
36	VOHS_9047	MET Antenna	2011	1438	17°13'54.504"N	078°25'07.973"E	631.9	Clear	IN TS	603.5	9.6	Within RWY Strip	-	-	-
37	VOHS_9002	Obstacle Light on GP Hut RWY 09L	1992	1479	17°13'54.468"N	078°25'06.155"E	631.7	Clear	IN TS	603.3	3.9	Within RWY Strip	-	-	-
38	VOHS_4004	GP Antenna 09L	2029	1483	17°13'54.480"N	078°25'05.976"E	631.7	Clear	IN TS	603.3	15.1	Within RWY Strip	-	-	-
39	VOHS_4009	GP DME	2016	1484	17°13'54.499"N	078°25'05.902"E	631.8	Clear	IN TS	603.3	11.1	Within RWY Strip	-	-	-
40	VOHS_4010	GP Monitor Antenna	1994	1541	17°13'54.474"N	078°25'03.424"E	631.6	Clear	IN TS	603.2	4.5	Within RWY Strip	-	-	-
41	VOHS_9025	Beacon on ATC	2235	992	17°14'05.646"N	078°25'17.899"E	663.6	17.7	IN I.H.S.	-	-	-	-	-	-
42	VOHS_9005	Antenna on ATC	2258	992	17°14'05.647"N	078°25'17.903"E	663.6	24.7	IN I.H.S.	-	-	-	-	-	-
43	VOHS_9078	Sign Board	1986	1117	17°13'55.438"N	078°25'23.558"E	636.1	Clear	IN TS	605.1	0.4	IN TS	-	-	-
44	VOHS_9077	Sign Board	1983	1194	17°13'53.693"N	078°25'21.553"E	628.6	Clear	IN TS	604.3	0.2	Within RWY Strip	-	-	-
45	VOHS_9082	Sign Board	1984	1204	17°13'51.959"N	078°25'23.812"E	620.8	Clear	IN TS	604.5	0.2	Within RWY Strip	-	-	-
46	VOHS_9083	Sign Board	1984	1280	17°13'49.371"N	078°25'23.373"E	609.5	Clear	IN TS	604.5	0.2	Within RWY Strip	-	-	-
47	VOHS_9081	Sign Board	1981	1350	17°13'47.739"N	078°25'21.593"E	603.3	0.6	Within RWY Strip	604.3	Clear	Within RWY Strip	-	-	-
48	VOHS_9101	Sign Board	1980	1364	17°13'47.200"N	078°25'21.572"E	603.3	0.3	Within RWY Strip	604.3	Clear	Within RWY Strip	-	-	-
49	VOHS_9104	Sign Board	1981	1388	17°13'44.826"N	078°25'24.764"E	603.5	0.4	Within RWY Strip	610.6	Clear	IN TS	-	-	-
50	VOHS_9105	Sign Board	1983	1322	17°13'44.789"N	078°25'31.296"E	604.0	0.4	Within RWY Strip	611.6	Clear	IN TS	-	-	-
51	VOHS_9084	Sign Board	1985	1214	17°13'49.440"N	078°25'28.511"E	609.9	Clear	IN TS	604.8	0.3	Within RWY Strip	-	-	-
52	VOHS_9085	Sign Board	1986	1081	17°13'52.082"N	078°25'34.348"E	621.6	Clear	IN TS	605.1	0.2	Within RWY Strip	-	-	-
53	VOHS_9076	Sign Board	1986	1005	17°13'53.971"N	078°25'37.160"E	630.0	Clear	IN TS	605.3	0.1	Within RWY Strip	-	-	-
54	VOHS_9074	Sign Board	1989	939	17°13'55.663"N	078°25'40.287"E	637.4	Clear	IN TS	606.0	0.2	IN TS	-	-	-
55	VOHS_9075	Sign Board	1987	995	17°13'53.953"N	078°25'39.416"E	629.9	Clear	IN TS	605.4	0.2	Within RWY Strip	-	-	-
56	VOHS_9088	Sign Board	1987	1040	17°13'52.237"N	078°25'42.258"E	622.4	Clear	IN TS	605.5	0.1	Within RWY Strip	-	-	-
57	VOHS_9089	Sign Board	1988	1053	17°13'52.243"N	078°25'49.777"E	622.6	Clear	IN TS	605.8	0.2	Within RWY Strip	-	-	-
58	VOHS_9086	Sign Board	1987	1131	17°13'49.582"N	078°25'38.672"E	610.7	Clear	IN TS	605.3	0.4	Within RWY Strip	-	-	-
59	VOHS_9087	Sign Board	1989	1115	17°13'49.931"N	078°25'47.630"E	612.5	Clear	IN TS	605.7	0.5	Within RWY Strip	-	-	-
60	VOHS_9106	Sign Board	1986	1262	17°13'44.972"N	078°25'44.197"E	605.0	0.3	Within RWY Strip	612.2	Clear	IN TS	-	-	-
~~61~~	~~VOHS_5004~~	~~Bird Chaser Hut~~	~~1996~~	~~1485~~	~~17°13'38.620"N~~	~~078°25'53.550"E~~	~~608.6~~	~~Clear~~	~~IN TS~~	~~641.4~~	~~Clear~~	~~IN TS~~	~~-~~	~~-~~	~~-~~
62	VOHS_9099	Sign Board	1988	1298	17°13'45.187"N	078°25'55.116"E	605.8	0.3	Within RWY Strip	612.6	Clear	IN TS	-	-	-
63	VOHS_9100	Sign Board	1989	1316	17°13'45.299"N	078°25'57.685"E	606.0	0.2	Within RWY Strip	612.5	Clear	IN TS	-	-	-
64	VOHS_9108	Sign Board	1991	1186	17°13'50.064"N	078°25'58.480"E	613.0	Clear	IN TS	606.7	0.2	Within RWY Strip	-	-	-
65	VOHS_9109	Sign Board	1989	1258	17°13'48.172"N	078°26'00.125"E	606.1	0.2	Within RWY Strip	606.8	Clear	Within RWY Strip	-	-	-
66	VOHS_9110	Sign Board	1999	1273	17°13'52.606"N	078°26'09.359"E	625.1	Clear	IN TS	609.0	0.2	Within RWY Strip	-	-	-
67	VOHS_9111	Sign Board	2003	1322	17°13'54.430"N	078°26'14.274"E	634.1	Clear	IN TS	610.1	0.3	Within RWY Strip	-	-	-
68	VOHS_9107	Sign Board	2002	1398	17°13'50.056"N	078°26'12.868"E	614.6	Clear	IN TS	609.8	0.3	Within RWY Strip	-	-	-
69	VOHS_9098	Sign Board	1996	1488	17°13'45.378"N	078°26'11.303"E	608.0	0.3	Within RWY Strip	615.9	Clear	IN TS	-	-	-
70	VOHS_9097	Sign Board	1997	1517	17°13'45.385"N	078°26'13.073"E	608.5	0.3	Within RWY Strip	616.4	Clear	IN TS	-	-	-
71	VOHS_5005	Bird Chaser Hut	2012	1776	17°13'38.980"N	078°26'18.820"E	612.8	0.3	IN TS	646.5	Clear	IN TS	-	-	-
~~72~~	~~VOHS_5003~~	~~Bird Chaser Hut~~	~~2022~~	~~2085~~	~~17°13'39.250"N~~	~~078°26'35.030"E~~	~~617.0~~	~~Clear~~	~~IN TS~~	~~650.6~~	~~Clear~~	~~IN TS~~	~~-~~	~~-~~	~~-~~
73	VOHS_9095	Sign Board	2007	1719	17°13'45.537"N	078°26'24.076"E	611.6	0.3	Within RWY Strip	619.4	Clear	IN TS	-	-	-
74	VOHS_9096	Sign Board	2004	1631	17°13'47.458"N	078°26'21.857"E	610.8	0.2	Within RWY Strip	612.3	Clear	Within RWY Strip	-	-	-
75	VOHS_9090	Sign Board	2013	1652	17°13'50.230"N	078°26'25.639"E	618.0	Clear	IN TS	613.1	0.5	Within RWY Strip	-	-	-
76	VOHS_9091	Sign Board	2017	1767	17°13'50.297"N	078°26'30.763"E	619.4	Clear	IN TS	614.8	0.1	Within RWY Strip	-	-	-
77	VOHS_9115	Sign Board	2017	1869	17°13'48.730"N	078°26'33.861"E	614.0	0.9	Within RWY Strip	615.5	Clear	Within RWY Strip	-	-	-
78	VOHS_9093	Sign Board	2016	1886	17°13'47.915"N	078°26'33.956"E	614.0	0.6	Within RWY Strip	615.5	Clear	Within RWY Strip	-	-	-
79	VOHS_9092	Sign Board	2014	1859	17°13'45.739"N	078°26'30.845"E	613.3	0.6	Within RWY Strip	620.9	Clear	IN TS	-	-	-
80	VOHS_9094	Sign Board	2017	1934	17°13'47.947"N	078°26'36.011"E	614.6	0.2	Within RWY Strip	615.9	Clear	Within RWY Strip	-	-	-
81	VOHS_9114	Sign Board	2018	1920	17°13'48.756"N	078°26'36.059"E	614.6	0.6	Within RWY Strip	615.9	Clear	Within RWY Strip	-	-	-
82	VOHS_9113	Sign Board	2022	1912	17°13'50.378"N	078°26'36.964"E	620.9	Clear	IN TS	616.1	0.1	Within RWY Strip	-	-	-
83	VOHS_9112	Sign Board	2024	1929	17°13'52.789"N	078°26'39.308"E	632.1	Clear	IN TS	616.4	0.5	Within RWY Strip	-	-	-
84	VOHS_9073	Sign Board	2020	2047	17°13'45.852"N	078°26'39.179"E	615.3	0.5	Within RWY Strip	622.5	Clear	IN TS	-	-	-
~~85~~	~~VOHS_5002~~	~~Bird Chaser Hut~~	~~2033~~	~~2475~~	~~17°13'39.310"N~~	~~078°26'52.150"E~~	~~620.4~~	~~Clear~~	~~IN TS~~	~~653.5~~	~~Clear~~	~~IN TS~~	~~-~~	~~-~~	~~-~~
86	VOHS_4023	RVR Antenna	2029	2546	17°13'40.773"N	078°26'56.092"E	617.4	1.2	Within RWY Strip	647.9	Clear	IN TS	-	-	-
87	VOHS_9041	Lightening Arrester Near RVR	2033	2548	17°13'40.688"N	078°26'56.090"E	617.4	2.4	Within RWY Strip	648.1	Clear	IN TS	-	-	-
88	VOHS_9033	Electrical Panel	2032	2566	17°13'39.764"N	078°26'56.184"E	619.1	0.4	IN TS	652.3	Clear	IN TS	-	-	-
89	VOHS_4022	RVR Antenna	2029	2522	17°13'40.755"N	078°26'55.111"E	617.3	1.3	Within RWY Strip	647.8	Clear	IN TS	-	-	-
90	VOHS_9188	PAPI Light	2026	2460	17°13'43.211"N	078°26'54.239"E	617.2	0.2	Within RWY Strip	636.9	Clear	IN TS	-	-	-
91	VOHS_9045	MET Antenna	2056	2545	17°13'40.629"N	078°26'55.927"E	617.4	9.1	Within RWY Strip	648.4	Clear	IN TS	-	-	-
92	VOHS_9021	Arrester on MET Building	2037	2629	17°13'39.471"N	078°26'58.543"E	620.5	0.4	IN TS	653.9	Clear	IN TS	-	-	-
~~93~~	~~VOHS_6044~~	~~Group of Tree~~	~~2048~~	~~2643~~	~~17°13'39.226"N~~	~~078°26'58.937"E~~	~~621.7~~	~~2.6~~	~~IN TS~~	~~655.1~~	~~Clear~~	~~IN TS~~	~~-~~	~~-~~	~~-~~
~~94~~	~~VOHS_6045~~	~~Group of Tree~~	~~2047~~	~~2650~~	~~17°13'39.755"N~~	~~078°26'59.593"E~~	~~619.4~~	~~4.5~~	~~IN TS~~	~~652.8~~	~~Clear~~	~~IN TS~~	~~-~~	~~-~~	~~-~~
95	VOHS_4012	GP Monitor Antenna 27L	2043	2661	17°13'40.828"N	078°27'00.705"E	617.4	5.3	Within RWY Strip	648.1	Clear	IN TS	-	-	-
96	VOHS_4006	GP Antenna 27L	2072	2597	17°13'40.776"N	078°26'58.152"E	617.4	14.1	Within RWY Strip	648.2	Clear	IN TS	-	-	-
97	VOHS_5012	GP Hut	2033	2591	17°13'40.755"N	078°26'57.868"E	617.4	2.1	Within RWY Strip	648.2	Clear	IN TS	-	-	-
98	VOHS_4008	GP DME	2043	2598	17°13'40.769"N	078°26'58.163"E	617.4	5.5	Within RWY Strip	648.2	Clear	IN TS	-	-	-
99	VOHS_9060	Sign Board	2028	2717	17°13'46.191"N	078°27'06.015"E	617.5	0.6	Within RWY Strip	624.6	Clear	IN TS	-	-	-
100	VOHS_9061	Sign Board	2027	2602	17°13'46.123"N	078°27'01.596"E	617.4	0.5	Within RWY Strip	624.9	Clear	IN TS	-	-	-
101	VOHS_9059	Sign Board	2027	2479	17°13'49.027"N	078°26'58.482"E	617.4	0.4	Within RWY Strip	618.6	Clear	Within RWY Strip	-	-	-
102	VOHS_7029	Windsock 27 Side	2047	2516	17°13'49.624"N	078°27'00.174"E	618.8	5.1	IN TS	618.6	5.3	Within RWY Strip	-	-	-
103	VOHS_9058	Sign Board	2030	2481	17°13'50.685"N	078°26'59.396"E	623.5	Clear	IN TS	618.6	0.1	Within RWY Strip	-	-	-
104	VOHS_9056	Sign Board	2027	2421	17°13'49.049"N	078°26'56.253"E	617.4	0.4	Within RWY Strip	618.5	Clear	Within RWY Strip	-	-	-
105	VOHS_9054	Sign Board	2026	2389	17°13'46.036"N	078°26'53.236"E	617.1	0.5	Within RWY Strip	624.3	Clear	IN TS	-	-	-
106	VOHS_9057	Sign Board	2029	2283	17°13'53.162"N	078°26'53.222"E	634.4	Clear	IN TS	618.2	0.1	Within RWY Strip	-	-	-
107	VOHS_9055	Sign Board	2030	2437	17°13'53.318"N	078°26'59.063"E	635.1	Clear	IN TS	618.6	0.2	Within RWY Strip	-	-	-
~~108~~	~~VOHS_6078~~	~~Tree~~	~~2043~~	~~2425~~	~~17°13'54.903"N~~	~~078°26'59.318"E~~	~~642.0~~	~~Clear~~	~~IN TS~~	~~618.6~~	~~4.2~~	~~Within RWY Strip~~	~~-~~	~~-~~	~~-~~
~~109~~	~~VOHS_6049~~	~~Group of Tree~~	~~2043~~	~~2422~~	~~17°13'55.429"N~~	~~078°26'59.463"E~~	~~644.4~~	~~Clear~~	~~IN TS~~	~~618.6~~	~~4.1~~	~~Within RWY Strip~~	~~-~~	~~-~~	~~-~~
~~110~~	~~VOHS_6050~~	~~Group of Tree~~	~~2052~~	~~2401~~	~~17°13'56.749"N~~	~~078°26'59.263"E~~	~~650.1~~	~~Clear~~	~~IN TS~~	~~619.2~~	~~6.3~~	~~IN TS~~	~~-~~	~~-~~	~~-~~
~~111~~	~~VOHS_6051~~	~~Group of Tree~~	~~2056~~	~~2422~~	~~17°13'57.577"N~~	~~078°27'00.369"E~~	~~653.7~~	~~Clear~~	~~IN TS~~	~~622.7~~	~~3.9~~	~~IN TS~~	~~-~~	~~-~~	~~-~~
~~112~~	~~VOHS_6052~~	~~Group of Tree~~	~~2056~~	~~2457~~	~~17°13'57.880"N~~	~~078°27'01.745"E~~	~~655.0~~	~~Clear~~	~~IN TS~~	~~624.0~~	~~2.6~~	~~IN TS~~	~~-~~	~~-~~	~~-~~
~~113~~	~~VOHS_6053~~	~~Group of Tree~~	~~2060~~	~~2497~~	~~17°13'57.562"N~~	~~078°27'03.061"E~~	~~653.6~~	~~Clear~~	~~IN TS~~	~~622.6~~	~~5.3~~	~~IN TS~~	~~-~~	~~-~~	~~-~~
~~114~~	~~VOHS_6054~~	~~Group of Tree~~	~~2047~~	~~2536~~	~~17°13'54.890"N~~	~~078°27'03.398"E~~	~~641.7~~	~~Clear~~	~~IN TS~~	~~619.3~~	~~4.8~~	~~IN APP Funnel 27R / TAKEOFF 09L~~	~~-~~	~~-~~	~~-~~
~~115~~	~~VOHS_6026~~	~~Group of Tree~~	~~2042~~	~~2587~~	~~17°13'54.723"N~~	~~078°27'05.203"E~~	~~641.0~~	~~Clear~~	~~IN TS~~	~~620.4~~	~~2.1~~	~~IN APP Funnel 27R / TAKEOFF 09L~~	~~-~~	~~-~~	~~-~~
116	VOHS_9011	Approach Light	2030	2540	17°13'52.104"N	078°27'02.285"E	629.6	Clear	IN TS	618.6	0.1	IN APP Funnel 27R / TAKEOFF 09L	-	-	-
117	VOHS_9012	Approach Light	2030	2512	17°13'52.091"N	078°27'01.265"E	629.6	Clear	IN TS	618.6	0.1	Within RWY Strip	-	-	-
~~118~~	~~VOHS_6055~~	~~Group of Tree~~	~~2046~~	~~2629~~	~~17°13'54.677"N~~	~~078°27'06.682"E~~	~~640.7~~	~~Clear~~	~~IN TS~~	~~621.2~~	~~2.4~~	~~IN APP Funnel 27R / TAKEOFF 09L~~	~~-~~	~~-~~	~~-~~
~~119~~	~~VOHS_6048~~	~~Group of Tree~~	~~2054~~	~~2708~~	~~17°13'57.795"N~~	~~078°27'10.718"E~~	~~654.4~~	~~Clear~~	~~IN TS~~	~~623.6~~	~~2.5~~	~~IN APP Funnel 27R~~	~~-~~	~~-~~	~~-~~
~~120~~	~~VOHS_6001~~	~~Bush Tree~~	~~2048~~	~~2715~~	~~17°13'54.933"N~~	~~078°27'09.921"E~~	~~641.8~~	~~Clear~~	~~IN TS~~	~~623.2~~	~~0.9~~	~~IN APP Funnel 27R / TAKEOFF 09L~~	~~-~~	~~-~~	~~-~~
~~121~~	~~VOHS_6025~~	~~Group of Tree~~	~~2061~~	~~2813~~	~~17°13'57.574"N~~	~~078°27'14.382"E~~	~~653.0~~	~~Clear~~	~~IN TS~~	~~625.8~~	~~2.4~~	~~IN APP Funnel 27R~~	~~-~~	~~-~~	~~-~~
~~122~~	~~VOHS_6003~~	~~Bush Tree~~	~~2035~~	~~2899~~	~~17°13'49.336"N~~	~~078°27'14.282"E~~	~~618.8~~	~~1.6~~	~~IN APP Funnel 27L~~	~~625.7~~	~~Clear~~	~~IN APP Funnel 27R / TAKEOFF 09L~~	~~-~~	~~-~~	~~-~~
~~123~~	~~VOHS_6004~~	~~Bush Tree~~	~~2036~~	~~2927~~	~~17°13'48.698"N~~	~~078°27'15.037"E~~	~~619.2~~	~~1.3~~	~~IN APP Funnel 27L~~	~~626.1~~	~~Clear~~	~~IN APP Funnel 27R / TAKEOFF 09L~~	~~-~~	~~-~~	~~-~~
124	VOHS_9009	Approach Light	2028	2901	17°13'44.919"N	078°27'12.299"E	617.6	0.5	Within RWY Strip	630.3	Clear	IN TS	-	-	-
125	VOHS_9010	Approach Light	2028	2875	17°13'44.906"N	078°27'11.286"E	617.6	0.5	Within RWY Strip	630.5	Clear	IN TS	-	-	-
~~126~~	~~VOHS_6046~~	~~Group of Tree~~	~~2040~~	~~3019~~	~~17°13'42.177"N~~	~~078°27'15.317"E~~	~~619.4~~	~~2.4~~	~~IN APP Funnel 27L / TAKEOFF 09R~~	~~642.5~~	~~Clear~~	~~IN TS~~	~~-~~	~~-~~	~~-~~
~~128~~	~~VOHS_6047~~	~~Group of Tree~~	~~2053~~	~~3255~~	~~17°13'41.922"N~~	~~078°27'24.074"E~~	~~624.5~~	~~1.3~~	~~IN APP Funnel 27L / TAKEOFF 09R~~	~~643.7~~	~~Clear~~	~~IN TS~~	~~-~~	~~-~~	~~-~~
131	VOHS_9133	Obstacle Light on Pylon Mast	2184	3869	17°12'24.394"N	078°26'17.406"E	663.6	2.1	IN I.H.S.	-	-	-	-	-	-
132	VOHS_9134	Obstacle Light on Pylon Mast	2189	3815	17°12'24.454"N	078°26'09.652"E	663.6	3.7	IN I.H.S.	-	-	-	-	-	-
133	VOHS_6031	Group of Tree	2069	1197	17°15'01.409"N	078°26'00.740"E	-	-	-	-	-	-	614.6	16.0	IN TS
134	VOHS_6030	Group of Tree	2041	1199	17°15'00.461"N	078°26'02.918"E	-	-	-	-	-	-	619.2	2.9	IN TS
135	VOHS_6029	Group of Tree	2036	1240	17°15'00.899"N	078°26'04.968"E	-	-	-	-	-	-	617.7	3.0	IN TS
136	VOHS_6028	Group of Tree	2032	1351	17°15'03.357"N	078°26'07.991"E	-	-	-	-	-	-	607.0	12.3	IN TS
137	VOHS_6037	Group of Tree	2056	1562	17°15'15.811"N	078°25'54.274"E	-	-	-	-	-	-	614.7	11.9	IN TS
138	VOHS_6039	Group of Tree	2047	1611	17°15'16.129"N	078°25'59.756"E	-	-	-	-	-	-	616.8	7.1	IN TS
139	VOHS_6036	Group of Tree	2051	1526	17°15'14.535"N	078°25'54.636"E	-	-	-	-	-	-	609.0	16.1	IN TS
140	VOHS_6035	Group of Tree	2056	1478	17°15'13.030"N	078°25'54.221"E	-	-	-	-	-	-	602.4	24.3	IN TS
141	VOHS_6027	Group of Tree	2054	1506	17°15'14.345"N	078°25'51.957"E	-	-	-	-	-	-	607.8	18.1	IN TS
142	VOHS_6034	Group of Tree	2050	1513	17°15'14.804"N	078°25'50.308"E	-	-	-	-	-	-	609.6	15.2	IN TS
143	VOHS_6033	Group of Tree	2060	1551	17°15'16.125"N	078°25'49.751"E	-	-	-	-	-	-	615.5	12.4	IN TS
144	VOHS_6032	Group of Tree	2064	1636	17°15'18.928"N	078°25'49.466"E	-	-	-	-	-	-	627.6	1.6	IN TS
145	VOHS_6040	Group of Tree	2066	1610	17°15'17.948"N	078°25'50.684"E	-	-	-	-	-	-	623.7	6.1	IN TS
146	VOHS_6041	Group of Tree	2089	1623	17°15'18.144"N	078°25'52.398"E	-	-	-	-	-	-	624.6	12.1	IN TS
147	VOHS_6038	Group of Tree	2059	1598	17°15'17.185"N	078°25'53.272"E	-	-	-	-	-	-	620.5	7.1	IN TS
148	VOHS_4027	Radar on ATC	2234	989	17°14'05.637"N	078°25'18.029"E	663.6	17.4	IN I.H.S.	-	-	-	-	-	-
149	VOHS_9998B	MET Antenna	2049	2095	17°13'55.868"N	078°26'47.510"E	646.1	Clear	IN TS	617.4	7.2	Within RWY Strip	-	-	-
150	VOHS_4028	MID RVR Antenna	1991	1474	17°13'40.008"N	078°25'57.997"E	606.0	1.0	Within RWY Strip	635.8	Clear	IN TS	-	-	-

LEGEND	
AERODROME REFERENCE POINT (WGS 84) 17°14'26.002"N 078°25'43.943"E	⊕
POLE, TOWER, ANTENNA, ETC.	⊙
RAILWAY LINE	┼┼┼
POWER LINE	〰
WATERBODY	▨
ROAD	—
TREE	✳
BUILDING	■

NOTE:-

1. OBSTACLES SHOWN ARE THOSE WHICH PENETRATE THE SURFACE SPECIFIED IN ANNEX 14, VOL.1, CHAPTER 4.
2. TORA FOR RWY 09L IS 3707X45M.
3. TORA FOR RWY 27R IS 3707X45M.
4. TORA FOR RWY 09R IS 4260X60M.
5. TORA FOR RWY 27L IS 4260X60M.
6. TORA FOR RWY 10 IS 4260X60M.
7. TORA FOR RWY 28 IS 4260X60M.
8. TO BRING CLARITY IN THE OBSTACLES DEPICTED IN THE APPROACH AND TAKE-OFF SURFACES, ONLY THE HIGHER OBJECTS FROM GROUP OF OBSTACLES HAVE BEEN SHOWN.
9. MAG BEARING ROUNDED TO NEAREST 15 MINUTE.
10. FEATURES SOURCE: ESRI TOPOGRAPHIC MAP.
11. MAG. DECLINATION AS PER EPOCH CHART 2010.
12. OBJECT UNDER SR. NO. 1, 2, 3, 6, 7, 8, 9, 10, 11, 12, 13, 14, 15, 16, 17, 18, 27, 61, 72, 85, 93, 94, 108, 109, 110, 111, 112, 113, 114, 115, 118, 119, 120, 121, 122, 123, 126 AND 128 HAVE BEEN REMOVED ON GROUND DURING THE COURSE OF V & V SURVEY NOVEMBER 2023.HENCE THESE SR. NO. ARE REMOVED FROM THE CHART.
13. OBSTACLES OF TYPE A CHART UNDER SR. NO. 127, 129 & 130 HAVE BEEN REMOVED FROM THE CHART.

ORDER OF ACCURACY

HORIZONTAL - 3.0m

VERTICAL - 1Ft

AMENDMENT RECORDS		
NO.	DATE	ENTERED BY

CONSULTANT:	**ADL Coordinates Pvt. Ltd.**	Phone No.: 0253-2353407
CLIENT:	INDIA / SHAMSHABAD (HYDERABAD) RGI AIRPORT	
PROJECT:-	AERONAUTICAL SURVEY OF SHAMSHABAD (HYDERABAD) RGI AIRPORT	
TITLE:-	AERODROME OBSTACLE CHART-TYPE B	
SCALE:-	1:20000	DRG.NO:- ADL/AV/RGI/DRG/TYPE B CHART/97-20
PERIOD OF SURVEY:-	INITIAL/ FULL SURVEY :- 19 NOV 2020 TO 18 DEC 2020. 1ST BI-ANNUAL VALIDATION SURVEY :- 19 JUNE 2023 TO 07 JULY 2023.	
SURVEYED BY	P.PAGARE	
DRAWN BY	D.WAGH	
CHECKED BY	M.ADHAV	

SHAMSHABAD
(HYDERABAD), INDIA
RAJIV GANDHI INTL. AIRPORT