
DEPARTURE RUNWAY 09L

TAKE - OFF RUN AVAILABLE FROM DIFFERENT RUNWAY INTERSECTION

N

RUNWAY 09L				
ENTRY TAXIWAYS	B6	B5	B4	B3
TORA (M)	2948	2421	1960	1390
ANGLE WITH ENTRY TWY WITH THE RWY IN USE	90°	90°	90°	90°
LENGTH OF TWY (M)	175	175	175	175

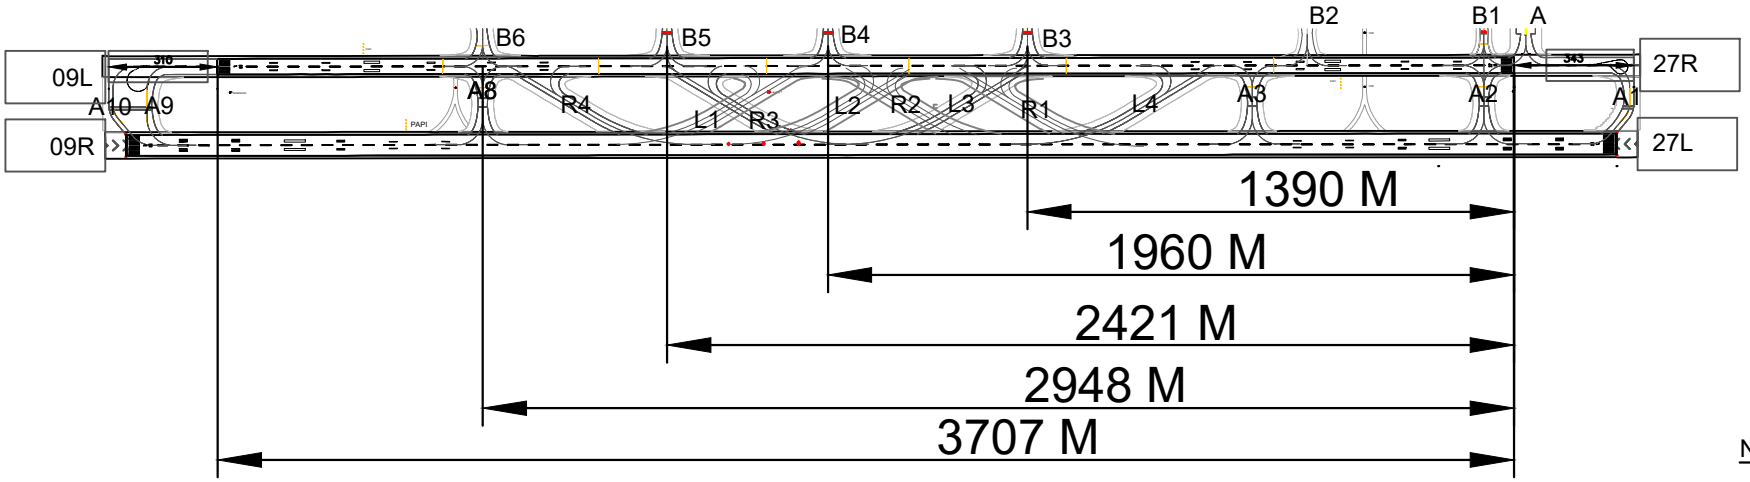

NOT TO SCALE