
AIRCRAFT PARKING/
DOCKING CHART

APRON ELEV. 5066ft
NEW APRON ELEV. 5071ft

TWR 118.350

SHIMLA, INDIA

SHIMLA AIRPORT

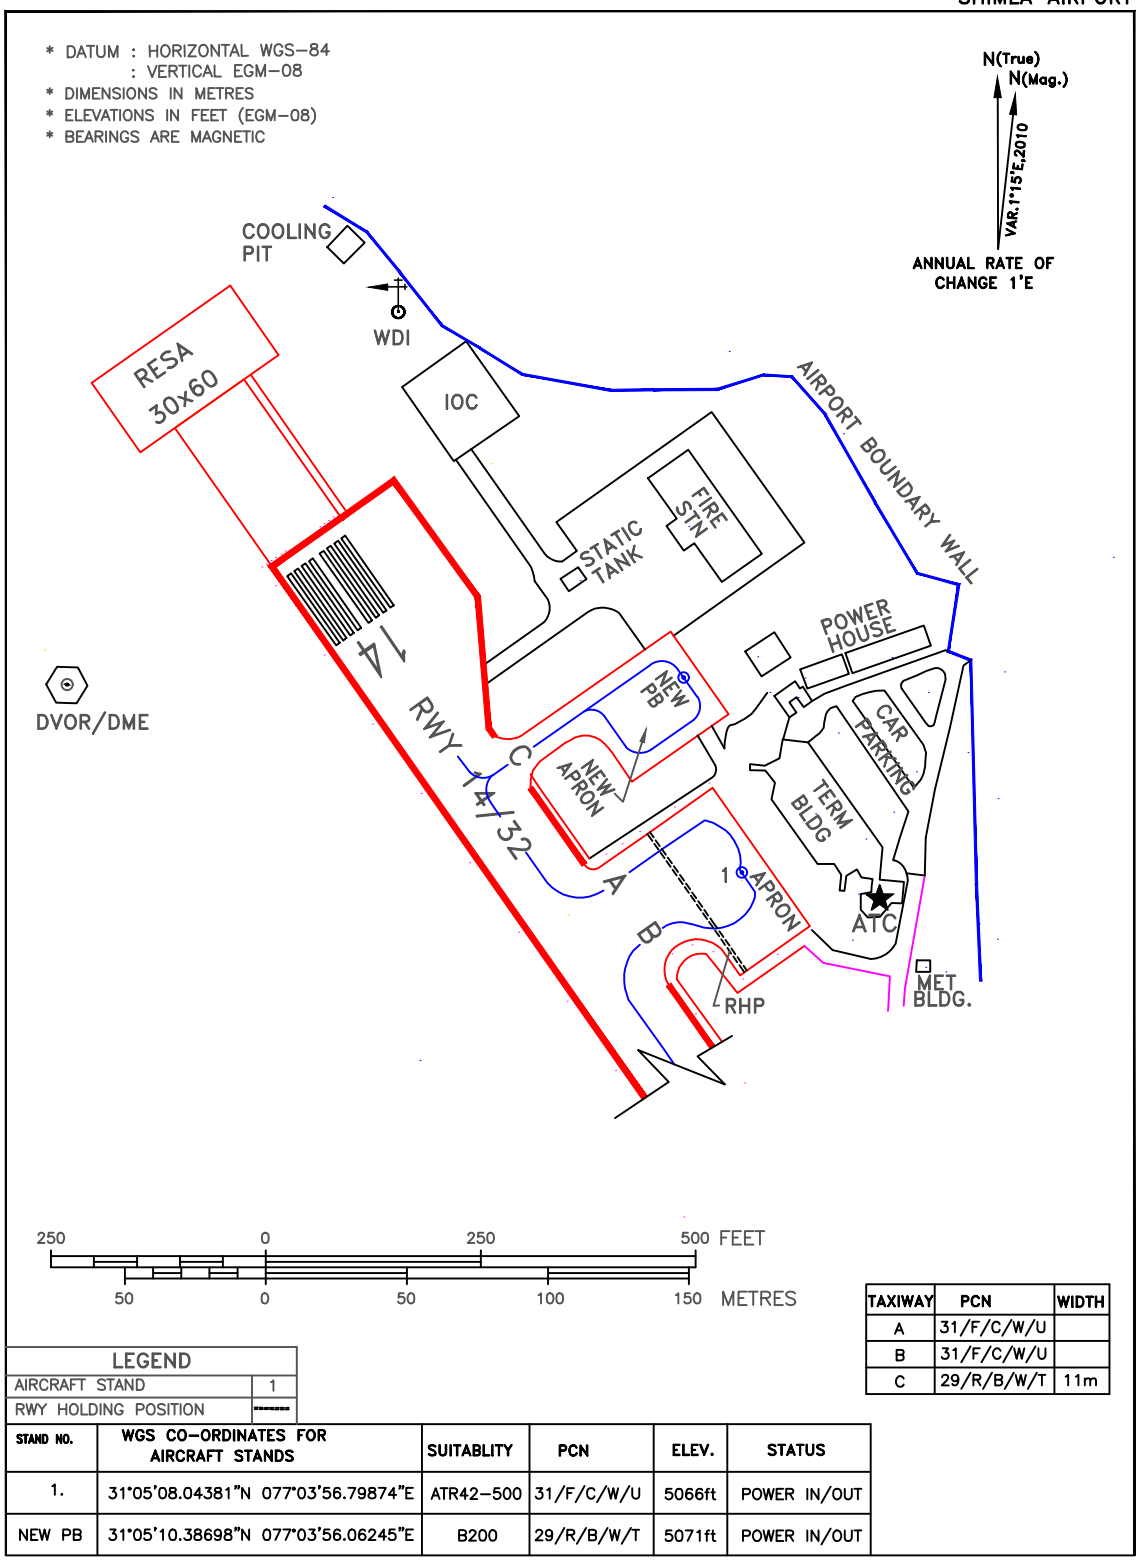

TAXIWAY	PCN	WIDTH
A	31/F/C/W/U	
B	31/F/C/W/U	
C	29/R/B/W/T	11m

LEGEND	
AIRCRAFT STAND	1
RWY HOLDING POSITION	------

STAND NO.	WGS CO–ORDINATES FOR AIRCRAFT STANDS	SUITABLITY	PCN	ELEV.	STATUS
1.	31°05'08.04381"N 077°03'56.79874"E	ATR42–500	31/F/C/W/U	5066ft	POWER IN/OUT
NEW PB	31°05'10.38698"N 077°03'56.06245"E	B200	29/R/B/W/T	5071ft	POWER IN/OUT

DATE OF AERONAUTICAL INFORMATION
MARCH 2021

DRG.No. AAI/02–PDC/2021

UPDATED AS ON 21.07.2025