
ELEVATIONS IN FEET AND EGM-08
ALL OTHER DIMENSIONS IN METRES

AERODROME OBSTACLE CHART
TYPE –A (OPERATING LIMITATIONS)

INDIA / SOLAPUR
SOLAPUR AIRPORT / RWY 33

MAGNETIC VARIATION 1°W (2010)

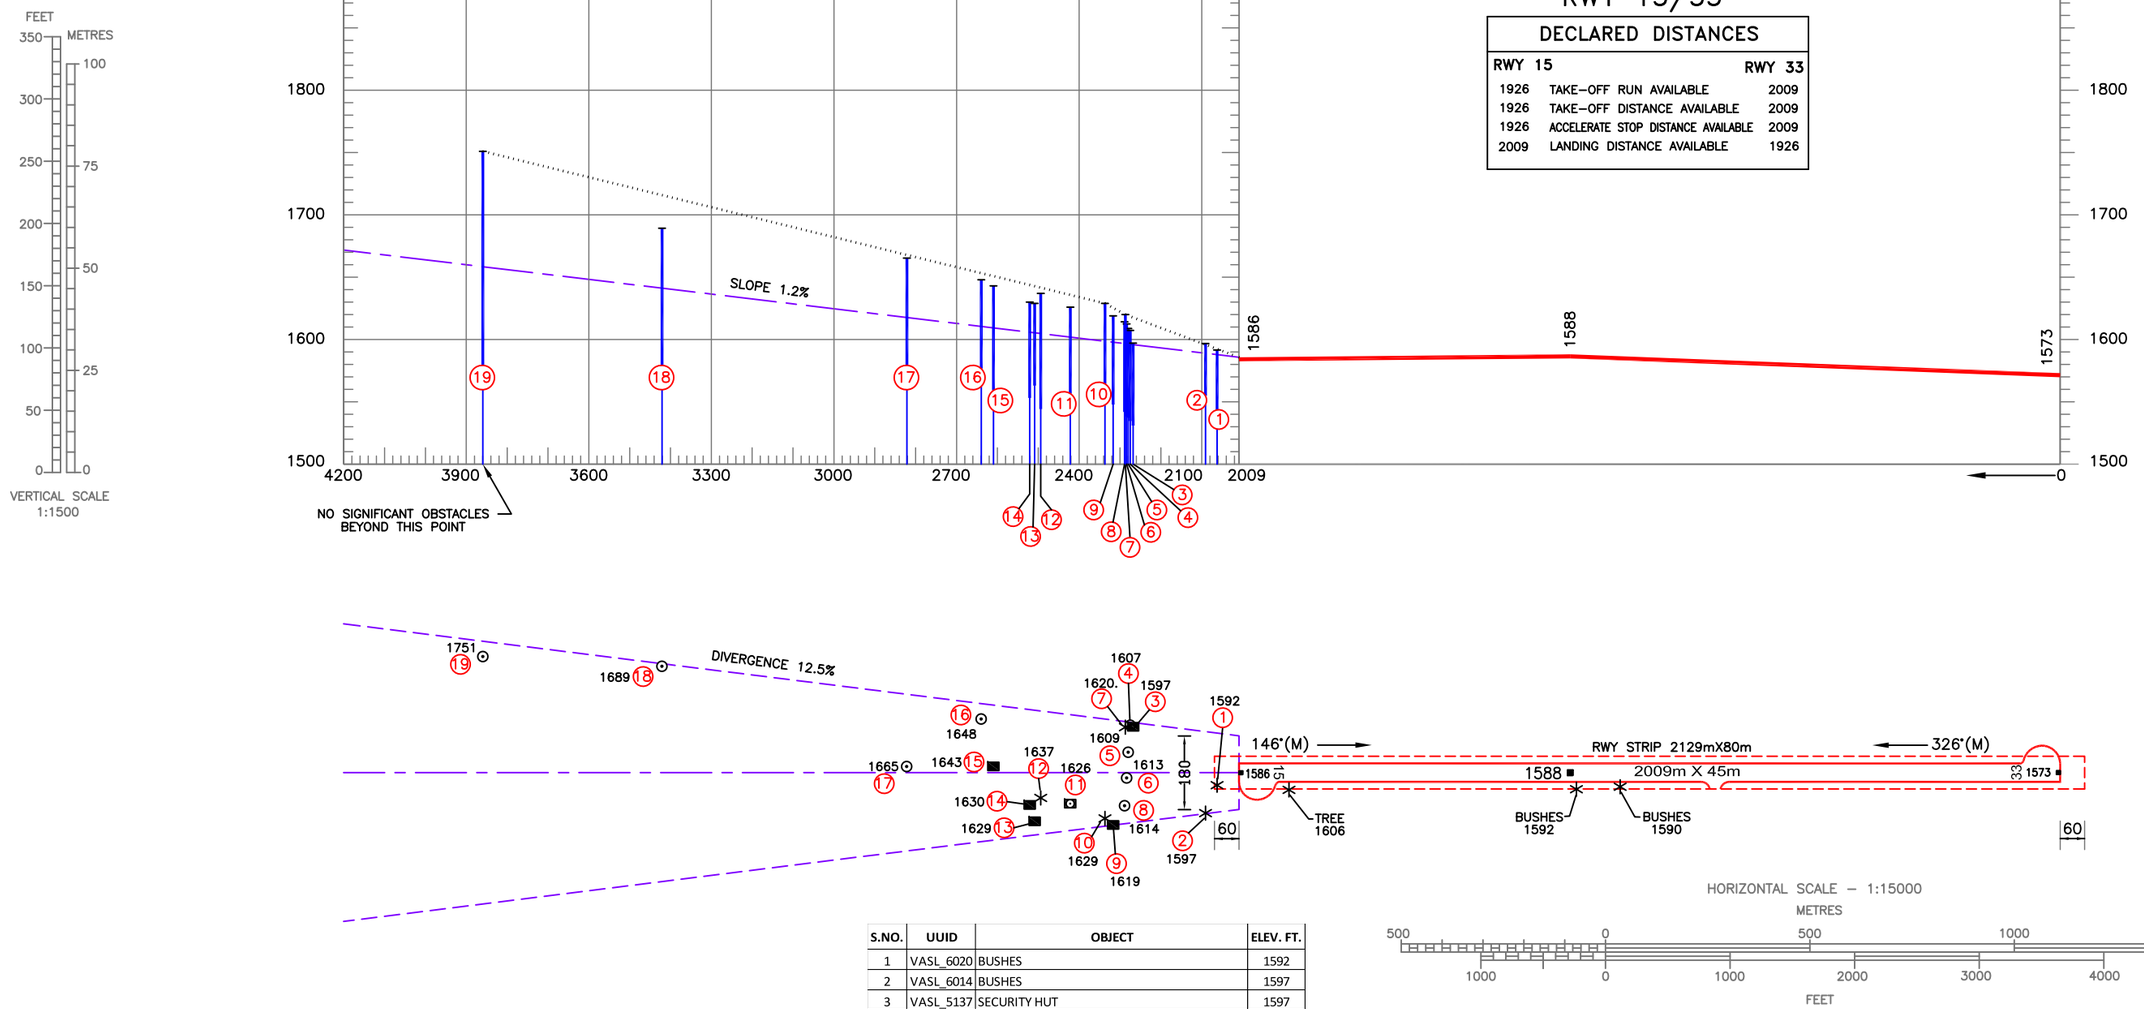

L E G E N D

	PLAN	PROFILE
IDENTIFICATION NUMBER	(17)	
TREE OR BUSHES	✳	
POLE,CHIMNEY,MAST,ANTENNA ETC.	⊙	
BUILDING,STRUCTURE	■	
TANK ON BUILDING,STRUCTURE	◘	
RWY ELEV. (SPOT)	1588■	

ORDER OF ACCURACY

HORIZONTAL	– 3.0m
VERTICAL	– 1ft.

S.NO.	UUID	OBJECT	ELEV. FT.
1	VASL_6020	BUSHES	1592
2	VASL_6014	BUSHES	1597
3	VASL_5137	SECURITY HUT	1597
4	VASL_7071	ELECTRIC POLE	1607
5	VASL_7062	ELECTRIC POLE	1609
6	VASL_7059	ELECTRIC POLE	1613
7	VASL_6019	GROUP OF TREE	1620
8	VASL_7057	ELECTRIC POLE	1614
9	VASL_5093	BUILDING	1619
10	VASL_6007	GROUP OF TREE	1629
11	VASL_5092	SINTEX ON BUILDING (BUILDING TOP 494.8M)	1626
12	VASL_6003	GROUP OF TREE	1637
13	VASL_5077	BUILDING	1629
14	VASL_5081	BUILDING	1630
15	VASL_5221	MOSQUE	1643
16	VASL_7055	FLOOD LIGHT MAST	1648
17	VASL_7041	MAST	1665
18	VASL_9015	L/A ON BUILDING (BUILDING TOP 514.3M)	1689
19	VASL_7030	MAST	1751

NOTES:–

1. The objects that have been shielded due to presence of other higher objects have not been shown in this chart.
2. Datum – All Elevations are in EGM–08.
3. Periphery road without traffic is no obstacle.
4. Consult Notam for latest information.
5. Rwy directions rounded to nearest degree.(Magnetic)
   (In degree minute : Rwy 15/33=145°59'/325°59')(2010)
   (In degree minute : Rwy 15/33=145°35'/325°35')(2022)
6. Magnetic Variation rounded to nearest degree 1°00'W, Annual rate of change 02'E (2010).
7. All obstacles shown in this chart are based on aeronautical obstacle Survey Nov. 2022.
8. Chart prepared based on DGCA CAR section 9 AS & ATM Series 'G', Part–1.

AMENDMENT RECORD

NO.	DATE	ENTERED BY

AERONAUTICAL INFORMATION UPTO – AUG. 2023

COMPILED BY– CARTO, AIRPORTS AUTHORITY OF INDIA

CHART No. AAI/54–OBS/CARTO/2024

(UPDATED ON 30.07.2024)