AERODROME ELEVATION 1588FT.


DISTANCE IN METRE.
ELEVATION IN FEET(EGM-08).
GRID LINES AND CO-ORDINATES SHOWN ARE BASED ON WGS-84 DATUM.
UTM ZONE-43N

AERODROME OBSTACLE CHART

TYPE - B

SOLAPUR,INDIA

SOLAPUR AIRPORT

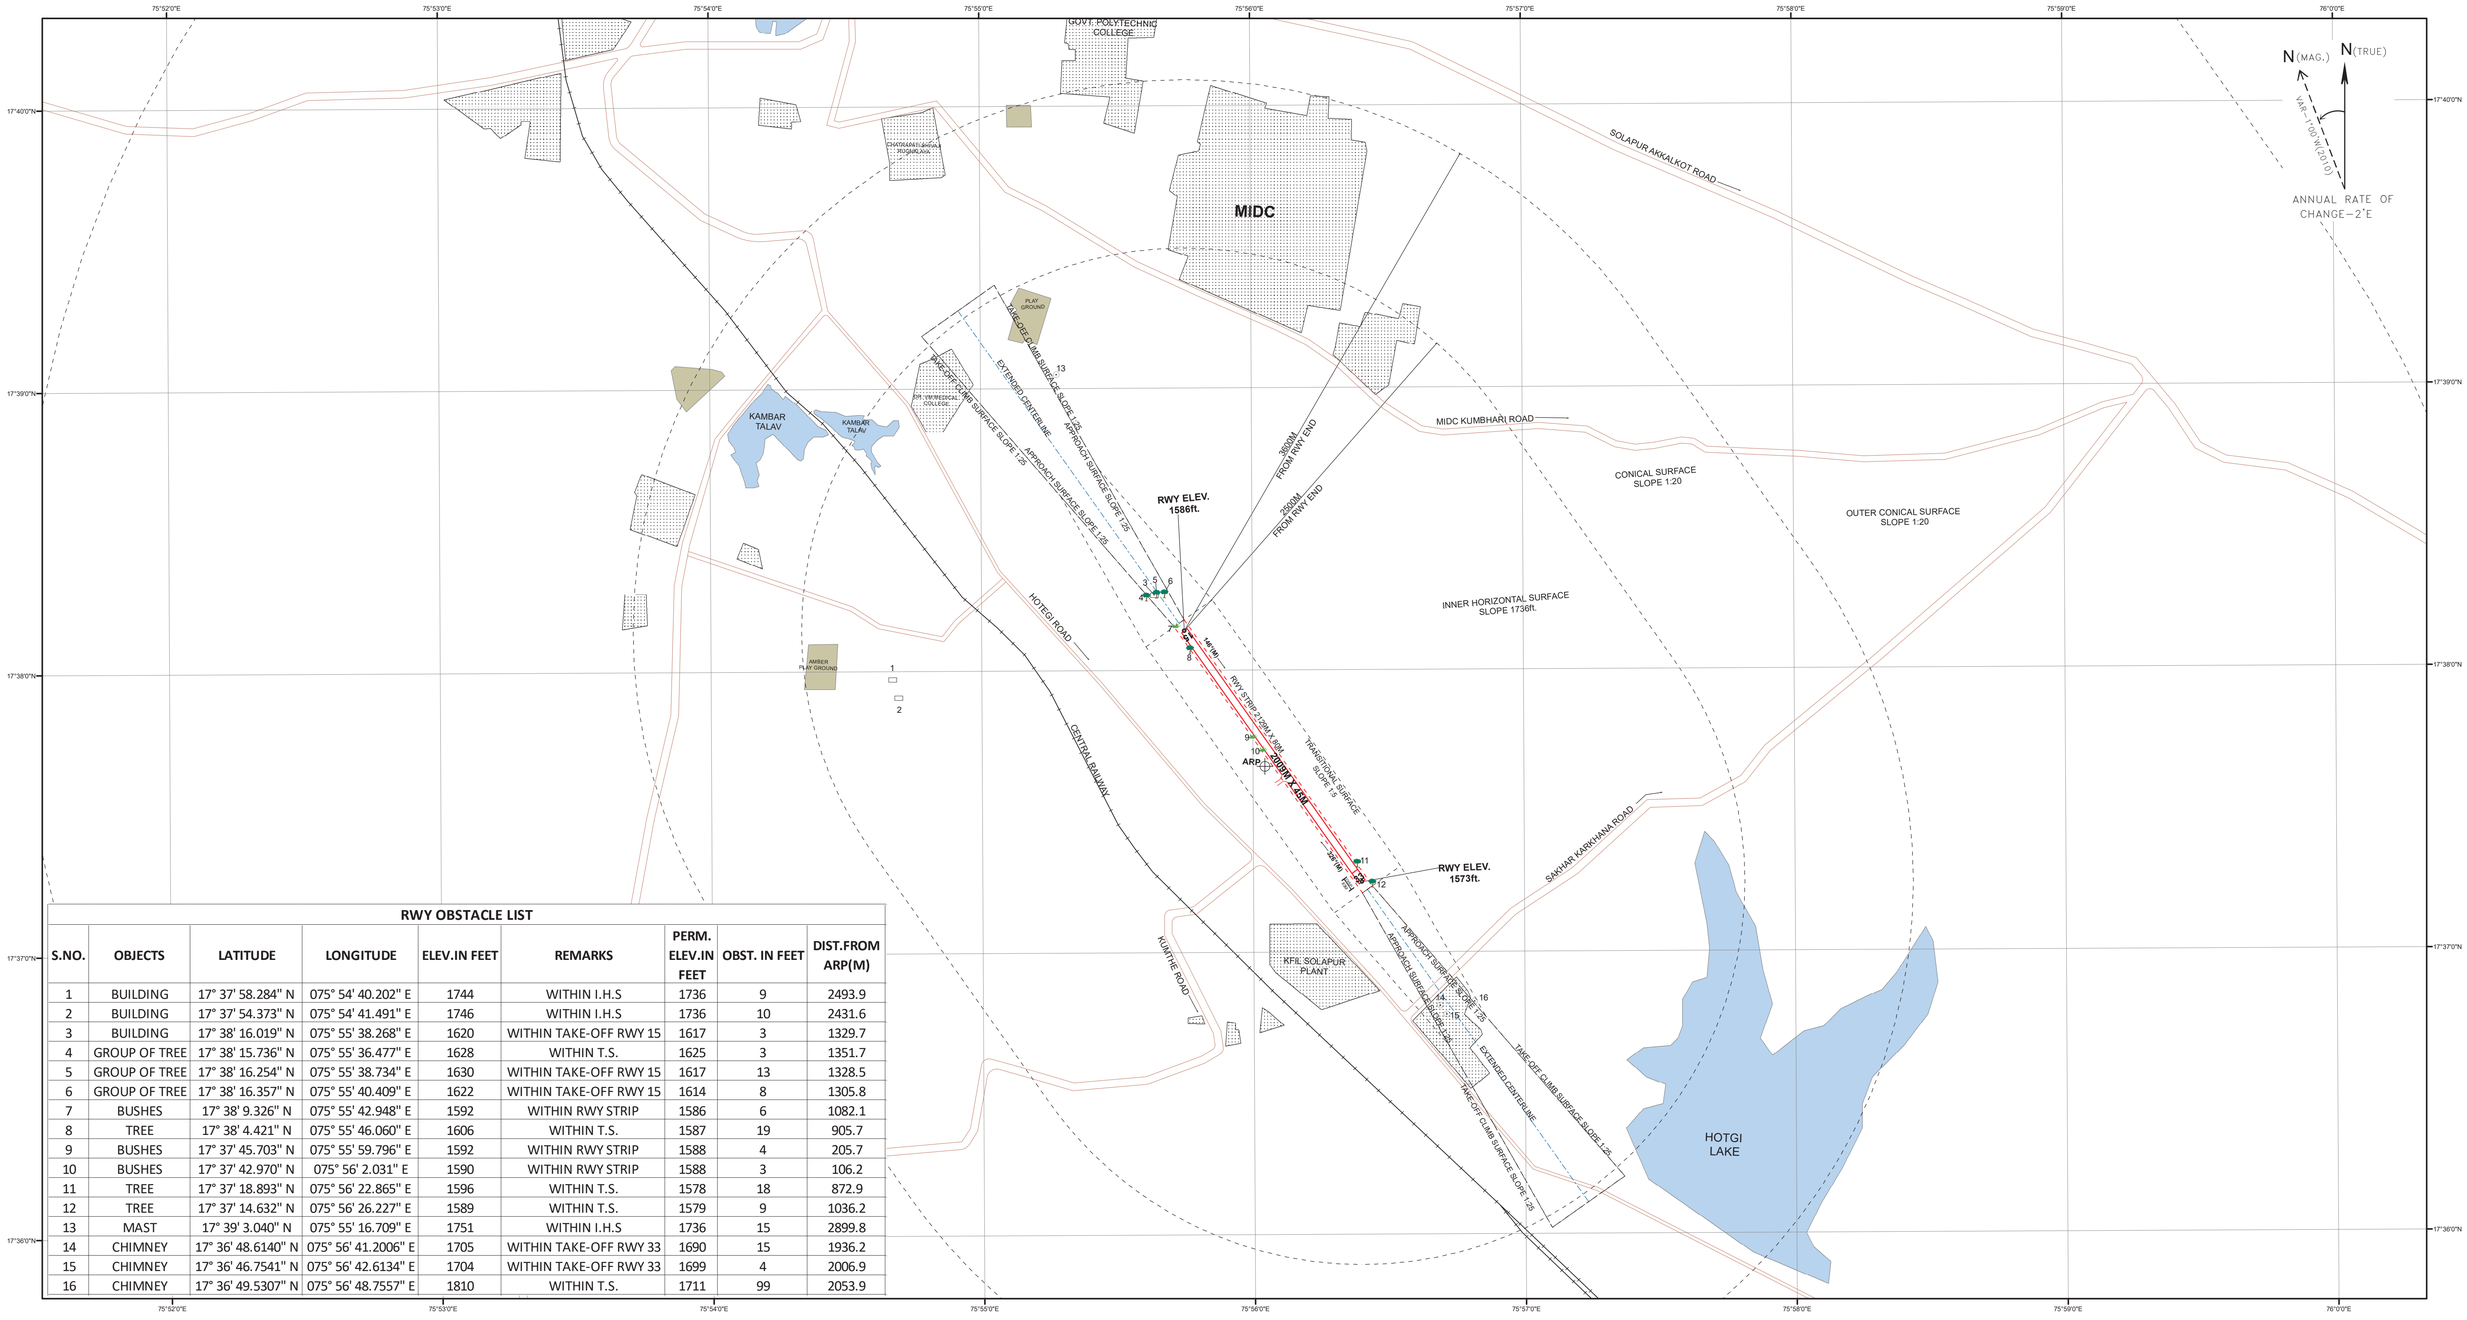

RWY OBSTACLE LIST

S.NO.	OBJECTS	LATITUDE	LONGITUDE	ELEV.IN FEET	REMARKS	PERM. ELEV.IN FEET	OBST. IN FEET	DIST.FROM ARP(M)
1	BUILDING	17° 37' 58.284" N	075° 54' 40.202" E	1744	WITHIN I.H.S	1736	9	2493.9
2	BUILDING	17° 37' 54.373" N	075° 54' 41.491" E	1746	WITHIN I.H.S	1736	10	2431.6
3	BUILDING	17° 38' 16.019" N	075° 55' 38.268" E	1620	WITHIN TAKE-OFF RWY 15	1617	3	1329.7
4	GROUP OF TREE	17° 38' 15.736" N	075° 55' 36.477" E	1628	WITHIN T.S.	1625	3	1351.7
5	GROUP OF TREE	17° 38' 16.254" N	075° 55' 38.734" E	1630	WITHIN TAKE-OFF RWY 15	1617	13	1328.5
6	GROUP OF TREE	17° 38' 16.357" N	075° 55' 40.409" E	1622	WITHIN TAKE-OFF RWY 15	1614	8	1305.8
7	BUSHES	17° 38' 9.326" N	075° 55' 42.948" E	1592	WITHIN RWY STRIP	1586	6	1082.1
8	TREE	17° 38' 4.421" N	075° 55' 46.060" E	1606	WITHIN T.S.	1587	19	905.7
9	BUSHES	17° 37' 45.703" N	075° 55' 59.796" E	1592	WITHIN RWY STRIP	1588	4	205.7
10	BUSHES	17° 37' 42.970" N	075° 56' 2.031" E	1590	WITHIN RWY STRIP	1588	3	106.2
11	TREE	17° 37' 18.893" N	075° 56' 22.865" E	1596	WITHIN T.S.	1578	18	872.9
12	TREE	17° 37' 14.632" N	075° 56' 26.227" E	1589	WITHIN T.S.	1579	9	1036.2
13	MAST	17° 39' 3.040" N	075° 55' 16.709" E	1751	WITHIN I.H.S	1736	15	2899.8
14	CHIMNEY	17° 36' 48.6140" N	075° 56' 41.2006" E	1705	WITHIN TAKE-OFF RWY 33	1690	15	1936.2
15	CHIMNEY	17° 36' 46.7541" N	075° 56' 42.6134" E	1704	WITHIN TAKE-OFF RWY 33	1699	4	2006.9
16	CHIMNEY	17° 36' 49.5307" N	075° 56' 48.7557" E	1810	WITHIN T.S.	1711	99	2053.9

LEGEND

AERODROME REFERENCE POINT 17°37'39.5483"N 075°56'02.5393"E	⊕
RAILWAY TRACK	
ROADS	
WATERBODIES	
BUILD-UP AREA	
PARKS	

ORDER OF ACCURACY	
TAKE-OFF AND APPROACH AREAS	
HORIZONTAL	REMARK
5M	AT POINT OF ORIGIN INCREASING AT A RATE OF 1 PER 500.
VERTICAL	REMARK
0.5M	IN THE FIRST 300M AND INCREASING AT A RATE OF 1 PER 1000.
OTHER AREAS	
HORIZONTAL	REMARK
5M	WITHIN 5000M OF THE ARP AND 12M BEYOND THAT AREA.
VERTICAL	REMARK
1M	WITHIN 1500M OF THE ARP INCREASING AT A RATE OF 1 PER 1000.

SCALE 1:20,000

METRES
400 0 400 800 1200 1600 2000

FEET
1400 0 1400 2800 4200 5600 7000

NOTE :

1.OBSTACLES SHOWN ARE THOSE WHICH PENETRATE THE SURFACES SPECIFIED IN ANNEX 14, VOL-1, CHAPTER-4 & GSR.
2.TORA FOR RWY 15 IS 1926M. TORA FOR RWY33 IS 2009M.
3.TO BRING OUT THE CLEARITY IN THE OBSTACLES DEPICTED IN THE APPROACH AND TAKE-OFF SURFACE, ONLY HIGHER OBSTACLES HAVE BEEN SHOWN FROM GROUP OF OBSTACLES.
4.ALL OBSTACLES ARE SHOWN IN THE CHART BASED ON AERONAUTICAL SURVEY NOV, 2022.
5.TOPOGRAPHIC FEATURES SOURCE- WORLD TOPO MAP, ESRI.

AMENDMENT RECORD		
NO.	DATE	ENTERED BY

AERONAUTICAL INFORMATION UPTO:JUNE 2024

COMPILED BY:CARTO, AIRPORTS AUTHORITY OF INDIA

AAI DRG.NO.- 32/SOLAPUR/2024(CARTO)