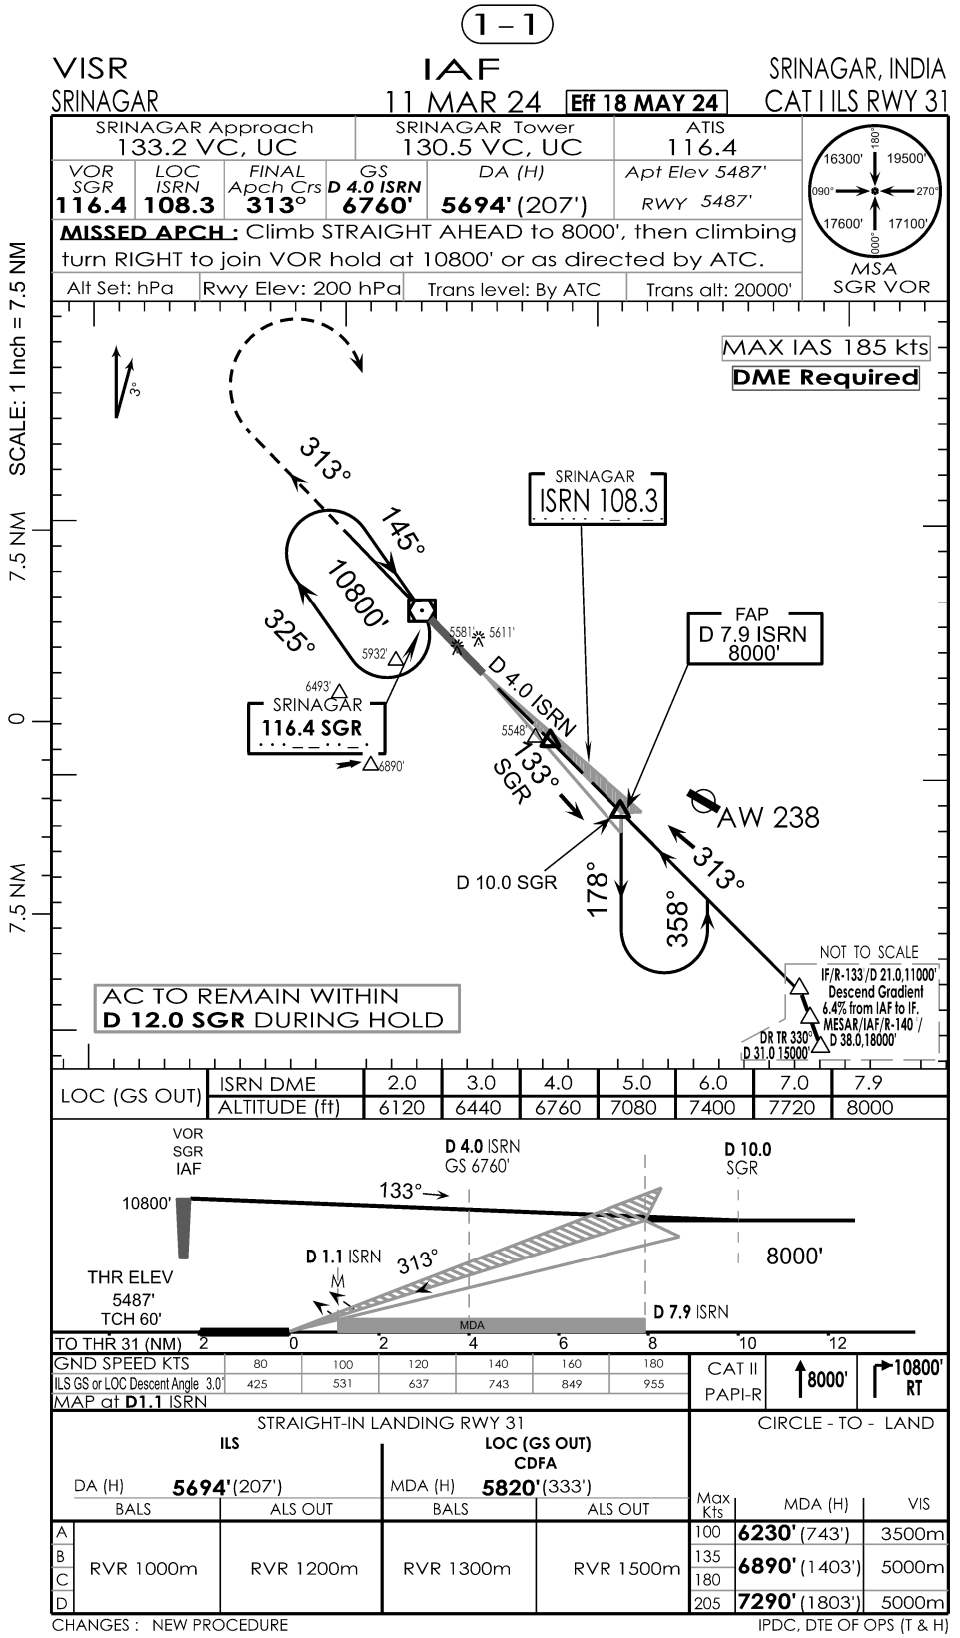

1 – 1
VISR
SRINAGAR
IAF
11 MAR 24
Eff 18 MAY 24
SRINAGAR, INDIA
CAT I ILS RWY 31
SRINAGAR Approach
133.2 VC, UC
SRINAGAR Tower
130.5 VC, UC
ATIS
116.4
VOR SGR 116.4
LOC ISRN 108.3
FINAL Apch Crs 313°
GS D 4.0 ISRN 6760'
DA (H) 5694' (207')
Apt Elev 5487'
RWY 5487'
MISSED APCH : Climb STRAIGHT AHEAD to 8000', then climbing turn RIGHT to join VOR hold at 10800' or as directed by ATC.
Alt Set: hPa
Rwy Elev: 200 hPa
Trans level: By ATC
Trans alt: 20000'
16300'
19500'
17600'
17100'
MSA
SGR VOR
SCALE: 1 Inch = 7.5 NM
7.5 NM
0
7.5 NM
SURVEY PERIOD : 2022-23 & 2023-24
MAX IAS 185 kts
DME Required
313°
145°
10800'
325°
SRINAGAR
ISRN 108.3
FAP
D 7.9 ISRN
8000'
D 4.0 ISRN
SRINAGAR
116.4 SGR
133°
SGR
AW 238
313°
D 10.0 SGR
178°
358°
NOT TO SCALE
IF/R-133/D 21.0,11000'
Descend Gradient
6.4% from IAF to IF.
MESAR/IAF/R-140 /
D 38.0,18000'
DR TR 330°
D 31.0 15000'
AC TO REMAIN WITHIN
D 12.0 SGR DURING HOLD
LOC (GS OUT)
ISRN DME 2.0 3.0 4.0 5.0 6.0 7.0 7.9
ALTITUDE (ft) 6120 6440 6760 7080 7400 7720 8000
VOR SGR IAF
10800'
D 4.0 ISRN GS 6760'
133°
D 10.0 SGR
8000'
D 1.1 ISRN
313°
THR ELEV 5487'
TCH 60'
MDA
D 7.9 ISRN
TO THR 31 (NM) 2 0 2 4 6 8 10 12
GND SPEED KTS 80 100 120 140 160 180
ILS GS or LOC Descent Angle 3.0° 425 531 637 743 849 955
MAP at D1.1 ISRN
CAT II
PAPI-R
8000'
10800' RT
STRAIGHT-IN LANDING RWY 31
ILS
LOC (GS OUT)
CDFA
DA (H) 5694' (207')
MDA (H) 5820' (333')
BALS
ALS OUT
BALS
ALS OUT
A
B
C
D
RVR 1000m
RVR 1200m
RVR 1300m
RVR 1500m
CIRCLE - TO - LAND
Max Kts
MDA (H)
VIS
100 6230' (743') 3500m
135 180 6890' (1403') 5000m
205 7290' (1803') 5000m
CHANGES : NEW PROCEDURE
IPDC, DTE OF OPS (T & H)